# ДИЗАЙН-ПРОЕКТ

## Квартира № 72 · ЖК Buta Zaman · г. Алматы

Студия 37,4 м² (1 комн., тип 1, этаж 2–7) · высота потолка 2,88 м

Стиль: минимализм · спальня за стеклянной раздвижной перегородкой · шкаф-купе в прихожей · ванна · тёплый пол в прихожей и санузле


### Состав альбома

2. Обмерный план
3. Планировочное решение
4. План монтажа перегородок
5. Напольные покрытия
6. План осветительных приборов
7. План розеток
8. План выключателей
9. План потолка
10. План сантехнического оборудования
11. План радиаторов и тёплых полов
12. Развёртка стен: кухня
13. Развёртка стен: санузел
14. Развёртка стен: прихожая
15. Развёртка стен: гостиная
16. Развёртка стен: спальня
17. Мебель: схема
18. Мебель: размеры для мебельщика
19. Визуализация 1
20. Визуализация 2
21. Ведомость материалов
22. Смета

Исполнитель: Claude (ИИ-ассистент) по заданию владельца · 26.10.2026 · Не является официальной проектной документацией: нормы и сечения проверяют исполнители работ.

# Обмерный план

**КВАРТИРА** 72

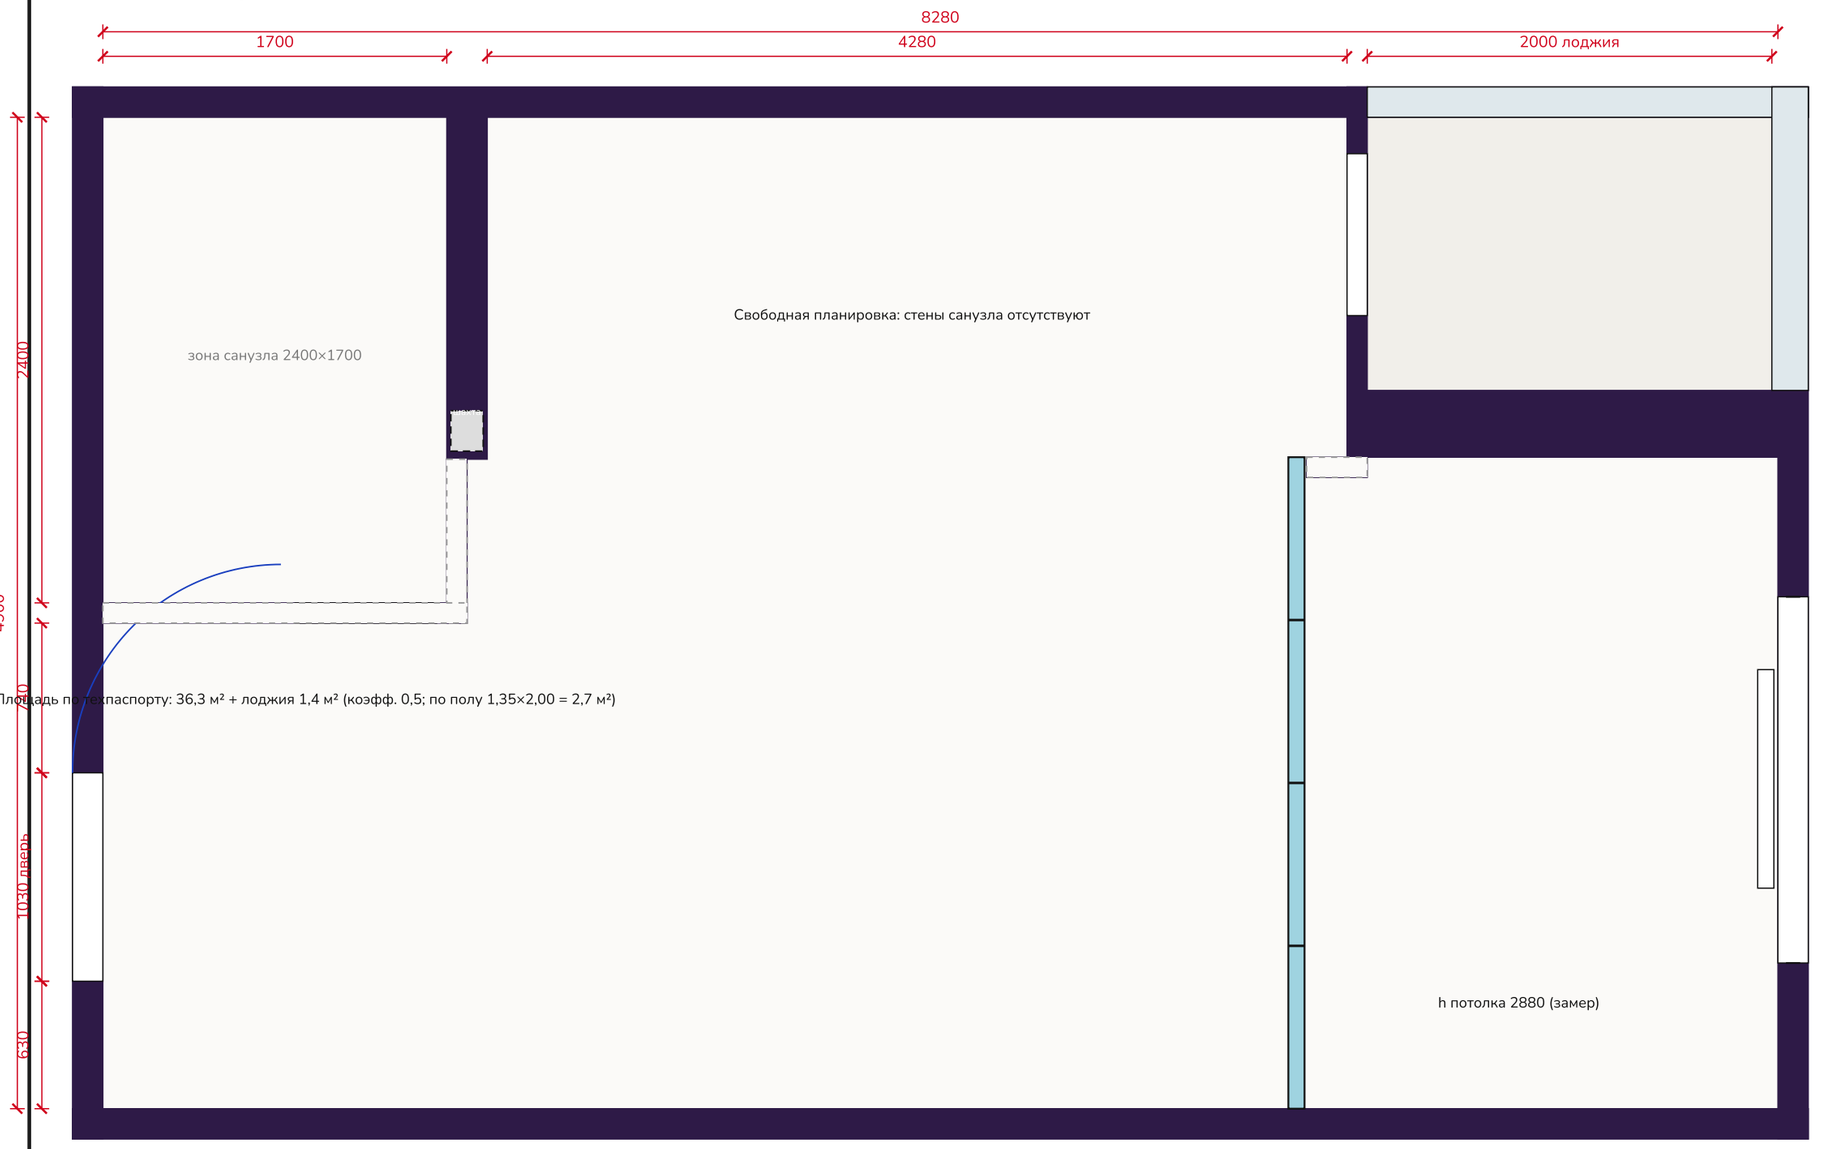


**Условные обозначения**

- Несущие стены (монолит)
- Возводимые перегородки (газоблок 100 мм)
- Стеклянная раздвижная перегородка
- Стояки / вентканал

Площадь по техпаспорту: 36,3 м² + лоджия 1,4 м² (коэфф. 0,5; по полу 1,35×2,00 = 2,7 м²)


**ПРИМЕЧАНИЯ:**

1. За отметку 0.000 принят уровень чистового пола.
2. Все размеры уточнить по месту перед началом работ; привязки даны по неоштукатуренным стенам.
3. Положение короба стояков и вентканала уточнить после приёмки квартиры 10.10.2026.
4. Размеры в миллиметрах, площади в м².
5. Замер 26.10.2026: 4,90×8,28; готовый выступ 1690×200 в 1700 от входа (ниша 1650×1700 со стояками); лоджия внутри 1350×2000 (по техпаспорту), дверь 800, стена к спальне ~330; окно 1810, простенки 720 и 700.
6. Входная дверь 1030 в 630 от правого угла (открывается наружу). Потолок 2880. От выступа до балкона 4280.

| Стадия | Лист | Листов | Квартира 72 · ЖК Buta Zaman · Алматы |
|---|---|---|---|
| РД | 2 | 22 | Обмерный план<br>26.10.2026 · М 1:30 · А3 |

# Планировочное решение

**КВАРТИРА** 72

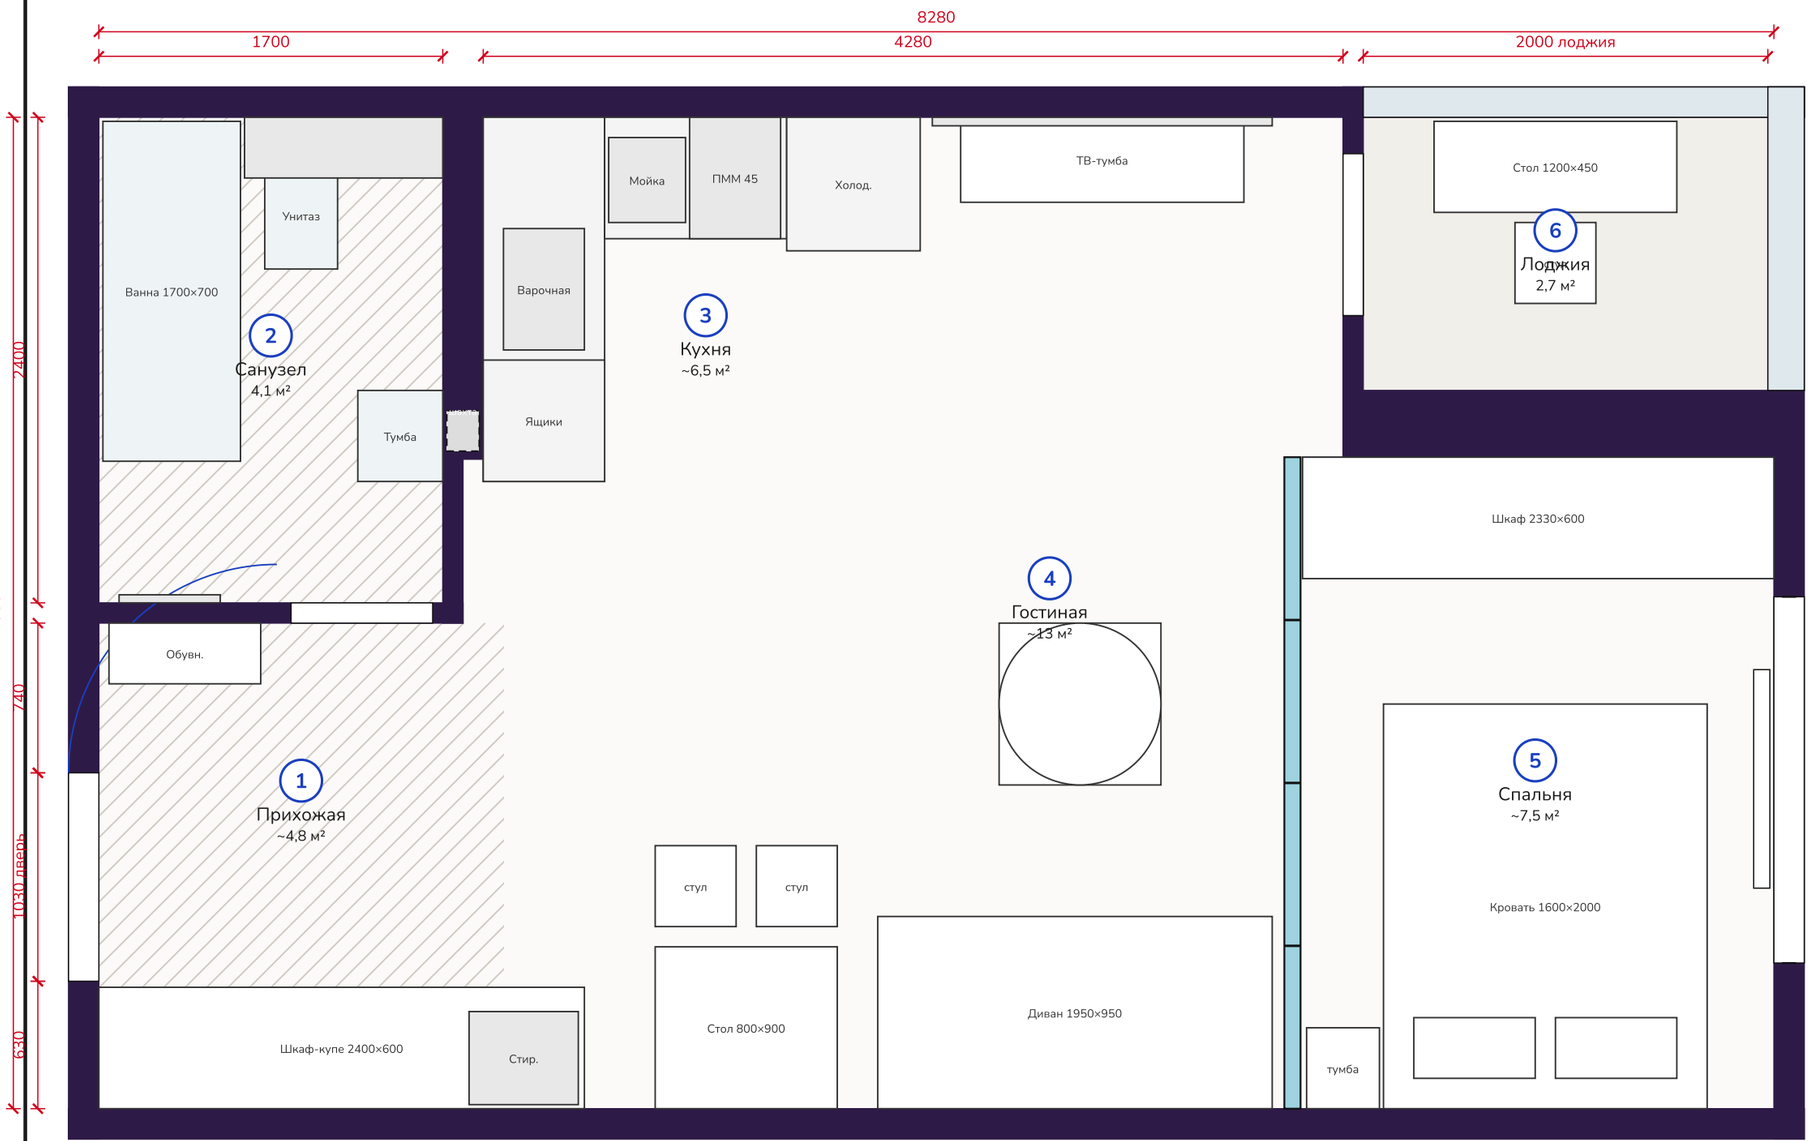


## Спецификация помещений

| № | Помещение | Площадь |
|---|---|---|
| 1 | Прихожая | ~4,8 м² |
| 2 | Санузел | 4,1 м² |
| 3 | Кухня | ~6,5 м² |
| 4 | Гостиная | ~13 м² |
| 5 | Спальня | ~7,5 м² |
| 6 | Лоджия | 2,7 м² |
| | Итого по техпаспорту | 37,4 м² |

## Покрытия пола:

Ламинат 33 кл. — кухня, гостиная, спальня (~27 м²)

Керамогранит: прихожая 200×200 PM213460 (~5 м²), санузел 600×600 (~4 м²)

Лоджия — керамогранит или плитка (~2,7 м²)


## ПРИМЕЧАНИЯ:

1. За отметку 0.000 принят уровень чистового пола.
2. Все размеры уточнить по месту перед началом работ; привязки даны по неоштукатуренным стенам.
3. Положение короба стояков и вентканала уточнить после приёмки квартиры 10.10.2026.
4. Размеры в миллиметрах, площади в м².
5. Перегородка спальни: 4 раздвижные стеклянные створки в чёрном профиле с переплётом, до потолка, с тюлем со стороны спальни.
6. Спальня: шкаф 2330×600 до потолка вдоль левой стены (4 двери), подоконник-полка 300 мм на h=950 (окно 950–2580), скрытый карниз в потолке. Балкон: рабочий стол 1200×450 с полками вдоль остекления.

| Стадия | Лист | Листов | Квартира 72 · ЖК Buta Zaman · Алматы |
|---|---|---|---|
| РД | 3 | 22 | Планировочное решение<br>26.10.2026 · М 1:30 · А3 |

# План монтажа перегородок

**КВАРТИРА** 72

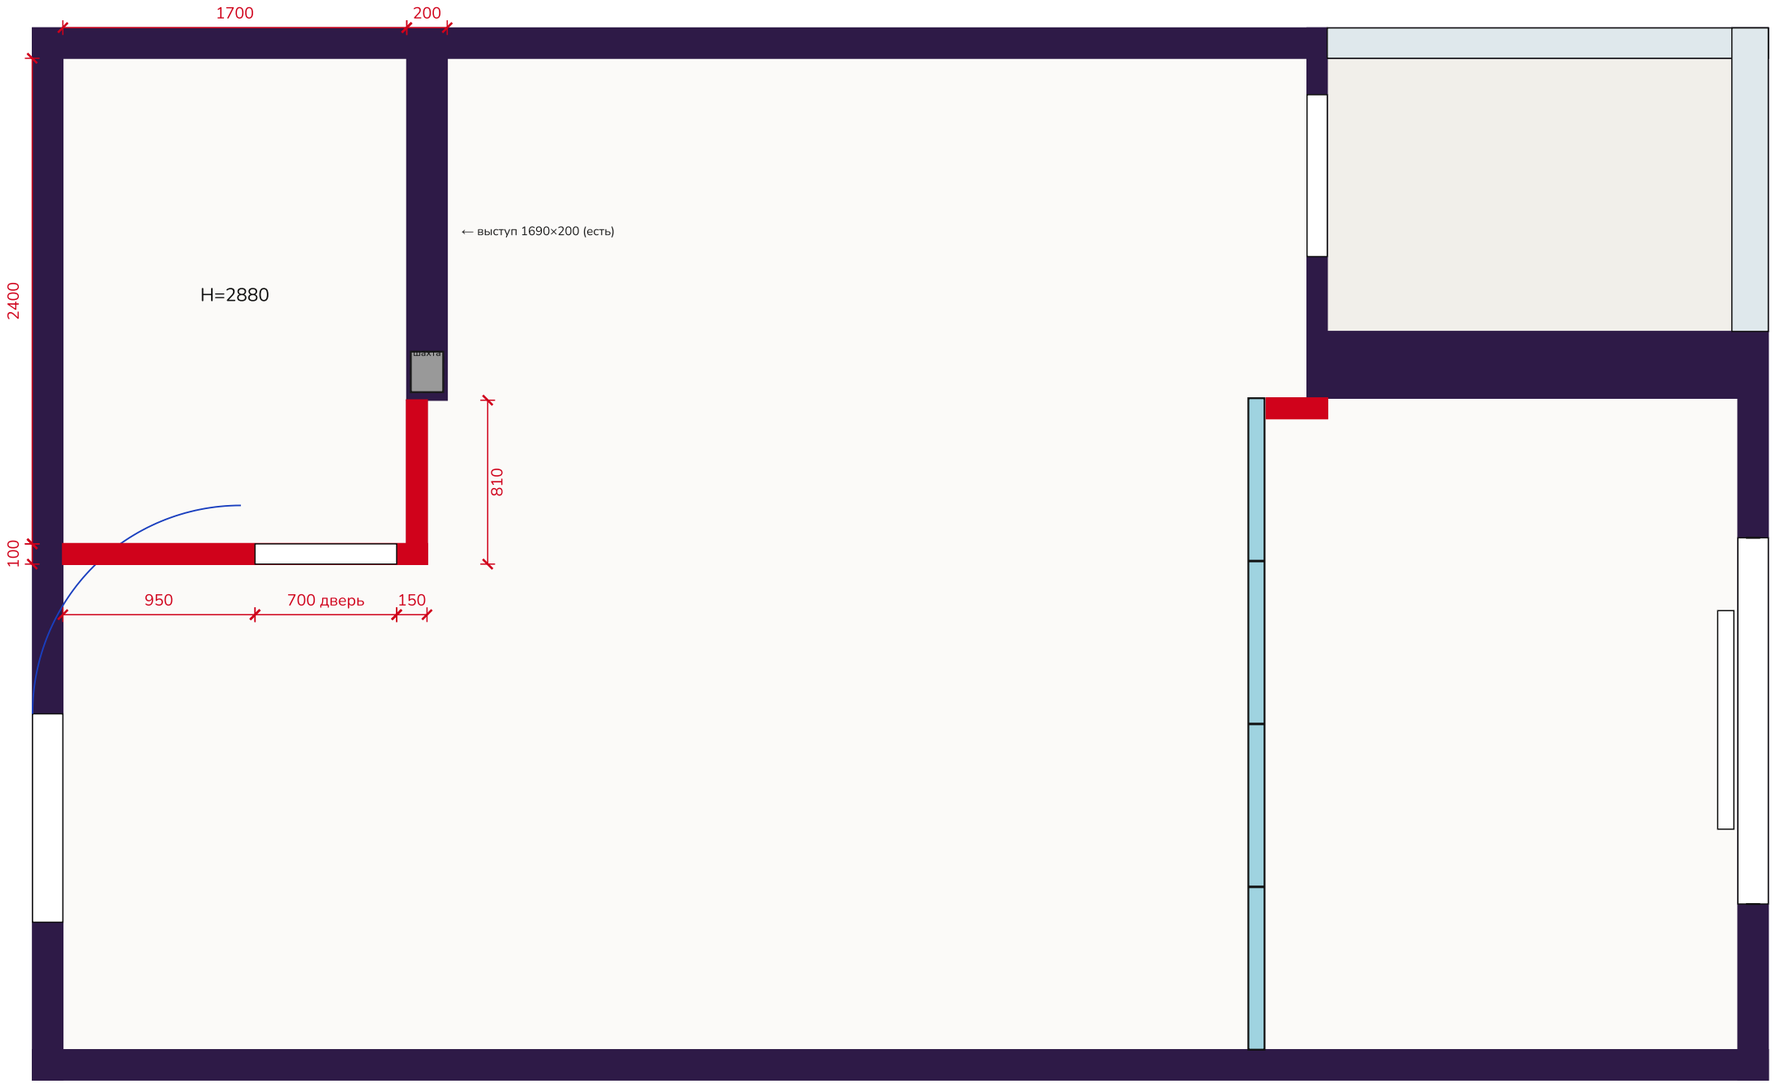


### Условные обозначения

- Существующие стены и выступ
- Возводимые перегородки, газоблок 100 мм
- Стояки / вентшахта в выступе
- Стеклянная раздвижная перегородка (чистовая стадия)

### Спецификация перегородок

| Элемент | Длина | Высота | Площадь |
|---|---|---|---|
| Санузел, стена с дверью | 1 800 | 2 880 | 3,7 м²* |
| Санузел, у выступа | 810 | 2 880 | 2,3 м² |
| Возврат у балкона | 300 | 2 880 | 0,9 м² |
| Газоблок 500×300×100 | | | ~50 шт |

* за вычетом дверных проёмов


**ПРИМЕЧАНИЯ:**

1. За отметку 0.000 принят уровень чистового пола.
2. Все размеры уточнить по месту перед началом работ; привязки даны по неоштукатуренным стенам.
3. Положение короба стояков и вентканала уточнить после приёмки квартиры 10.10.2026.
4. Размеры в миллиметрах, площади в м².
5. Кладка на клей, армирование каждого 3-го ряда, примыкание к монолиту и к выступу через анкеры.
6. Дверные проёмы 700×2100 (санузел) и 800×2100 (спальня), перемычки — уголок или армированный ряд. Санузел 2400×1700 = ниша 1650 + расширение 750.

| Стадия | Лист | Листов | Квартира 72 · ЖК Buta Zaman · Алматы |
|---|---|---|---|
| РД | 4 | 22 | План монтажа перегородок<br>26.10.2026 · М 1:30 · А3 |

# Напольные покрытия

КВАРТИРА 72

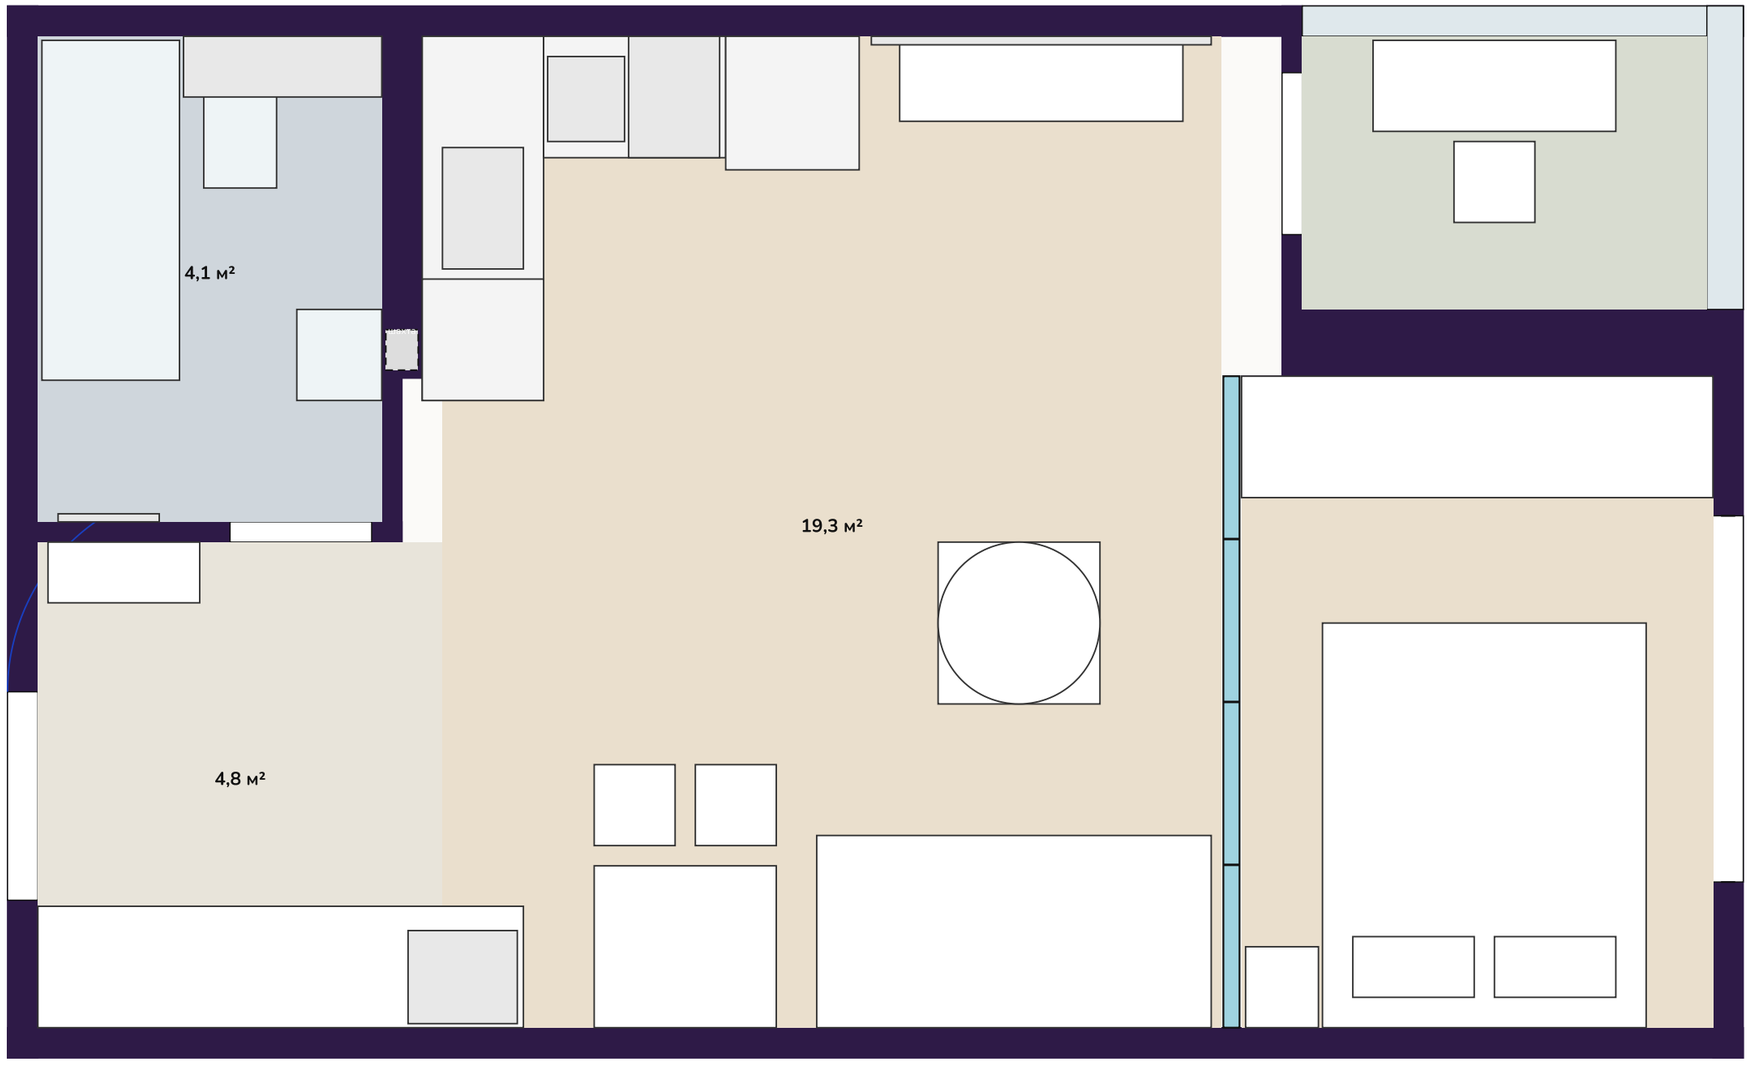


**Спецификация**

| Покрытие | Площадь | С запасом |
|---|---|---|
| Ламинат 33 кл., 8 мм | 26,8 м² | 29,5 м² (+10%) |
| Керамогранит 600×600 (санузел) | 4,1 м² | 4,6 м² (+12%) |
| Керамогранит 200×200 PM213460 (прихожа | 4,8 м² | 5,5 м² (+15%) |
| Лоджия: керамогранит | 2,7 м² | 3,0 м² |
| Подложка 3 мм | 26,8 м² | 29,5 м² |
| Плинтус 60 мм | — | 30 м |
| Порожек плитка/ламинат | — | 1 шт (у санузла и прихожей) |

Количество указано с запасом на подрезку.


**ПРИМЕЧАНИЯ:**

1. За отметку 0.000 принят уровень чистового пола.
2. Все размеры уточнить по месту перед началом работ; привязки даны по неоштукатуренным стенам.
3. Положение короба стояков и вентканала уточнить после приёмки квартиры 10.10.2026.
4. Размеры в миллиметрах, площади в м².
5. Ламинат укладывать вдоль длинной стороны (от входа к окну). Плитка прихожей и санузла на одном уровне с ламинатом через порожек.
6. Под плиткой в прихожей и санузле — электрический тёплый пол (см. план тёплых полов).

| Стадия | Лист | Листов | Квартира 72 · ЖК Buta Zaman · Алматы |
|---|---|---|---|
| РД | 5 | 22 | Напольные покрытия<br>26.10.2026 · М 1:30 · А3 |

# План осветительных приборов

КВАРТИРА 72

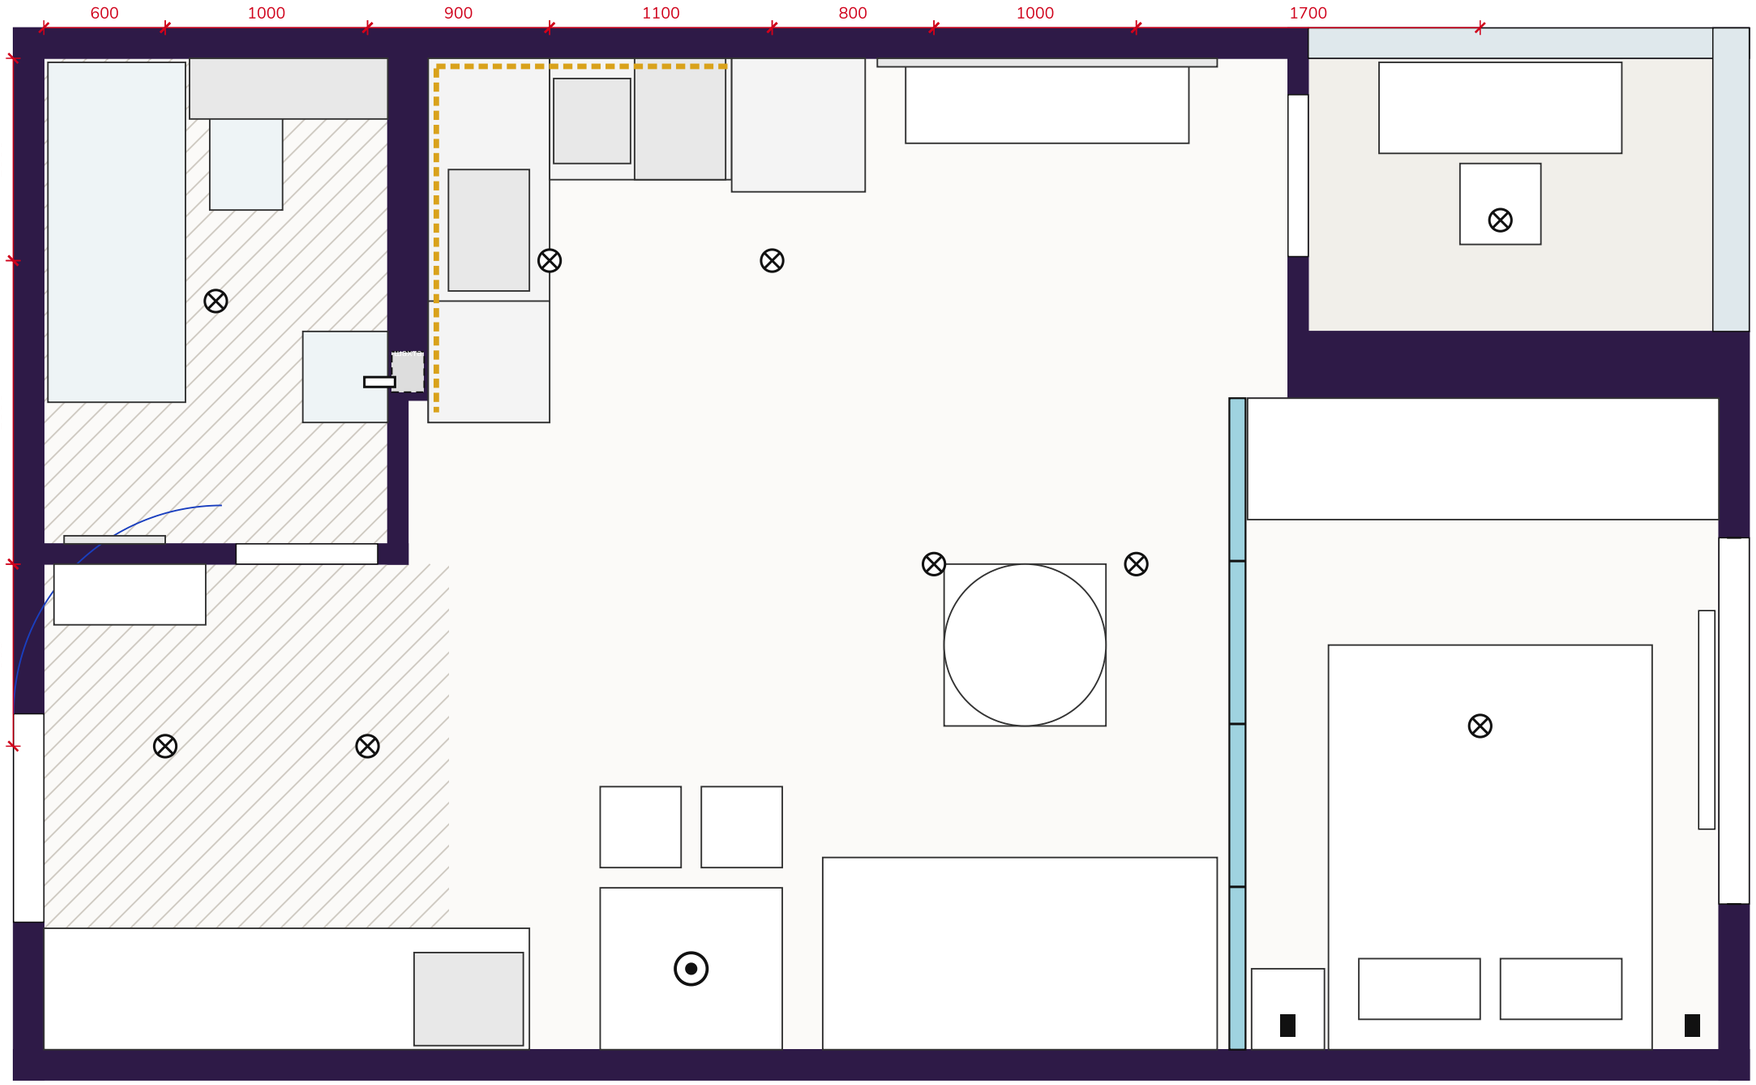


### Условные обозначения

- Спот встраиваемый: двойной (кухня, гостиная, спальня), одинарный
- Подвесной светильник над столом
- Бра, h=1300
- Светодиодная лента (подсветка кухни)
- Зеркало с подсветкой

### Ведомость осветительных приборов

| Наименование | Шт. |
|---|---|
| Спот встраиваемый двойной | 6 |
| Спот встраиваемый одинарный / IP65 в санузле | 3 |
| Подвес над столом | 1 |
| Бра | 2 |
| LED-лента, м | 5 |
| Светящиеся полосы в рейках ТВ-стены | 4 |
| Зеркало с подсветкой | 1 |
| Вентилятор вытяжной | 1 |


**ПРИМЕЧАНИЯ:**

1. За отметку 0.000 принят уровень чистового пола.
2. Все размеры уточнить по месту перед началом работ; привязки даны по неоштукатуренным стенам.
3. Положение короба стояков и вентканала уточнить после приёмки квартиры 10.10.2026.
4. Размеры в миллиметрах, площади в м².
5. Привязки даны к центру светильника.
6. Споты — на отдельных группах: прихожая+санузел, кухня, гостиная, спальня, балкон.

| Стадия | Лист | Листов | Квартира 72 · ЖК Buta Zaman · Алматы |
|---|---|---|---|
| РД | 6 | 22 | План осветительных приборов<br>26.10.2026 · М 1:30 · А3 |

# План розеток

**КВАРТИРА** 72

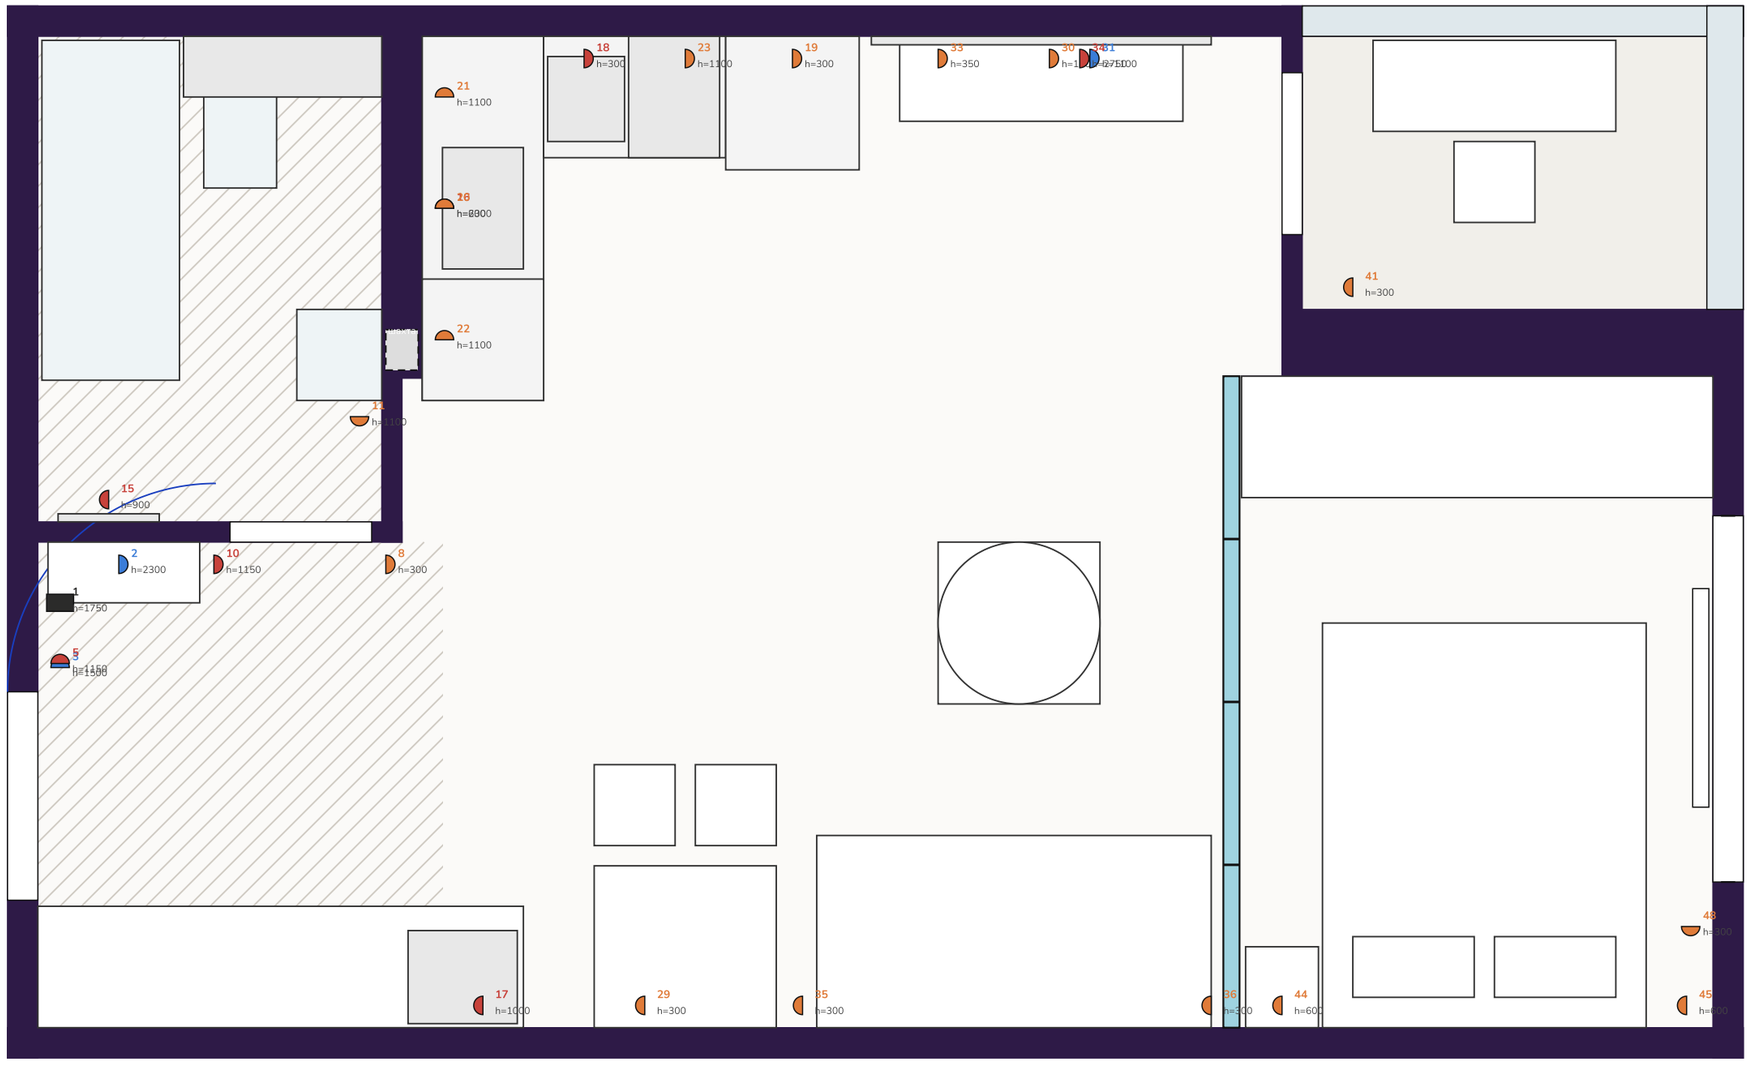


## Условные обозначения

- Розетка (одинарная/двойная), h=300 если не указано
- Вывод для техники / отдельная линия
- Интернет, ТВ, домофон
- Электрощиток h=1750

## Ведомость

| Наименование | Кол-во |
|---|---|
| Розетки, в т.ч. с USB и IP44 | 16 |
| Выводы силовых линий (техника, тёплый пол, полотенцесушитель, кондиционер) | 7 |
| Слаботочные точки | 3 |
| Щиток | 1 |


## ПРИМЕЧАНИЯ:

1. За отметку 0.000 принят уровень чистового пола.
2. Все размеры уточнить по месту перед началом работ; привязки даны по неоштукатуренным стенам.
3. Положение короба стояков и вентканала уточнить после приёмки квартиры 10.10.2026.
4. Размеры в миллиметрах, площади в м².
5. Высоты — до центра розетки от чистого пола. Номера точек — см. таблицу на сайте.
6. Отдельные автоматы: плита 32А, стиральная, посудомоечная, кондиционер, каждый тёплый пол. УЗО на все розеточные группы.

| Стадия | Лист | Листов | Квартира 72 · ЖК Buta Zaman · Алматы |
|---|---|---|---|
| РД | 7 | 22 | План розеток<br>26.10.2026 · М 1:30 · А3 |

# План выключателей

**КВАРТИРА** 72

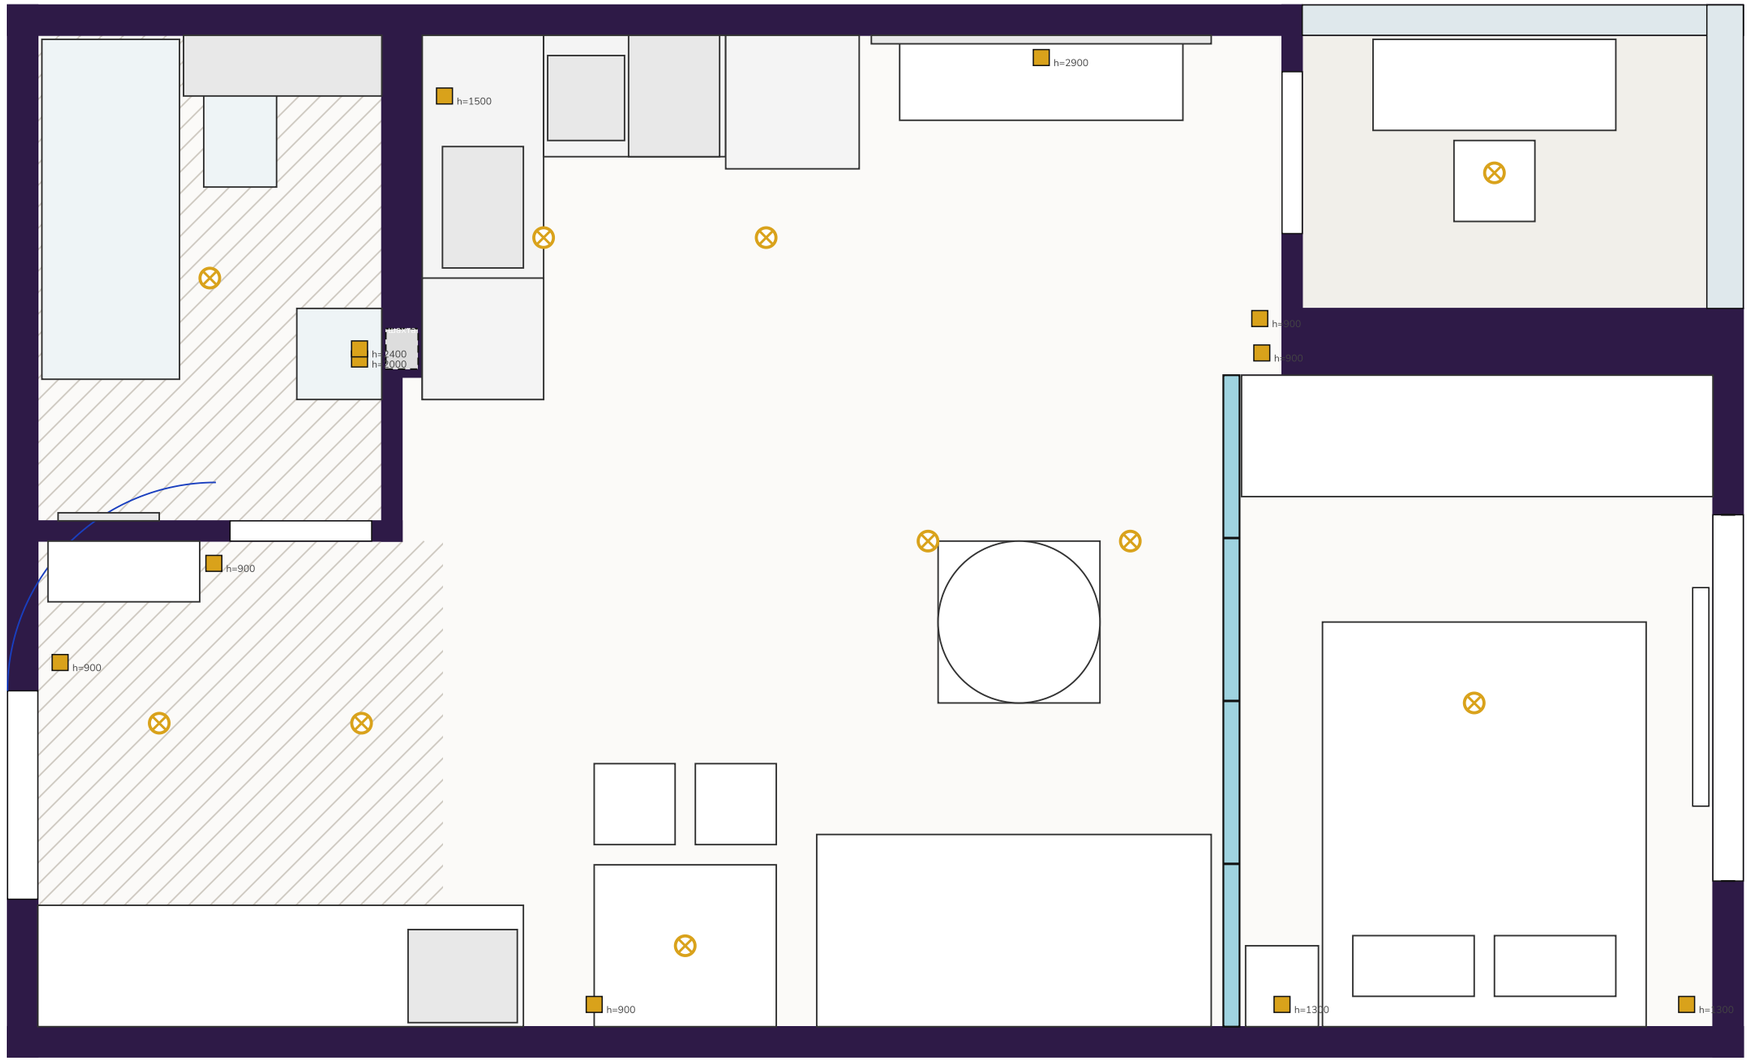


### Условные обозначения

- Выключатель, h=900 (если не указано иное)
- Вывод под светильник на потолке

### Ведомость выключателей и выводов

| Выключатель / вывод | h, мм |
|---|---|
| Выключатель света прихожей | 900 |
| Выключатель санузла + вентилятор | 900 |
| Подсветка зеркала и ниши | 2000 |
| Вытяжной вентилятор (в вентканал выступа) | 2400 |
| Подсветка под верхними шкафами | 1500 |
| Выключатели: кухня, стол, гостиная | 900 |
| Вывод под светящиеся полосы в рейках (4 шт., з | 2900 |
| Выключатель света балкона | 900 |
| Выключатель спальни (у перегородки, со стороны | 900 |
| Бра у кровати | 1300 |
| Бра у кровати | 1300 |


**ПРИМЕЧАНИЯ:**

1. За отметку 0.000 принят уровень чистового пола.
2. Все размеры уточнить по месту перед началом работ; привязки даны по неоштукатуренным стенам.
3. Положение короба стояков и вентканала уточнить после приёмки квартиры 10.10.2026.
4. Размеры в миллиметрах, площади в м².
5. Выключатели у входа в каждую зону со стороны ручки двери. Споты — на отдельных группах: прихожая+санузел, кухня, гостиная, спальня, балкон.

| Стадия | Лист | Листов | Квартира 72 · ЖК Buta Zaman · Алматы |
|---|---|---|---|
| РД | 8 | 22 | План выключателей<br>26.10.2026 · М 1:30 · А3 |

# План потолка

КВАРТИРА 72

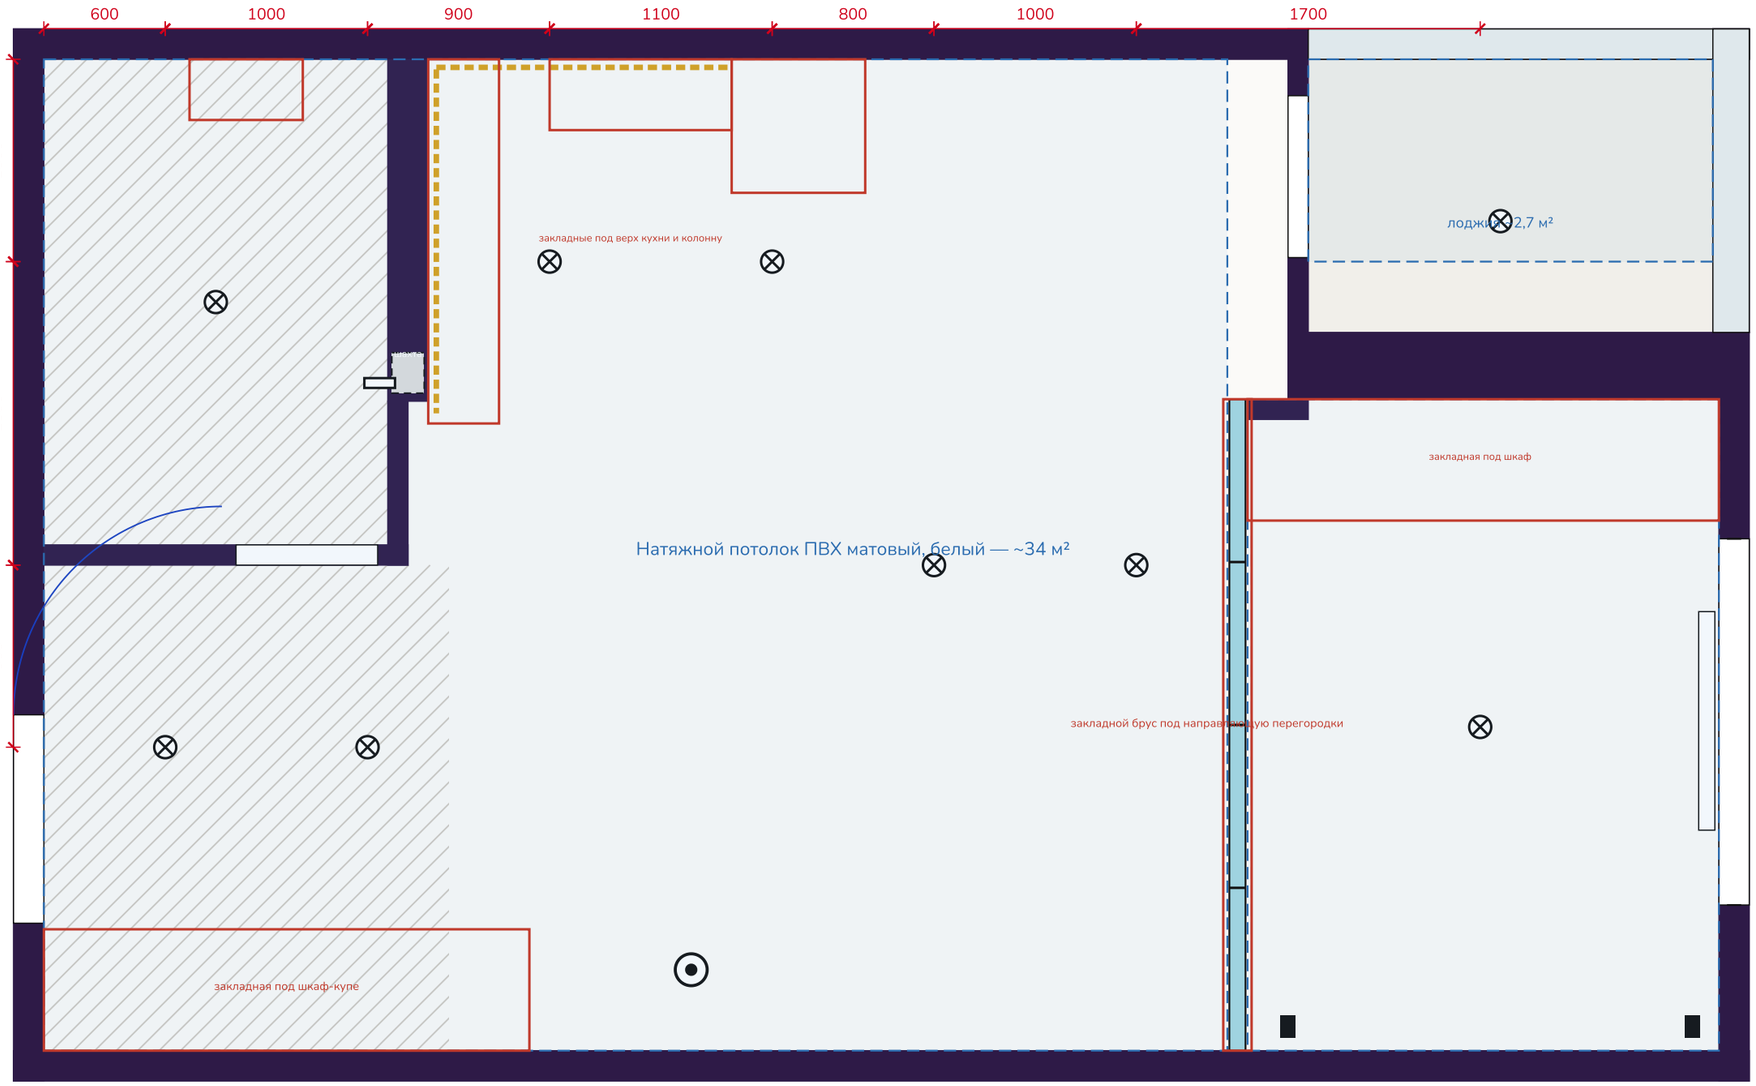


**Условные обозначения**

- ⊗ Спот встраиваемый, 9 точек
- Граница натяжного потолка
- Закладные (брус) до монтажа потолка

Потолок 2880; под встраиваемые споты полотно ниже на 80–100 мм: ~2790 мм

Перегородка и шкаф-купе крепятся к закладным, не к полотну.


**ПРИМЕЧАНИЯ:**

1. За отметку 0.000 принят уровень чистового пола.
2. Все размеры уточнить по месту перед началом работ; привязки даны по неоштукатуренным стенам.
3. Положение короба стояков и вентканала уточнить после приёмки квартиры 10.10.2026.
4. Размеры в миллиметрах, площади в м².
5. Монтаж потолка — после покраски стен и до ламината; трасса кондиционера и кабели спотов — до потолка.
6. Все шкафы до потолка без зазора: закладной брус по линии фасада до натяжного потолка; корпус на 30–50 мм ниже, сверху доборная планка в цвет фасада, подрезка по месту. Замер шкафов — после монтажа потолка.

| Стадия | Лист | Листов | Квартира 72 · ЖК Buta Zaman · Алматы |
|---|---|---|---|
| РД | 9 | 22 | План потолка<br>26.10.2026 · М 1:30 · А3 |

# План сантехнического оборудования

**КВАРТИРА** 72

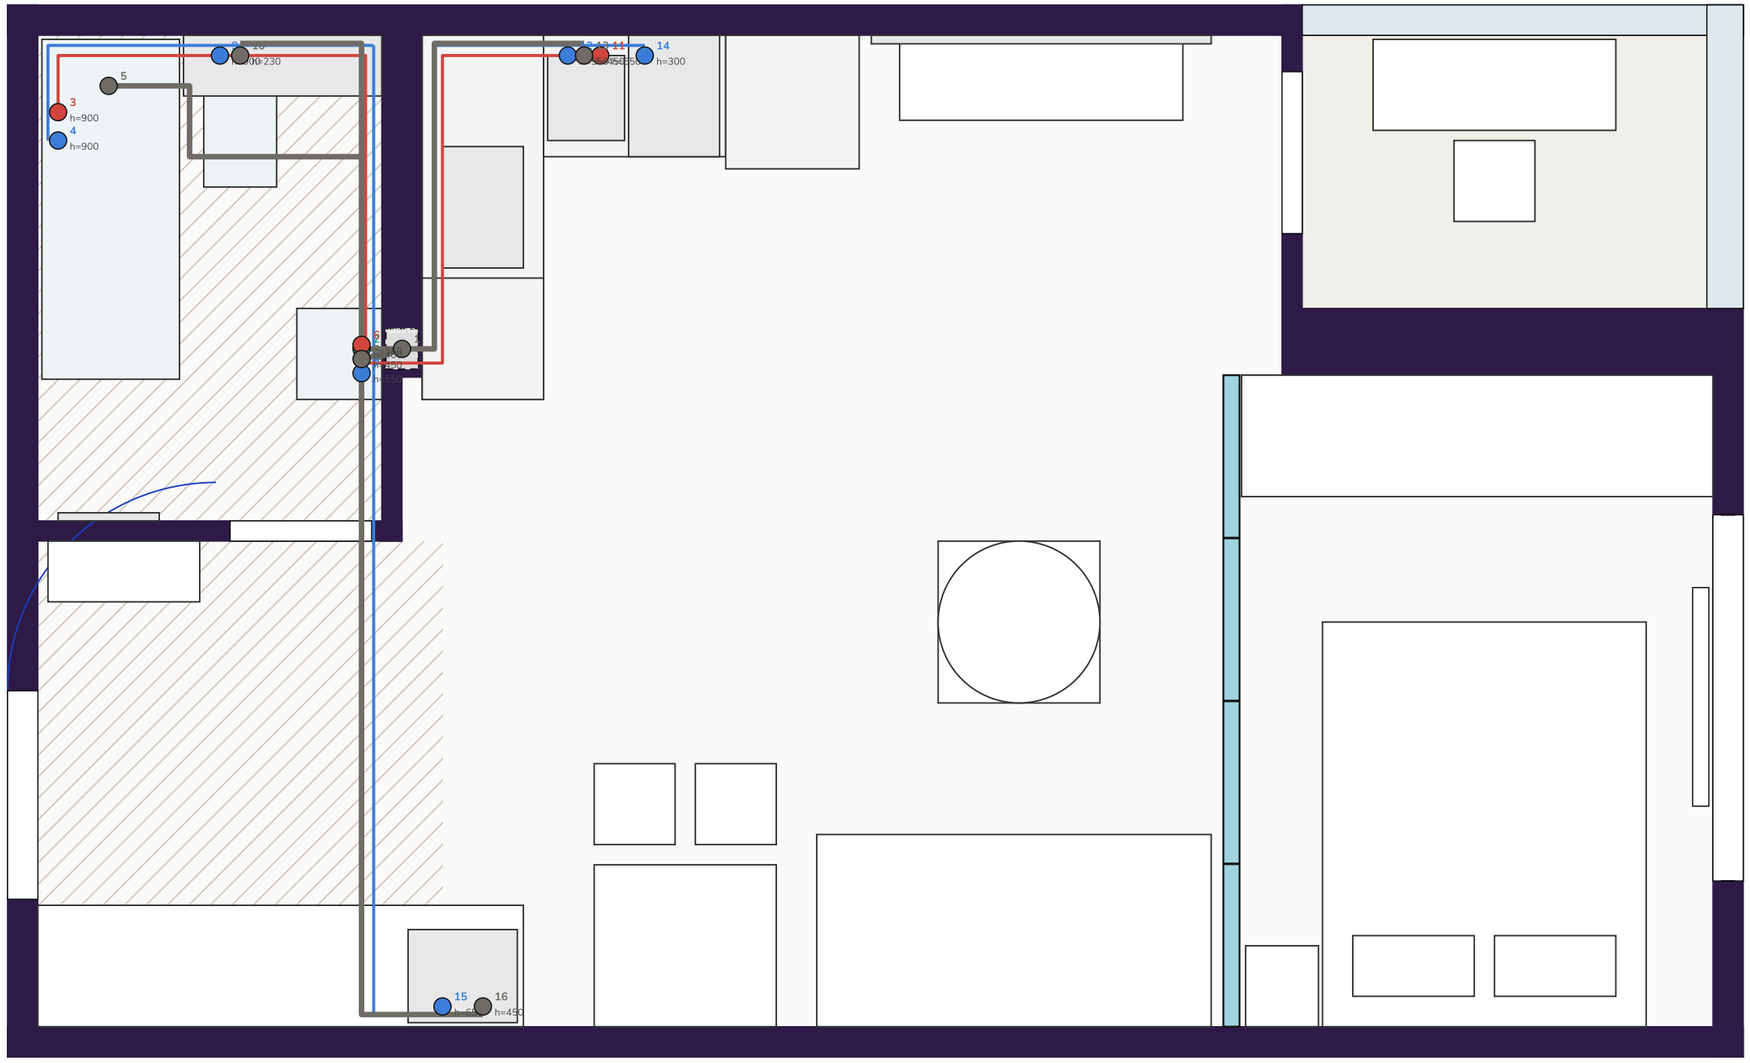


### Условные обозначения

- Холодная вода
- Горячая вода
- Канализация Ø50 / Ø110
- Краны, фильтры, счётчики
- Точка вывода (номер — см. таблицу)

### Ведомость точек

| № | Точка | h, мм |
|---|---|---|
| 1 | Стояки и вентканалы — внутри выступа 169×20 (шах | — |
| 2 | Краны, счётчики, фильтры (люк в выступе, внутри | 400 |
| 3 | Ванна: смеситель с тропическим душем, горячая | 900 |
| 4 | Ванна: смеситель с тропическим душем, холодная | 900 |
| 5 | Ванна: слив Ø50 у торца | в полу |
| 6 | Раковина: горячая | 550 |
| 7 | Раковина: холодная | 550 |
| 8 | Раковина: слив Ø50 | 450 |
| 9 | Унитаз: вода в инсталляцию | 900 |
| 10 | Унитаз: канализация Ø110 | 230 |
| 11 | Мойка: горячая | 550 |
| 12 | Мойка: холодная | 550 |
| 13 | Мойка: слив Ø50 | 450 |
| 14 | Посудомойка: кран на холодной, слив в сифон моек | 300 |
| 15 | Стиральная машина в шкафу-купе: кран холодной во | 650 |
| 16 | Стиральная машина: слив Ø50 с сифоном, труба в с | 450 |


**ПРИМЕЧАНИЯ:**

1. За отметку 0.000 принят уровень чистового пола.
2. Все размеры уточнить по месту перед началом работ; привязки даны по неоштукатуренным стенам.
3. Положение короба стояков и вентканала уточнить после приёмки квартиры 10.10.2026.
4. Размеры в миллиметрах, площади в м².
5. Горячая — слева, холодная — справа. Уклон канализации 2–3 см/м к стояку.
6. Опрессовка труб до штукатурки. Стиральная и посудомоечная — через краны и сифоны с обратным клапаном.
7. Стиральная машина — в шкафу-купе прихожей: вода и слив Ø50 из санузла через стену в стяжке прихожей (~4 м, уклон ≥1%); толщину стяжки согласовать с сантехником до заливки.
8. Ванна 1700×700 (при тесном стояке — 1500–1600). Унитаз подвесной на инсталляции.

| Стадия | Лист | Листов | Квартира 72 · ЖК Buta Zaman · Алматы |
|---|---|---|---|
| РД | 10 | 22 | План сантехнического оборудования<br>26.10.2026 · М 1:30 · А3 |

# План радиаторов и тёплых полов

КВАРТИРА 72

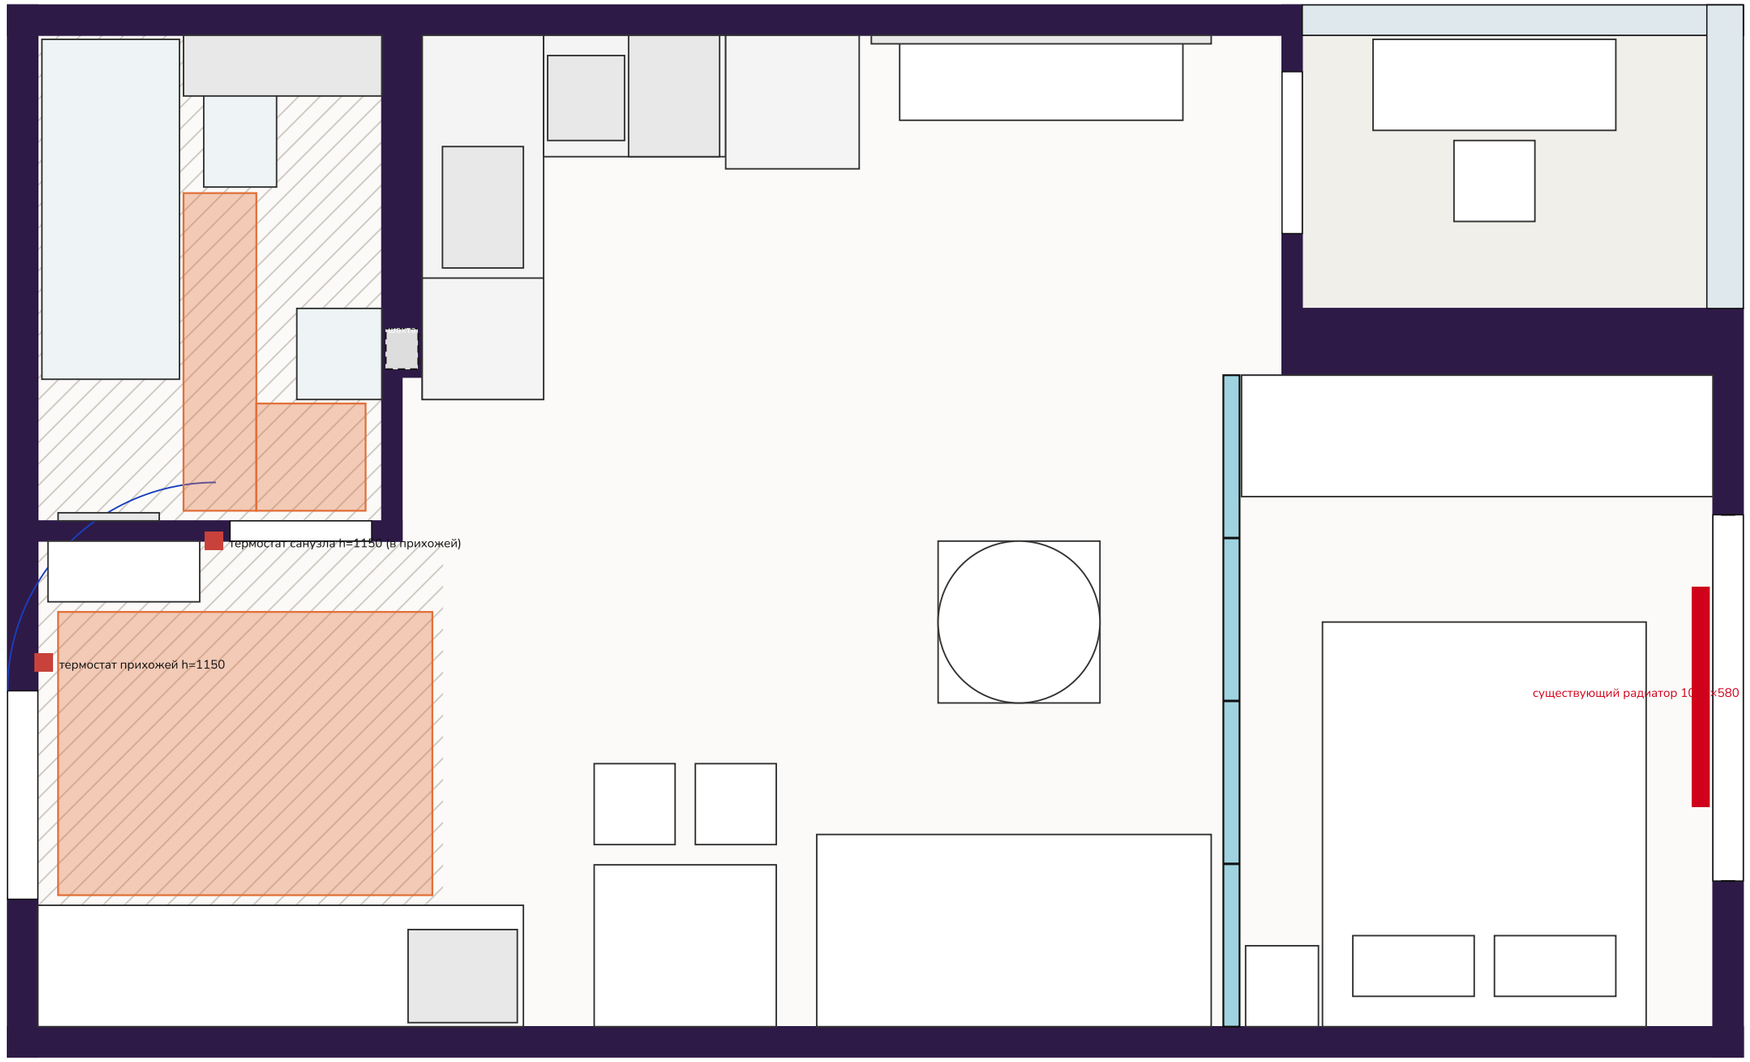


### Условные обозначения

- Радиатор отопления (существующий)
- Электрический тёплый пол, мат 150 Вт/м²
- Термостат с датчиком пола

### Ведомость

| Элемент | Кол-во |
|---|---|
| Радиатор под окном 1080×580 | 1 шт |
| Тёплый пол прихожая | 2,6 м² |
| Тёплый пол санузел | 1,6 м² |
| Термостаты | 2 шт |
| Полотенцесушитель электрический | 1 шт |


**ПРИМЕЧАНИЯ:**

1. За отметку 0.000 принят уровень чистового пола.
2. Все размеры уточнить по месту перед началом работ; привязки даны по неоштукатуренным стенам.
3. Положение короба стояков и вентканала уточнить после приёмки квартиры 10.10.2026.
4. Размеры в миллиметрах, площади в м².
5. Радиатор не переносится; подоконник-полка над ним — с зазором для конвекции не менее 30 мм.
6. Мат под плитку в слой клея, датчик в гофре между витками, включение через 28 дней.


| Стадия | Лист | Листов | Квартира 72 · ЖК Buta Zaman · Алматы |
|---|---|---|---|
| РД | 11 | 22 | План радиаторов и тёплых полов<br>26.10.2026 · М 1:30 · А3 |


# Развёртка стен: кухня

**A — выступ санузла (z=1900)**

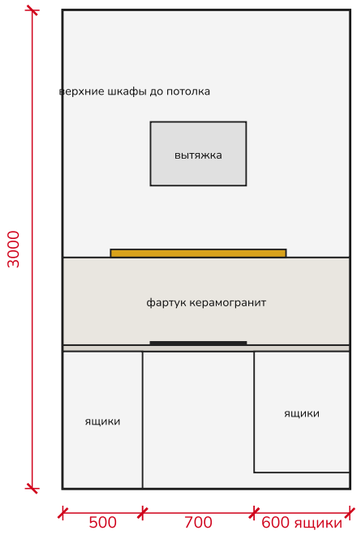


**B — левая стена (x=0)**

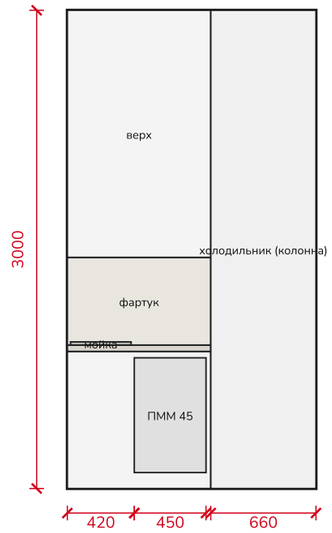

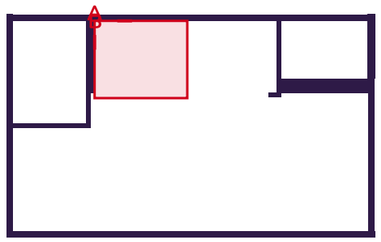ключ-план

Стена под краску

**8,5 м²**

стены кухни над фартуком и свободные участки

Отметки: столешница 900 · фартук 900–1450 · верхние шкафы 1450 — потолок (~2790) · розетки над столешницей h=1100 · LED под верхними шкафами · вытяжка h=1900–2250

Фасады белые матовые без ручек, столешница 38 мм светлый камень, фартук керамогранит 600×1200. Длина кухни 1,8 + 0,9 + колонна 0,66 м.


**ПРИМЕЧАНИЯ:**


1. За отметку 0.000 принят уровень чистового пола.
2. Все размеры уточнить по месту перед началом работ; привязки даны по неоштукатуренным стенам.
3. Положение короба стояков и вентканала уточнить после приёмки квартиры 10.10.2026.
4. Размеры в миллиметрах, площади в м².
5. Замер кухни — после штукатурки, установка — после пола и потолка.

| Стадия | Лист | Листов | Квартира 72 · ЖК Buta Zaman · Алматы |
|---|---|---|---|
| РД | 12 | 22 | Развёртка стен: кухня<br>26.10.2026 · М 1:38 · А3 |

КВАРТИРА 72

# Развёртка стен: санузел

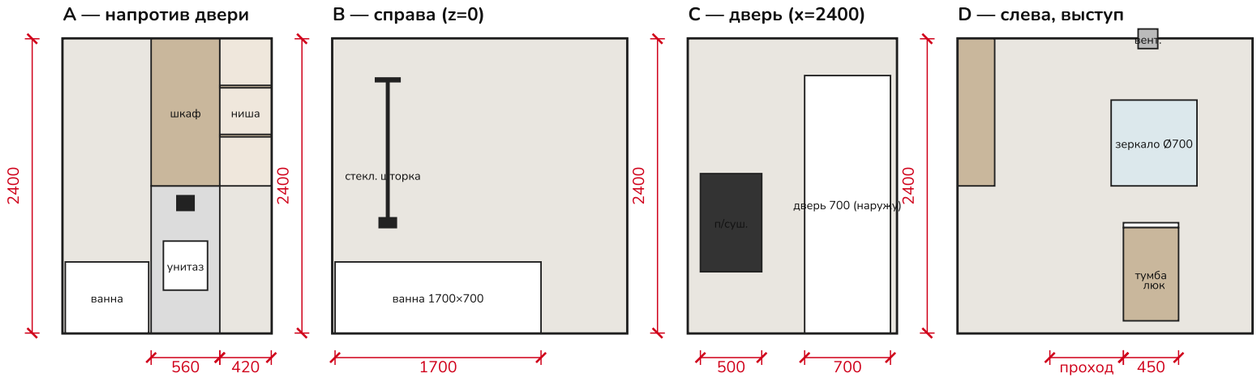

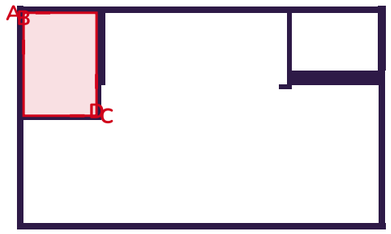
ключ-план

Санузел 2400 × 1700 = ниша 1650 + расширение 750 в прихожую; h ~2400 (натяжной потолок). Керамогранит 600×600 стены и пол, швы 2 мм. Стены ~18 м², пол 4,1 м².

От двери: напротив — подвесной унитаз, над ним шкаф до потолка и ниша с полками; справа — ванна 1700 со шторкой и тропическим душем; слева — узкая тумба 450×420 с раковиной у двери, над ней зеркало.

Отметки: смеситель 900 · душ 2100 · инсталляция 1200, шкаф над ней до потолка · столешница 900 · зеркало Ø700 h 1200–1900 · розетки IP44 h=1100. Дверь открывается наружу, п/сушитель у двери.

Перед унитазом свободно, проход вдоль ванны не меньше 580. Стиральная машина — в шкафу-купе прихожей (вода и слив из санузла в стяжке).

Стена под краску

**0 м²**

все стены — керамогранит 600×600, ~18 м²


**ПРИМЕЧАНИЯ:**

1. За отметку 0.000 принят уровень чистового пола.
2. Все размеры уточнить по месту перед началом работ; привязки даны по неоштукатуренным стенам.
3. Положение короба стояков и вентканала уточнить после приёмки квартиры 10.10.2026.
4. Размеры в миллиметрах, площади в м².
5. Стояки и вентканалы — внутри выступа 169×20. Ревизионный люк — в выступе внутри тумбы под раковиной. Унитаз — на дальней стене, ось унитаза в 300 мм от края ванны, слив Ø110 ~1,6 м к шахте.


| Стадия | Лист | Листов | Квартира 72 · ЖК Buta Zaman · Алматы |
|---|---|---|---|
| РД | 13 | 22 | Развёртка стен: санузел<br>26.10.2026 · М 1:50 · А3 |

# Развёртка стен: прихожая


**A — правая стена (x=4900): шкаф-купе**

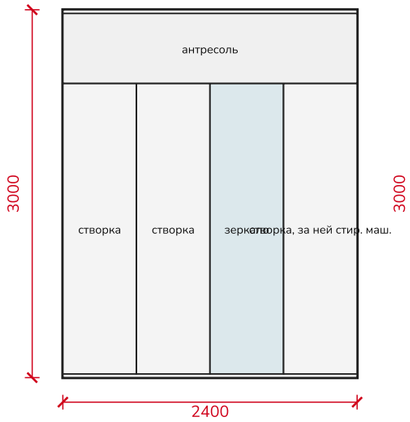



**B — стена санузла (x=2500)**

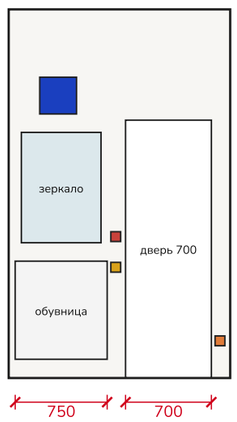


**C — входная стена (z=0)**

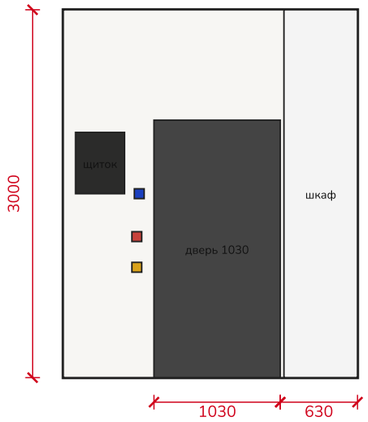

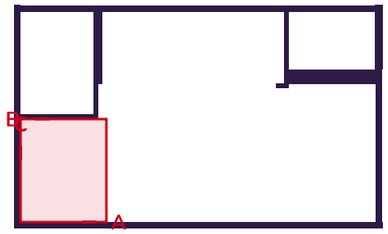
ключ-план

Стена под краску

**7,0 м²**

стены прихожей без шкафа и дверей

Шкаф-купе 2400×600 до потолка: 4 створки по 600, одна — зеркало, антресоль от 2400; в секции у гостиной — узкая стиральная машина глубиной 40 см (без дна, вода и слив из санузла в стяжке, розетка с УЗО); фасад вровень с откосом входной двери (630 от угла).

Обувница подвесная 750×300, h 150–950, зеркало над ней. Щиток h=1750 слева от входной двери, домофон h=1500 у двери, слаботочный щиток h=2300 над зеркалом.

**ПРИМЕЧАНИЯ:**


1. За отметку 0.000 принят уровень чистового пола.
2. Все размеры уточнить по месту перед началом работ; привязки даны по неоштукатуренным стенам.
3. Положение короба стояков и вентканала уточнить после приёмки квартиры 10.10.2026.
4. Размеры в миллиметрах, площади в м².
5. Пол прихожей — керамогранит Medici PM213460 200×200 (молочный с чёрным рисунком) с тёплым полом; раскладку начинать от шкафа-купе целой плиткой, подрезка — к санузлу; порожек на границе с ламинатом.

| Стадия | Лист | Листов | Квартира 72 · ЖК Buta Zaman · Алматы |
|---|---|---|---|
| РД | 14 | 22 | Развёртка стен: прихожая<br>26.10.2026 · М 1:50 · А3 |


КВАРТИРА 72

# Развёртка стен: гостиная


**A — левая стена (x=0): ТВ-зона**

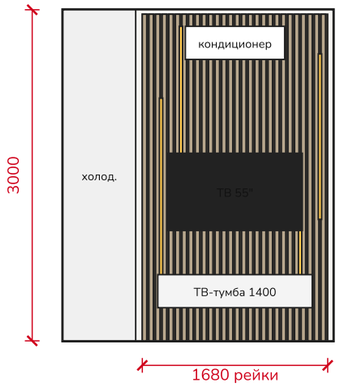



**B — правая стена (x=4900)**

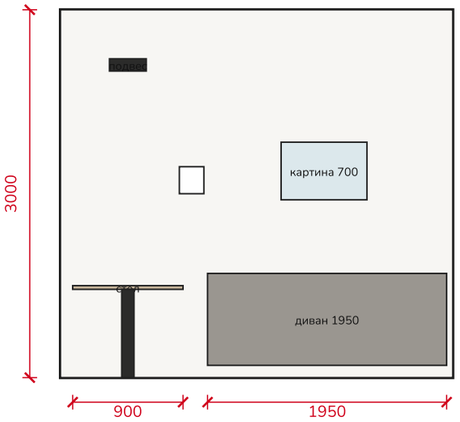


**C — стеклянная перегородка (z=5850)**

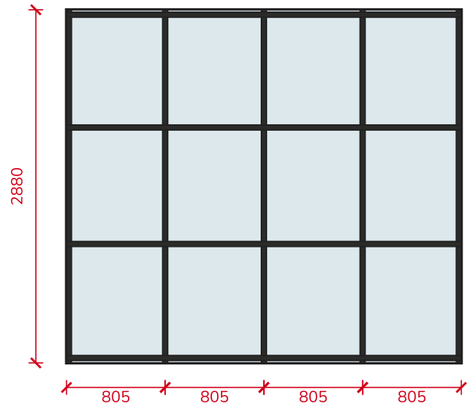

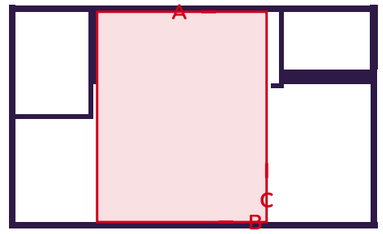
ключ-план

Стена под краску

**20,5 м²**

стены гостиной и кухонной зоны

ТВ-стена 1680×2960 (от холодильника до стены спальни): рейки 40 мм с шагом 60 мм на тёмной подложке, 4 светящиеся полосы 3000K между рейками, вывод кабеля h=2900 за рейками.

Тумба 1400, ТВ 55", кондиционер крепить сквозь рейки в стену; розетки ×2 + интернет/ТВ h=1100, розетка у тумбы h=350.

Перегородка спальни (z=5850): 4 стеклянные створки ~805 мм в чёрном профиле с переплётом, до потолка; створки уезжают к правой стене; тюль со стороны спальни.


**ПРИМЕЧАНИЯ:**

1. За отметку 0.000 принят уровень чистового пола.
2. Все размеры уточнить по месту перед началом работ; привязки даны по неоштукатуренным стенам.
3. Положение короба стояков и вентканала уточнить после приёмки квартиры 10.10.2026.
4. Размеры в миллиметрах, площади в м².


| Стадия | Лист | Листов | Квартира 72 · ЖК Buta Zaman · Алматы |
|---|---|---|---|
| РД | 15 | 22 | Развёртка стен: гостиная<br>26.10.2026 · M 1:50 · A3 |

# Развёртка стен: спальня


**A — стена с окном (z=8280)**

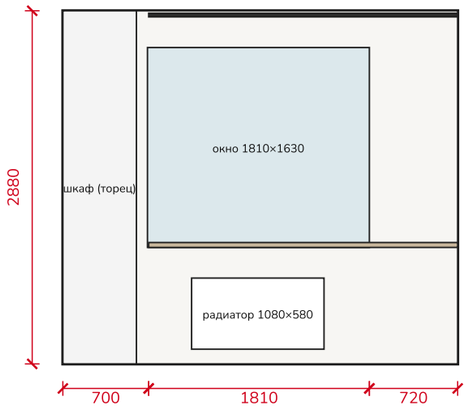



**B — правая стена (x=4900)**

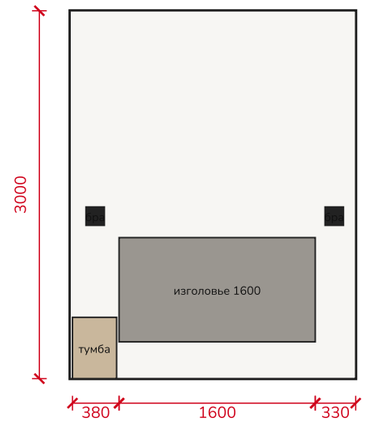


**C — шкаф у левой стены (x=1680)**

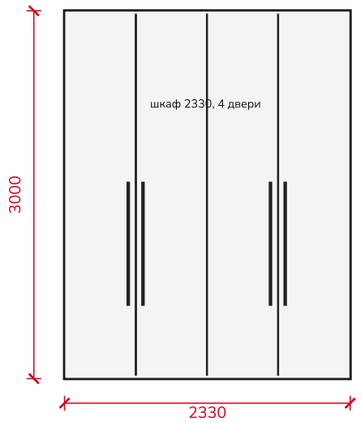

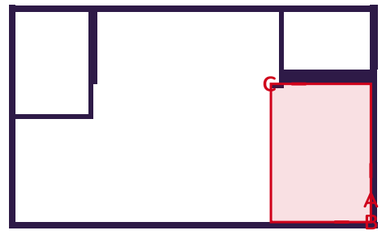
ключ-план

Стена под краску

**12,5 м²**

стены спальни без шкафа и окна

Шкаф 2330×600 до потолка вдоль левой стены, 4 распашные двери с ручками-профилями; проход до кровати ~620. Окно: низ 950, верх 2580.

Скрытый карниз в нише натяжного потолка. Подоконник-полка 300 мм на h=950, радиатор 1080×580 под ним. Изголовье 1600×850, бра h=1300, розетки USB h=600.

Вход — через стеклянную раздвижную перегородку; выключатель спальни — со стороны гостиной у перегородки.


**ПРИМЕЧАНИЯ:**

1. За отметку 0.000 принят уровень чистового пола.
2. Все размеры уточнить по месту перед началом работ; привязки даны по неоштукатуренным стенам.
3. Положение короба стояков и вентканала уточнить после приёмки квартиры 10.10.2026.
4. Размеры в миллиметрах, площади в м².

| Стадия | Лист | Листов | Квартира 72 · ЖК Buta Zaman · Алматы |
|---|---|---|---|
| РД | 16 | 22 | Развёртка стен: спальня<br>26.10.2026 · M 1:50 · A3 |

# Мебель: схема

КВАРТИРА 72

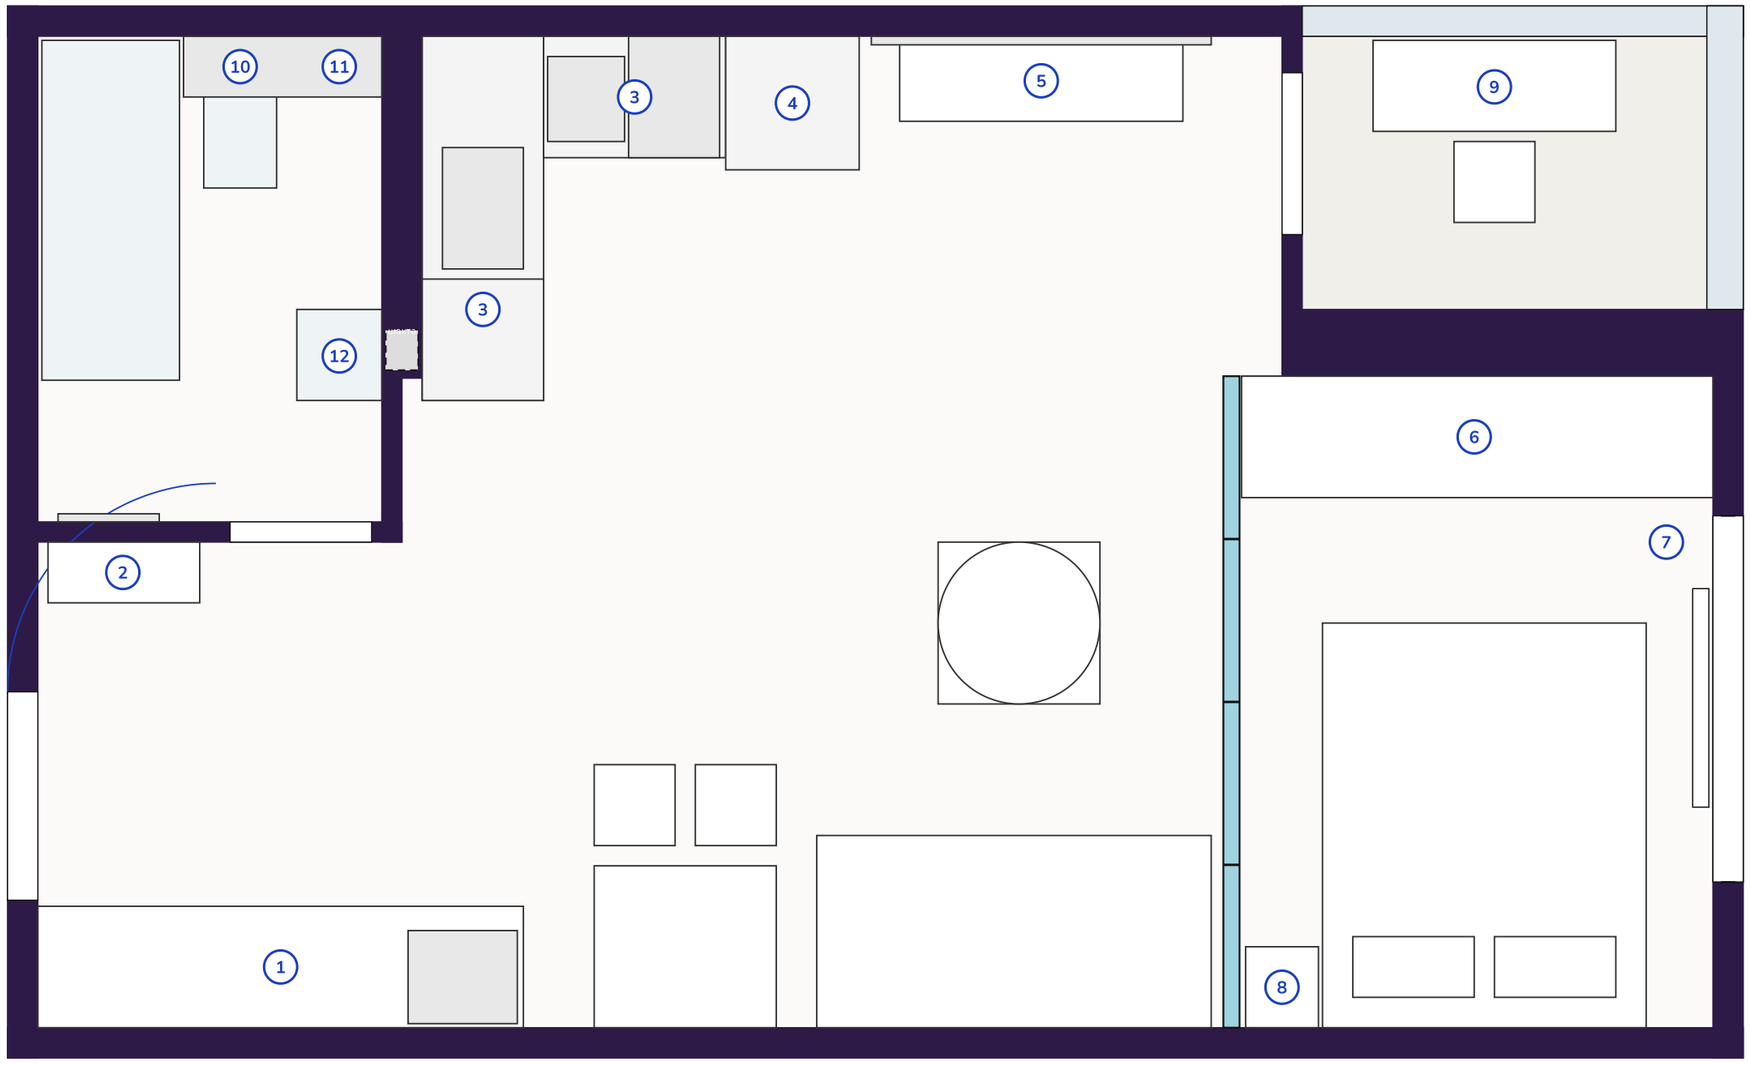


**Изделия по схеме**

| № | Изделие |
|---|---|
| 1 | Шкаф-купе, прихожая |
| 2 | Обувница подвесная и зеркало |
| 3 | Кухня: низ, столешница, верх |
| 4 | Колонна под холодильник |
| 5 | ТВ-тумба подвесная |
| 6 | Шкаф распашной, спальня |
| 7 | Подоконник-полка, спальня |
| 8 | Тумба у кровати |
| 9 | Стол и 2 полки, лоджия |
| 10 | Шкаф над инсталляцией, санузел |
| 11 | Ниша с полками, санузел |
| 12 | Тумба с раковиной, санузел |

Размеры — на следующем листе.

**ПРИМЕЧАНИЯ:**

1. За отметку 0.000 принят уровень чистового пола.
2. Все размеры уточнить по месту перед началом работ; привязки даны по неоштукатуренным стенам.
3. Положение короба стояков и вентканала уточнить после приёмки квартиры 10.10.2026.
4. Размеры в миллиметрах, площади в м².
5. Схема показывает расположение. Точные размеры мебельщик снимает на замере после чистовых стен, пола и натяжного потолка.

| Стадия | Лист | Листов | Квартира 72 · ЖК Buta Zaman · Алматы |
|---|---|---|---|
| РД | 17 | 22 | Мебель: схема<br>26.10.2026 · М 1:30 · А3 |

# Мебель: размеры для мебельщика

**Встроенная и заказная мебель**

| № | Изделие | Ш × Г × В, мм | Исполнение и привязки |
|---|---|---|---|
| 1 | Шкаф-купе, прихожая | 2400 × 600 × до потолка | Глухой от пола, 4 раздвижные створки ~600, третья от входа — зеркало, антресоль от h 2400. Фасад на x=4270, фальш-планка до потолка. |
| 1а | Секция под стиральную машину | в свету ≥ 620 × см. прим. 3 | Крайняя секция со стороны гостиной, без дна. Вода h 650, слив h 450, розетка h 1000 на стене за машиной. Полки выше h 900. |
| 2 | Обувница подвесная | 750 × 300 × 800 | Низ h 150, верх h 950, стена санузла, от входной стены 50. Над ней зеркало 650 × 1000, h 1100–2100 (толщина 30). |
| 3а | Кухня, низ, стена выступа | 1800 × 600 × 860 | От левой стены: угол, шкаф под варочную 700, ящики 600. Цоколь 100. Точная разбивка — по проекту мебельщика и размерам техники. |
| 3б | Кухня, низ, левая стена | 900 × 600 × 860 | От угла: шкаф под мойку 420, посудомойка встроенная 450, добор. Цоколь 100. Вода и слив на левой стене, h 450–550. |
| 3в | Столешница | Г-образная 1820 + 900 × 620 | Толщина 38, верх h 900, светлая под камень. Вырезы: варочная 600, мойка ~380 × 420. Фартук 900–1450 (керамогранит, в смету мебели не входит). |
| 3г | Кухня, верх, стена выступа | 1800 × 350 × 1340 | h 1450 — потолок, 3 фасада ~550/600/650, встраиваемая вытяжка 600 (розетка h 2300 в шкафу), LED снизу. Белый мат без ручек. |
| 3д | Кухня, верх, левая стена | 900 × 350 × 1340 | h 1450 — потолок, 2 фасада по 450. Белый мат без ручек, LED снизу. |
| 4 | Колонна под холодильник | 660 × 660 × до потолка | Два фасада, раздел на h 1000. Ширину и вентиляцию проверить по паспорту холодильника. |
| 5 | ТВ-тумба подвесная | 1400 × 380 × 300 | Низ h 300, верх h 600, крепление через реечную стену в основание (рейки 30 мм + подложка 12 мм). Закладные в стену — до реек. |
| 6 | Шкаф распашной, спальня | 2330 × 600 × до потолка | Вдоль левой стены, от перегородки до стены с окном. 4 двери ~580, ручки-профили 1000, цоколь 80. Двери открываются в спальню, до кровати 620. |
| 7 | Подоконник-полка, спальня | 2520 × 300 × 40 | h 950–990, от x=2380 до правой стены, под окном, дуб. Радиатор снизу: оставить зазор для тёплого воздуха. |
| 8 | Тумба у кровати | 400 × 360 × 500 | У правой стены, рядом с перегородкой, дуб. |
| 9 | Стол и 2 полки, лоджия | стол 1200 × 450, h 750 | Вдоль левого остекления, ножки металл. Полки 1200 × 250 × 30 на h 1300 и 1750, крепить к стене-простенку уточнить по месту. |
| 10 | Шкаф над инсталляцией, санузел | 560 × 300 × 1200 | h 1200 — потолок санузла 2400. 2 фасада, влагостойкий, под дуб. Сверху упор в полотно, планка 30–50 мм. |
| 11 | Ниша с полками, санузел | 420 × 250 × 1200 | h 1200–2400 рядом со шкафом, 2 полки 20 мм на h 1600 и 2000, LED сверху. |
| 12 | Тумба с раковиной, санузел | 450 × 420 × 860 | У двери, вдоль выступа-шахты. Столешница/раковина 40, верх h 900, ножки 100. Задняя стенка съёмная: внутри ревизионный люк шахты и краны. |

| Покупная мебель (для проверки места) | Размер, мм |
|---|---|
| Обеденный стол | 900 × 800, h 750 |
| Диван | 1950 × 950 |
| Кровать | 1600 × 2000 |
| Журнальный столик | Ø 800 |
| Ванна | 1700 × 700 |

**ПРИМЕЧАНИЯ:**

1. Высота: черновой потолок 2880, натяжной ~2790 (санузел 2400). Все шкафы до потолка без зазора: корпус на 30–50 мм ниже, сверху доборная планка в цвет фасада, подрезка по месту.
2. Закладной брус под линией фасадов ставят до натяжного потолка (лист «План потолка»). Замер мебели — только после монтажа потолка и чистовых стен и пола.
3. Стиральная машина: шир. ~600, выс. 850. Купе-рельсы занимают ~100 мм, в свету остаётся ~490: машина 400 + шланги ~80 входит, машина 450 — нет. Для неё корпус глубже (650) или распашная дверь.
4. Спальня: у перегородки выступает стена 100 × 300 (x 1680–1780, z 5950–6250). Корпус шкафа 6 в этом месте подрезать на замере, фасады оставить в одну линию.
5. Материал: ЛДСП белая, фасады МДФ белый мат; санузел — влагостойкие материалы. Кромка ПВХ, петли и направляющие с доводчиком.
6. Размеры — проектные. Окончательные снимает мебельщик по месту и согласует с заказчиком.

# Визуализация 1



Общий вид



Гостиная, вид на спальню и ТВ-стену



Кухня



Кухня крупно

| Стадия | Лист | Листов | Квартира 72 · ЖК Buta Zaman · Алматы |
|---|---|---|---|
| РД | 19 | 22 | Визуализация 1<br>26.10.2026 · M — · A3 |

# Визуализация 2



Спальня: шкаф до потолка, окно, стеклянная перегородка



Прихожая: плитка PM213460, шкаф-купе



Санузел: вид от двери



Санузел: вид на дверь и тумбу с раковиной

| Стадия | Лист | Листов | Квартира 72 · ЖК Buta Zaman · Алматы |
|---|---|---|---|
| РД | 20 | 22 | Визуализация 2<br>26.10.2026 · M — · A3 |

# Ведомость материалов

### Отделка помещений

| № | Помещение | Пол | Стены | Потолок | Площадь |
|---|---|---|---|---|---|
| 1 | Прихожая | Керамогранит 600×600 + тёплый пол | Краска | Натяжной | ~4,8 м² |
| 2 | Санузел | Керамогранит 600×600 + тёплый пол | Керамогранит 600×600 | Натяжной влагост. | 4,1 м² |
| 3 | Кухня | Ламинат 33 кл. | Краска; фартук керамогранит | Натяжной | ~6,5 м² |
| 4 | Гостиная | Ламинат 33 кл. | Краска; ТВ-стена — рейки | Натяжной | ~13 м² |
| 5 | Спальня | Ламинат 33 кл. | Краска | Натяжной | ~7,5 м² |
| 6 | Лоджия | Керамогранит | Краска | Натяжной / покраска | 2,7 м² |

### Ведомость отделки

| Элемент | Кол-во |
|---|---|
| Ламинат (с запасом 7%) | 29 м² |
| Керамогранит пол | 13 м² |
| Керамогранит стены санузла | 20 м² |
| Фартук кухни | 2,5 м² |
| Стены под покраску | ~90 м² |
| Натяжной потолок | ~36 м² |
| Плинтус | 30 м |
| Нагревательный мат | 6 м² |

### Ведомость электрики

| Электрика | Кол-во |
|---|---|
| Розетки | 16 |
| Силовые выводы | 7 |
| Выключатели / выводы света | 21 |
| Слаботочные точки | 3 |
| Споты встраиваемые | 9 |
| Подвес / бра | 1 / 2 |
| LED-лента | 5 м |
| Терморегуляторы | 2 |

### Ведомость сантехники

| Сантехника | Кол-во |
|---|---|
| Ванна акриловая 1700×700 | 1 |
| Унитаз подвесной + инсталляция | 1 |
| Тумба с раковиной 750 | 1 |
| Смесители (ванна, раковина, кухня) | 3 |
| Мойка кухонная | 1 |
| Полотенцесушитель эл. | 1 |
| Точки воды / канализации | 17 |

### Палитра

Стены: светло-серый тёплый

Потолок, фасады: молочно-белый

Пол: светлый дуб

Столешница, плитка: светлый камень

Текстиль: серо-бежевый

Рама, ручки, светильники: чёрный матовый

Встроенная мебель: шкаф-купе 2400×600 до потолка (4 створки, зеркало); ТВ-стена из реек 1980 с подсветкой; кухня 3,36 пог. м, верх до потолка, фасады без ручек; стеклянная раздвижная перегородка 3220 (4 створки); шкаф в спальню 2330×600; дверь санузла 700.

Техника: холодильник (колонна), варочная индукционная, вытяжка встраиваемая, микроволновка, стиральная машина, посудомойка 45 см, кондиционер, телевизор 55".

| Стадия | Лист | Листов | Квартира 72 · ЖК Buta Zaman · Алматы |
|---|---|---|---|
| РД | 21 | 22 | Ведомость материалов<br>26.10.2026 · M — · A3 |

# Смета

**Сводная смета (цены satu.kz, Алматы, 29.09.2026; работа мастеров — ориентировочно)**

| Раздел | Когда | Сумма, ₸ |
|---|---|---|
| 1. Стены санузла, штукатурка, стяжка | недели 1–3 | 1 735 500 |
| 2. Сантехника черновая | недели 1–2 | 238 000 |
| 3. Электрика черновая | неделя 2 | 410 000 |
| 4. Тёплый пол | неделя 5 | 78 000 |
| 5. Плитка | неделя 5 | 360 950 |
| 6. Стены, потолок, пол | недели 6–7 | 663 800 |
| 7. Электрика чистовая | неделя 8 | 205 000 |
| 8. Сантехника чистовая | неделя 8 | 535 000 |
| 9. Встроенная мебель | замер — неделя 4, установка — неделя 8 | 1 700 000 |
| 10. Техника | к установке кухни | 1 270 000 |
| 11. Мебель и текстиль | в конце | 1 130 000 |
| 12. Прочее | весь ремонт | 288 000 |
| Итого | | 8 614 250 |
| Запас 10 % | | 861 425 |
| Всего с запасом | | 9 475 675 |

| Крупнейшие позиции | Кол-во | Цена | Сумма | Разд. |
|---|---|---|---|---|
| Работа строительной бригады под ключ, 40 000 ₸ | 37.4 м² | 40 000 | 1 496 000 | 1 |
| Стеклянная раздвижная перегородка 3,2 м до пот | 1 шт | 600 000 | 600 000 | 9 |
| Кухонный гарнитур ~4 пог. м, эконом (от 40–80 | 1 шт | 450 000 | 450 000 | 9 |
| Шкаф-купе 2,4 × 0,6 до потолка, 4 двери; секци | 1 шт | 330 000 | 330 000 | 9 |
| Диван | 1 шт | 300 000 | 300 000 | 11 |
| Шкаф в спальню 2,3 × 0,6 до потолка, 4 распашн | 1 шт | 280 000 | 280 000 | 9 |
| Кондиционер с монтажом и трассой | 1 шт | 280 000 | 280 000 | 10 |
| Холодильник | 1 шт | 250 000 | 250 000 | 10 |
| Ламинат 33 класс (Tarkett / Navigator) | 28 м² | 8 300 | 232 400 | 6 |
| Посудомоечная машина 45 см встраиваемая | 1 шт | 200 000 | 200 000 | 10 |
| Стиральная машина узкая, глубина 40 см (в шкаф | 1 шт | 180 000 | 180 000 | 10 |
| Натяжной потолок матовый с монтажом — уточнить | 36 м² | 4 500 | 162 000 | 6 |
| Керамогранит Medici PM213460 200×200 на пол пр | 5.5 м² | 28 900 | 158 950 | 5 |
| Телевизор | 1 шт | 150 000 | 150 000 | 10 |
| Кровать 160×200 | 1 шт | 150 000 | 150 000 | 11 |
| Матрас 160×200 | 1 шт | 150 000 | 150 000 | 11 |
| Керамогранит 60×60 / 60×120: санузел стены и п | 29 м² | 5 000 | 145 000 | 5 |
| Кабель ВВГнг-LS 3×2,5 (розетки, техника, тёплы | 200 м | 720 | 144 000 | 3 |
| Варочная панель индукционная | 1 шт | 120 000 | 120 000 | 10 |
| Стол + 2 стула | 1 компл | 100 000 | 100 000 | 11 |
| Шторы + скрытый карниз (окно спальни + тюль на | 1 компл | 100 000 | 100 000 | 11 |
| Вывоз мусора, доставка, подъём материалов | 1 усл | 100 000 | 100 000 | 12 |
| Гипсовая штукатурка (Ротбанд / Vetonit), 30 кг | 35 меш | 2 800 | 98 000 | 1 |
| Рейки на ТВ-стену 1,3×3 м: рейка 40 мм, шаг 60 | 1 компл | 90 000 | 90 000 | 11 |

Полная смета по всем позициям (с редактированием цен) — на сайте проекта: leylagxx.github.io/kvartira72

Работа по сантехнике не учтена (выполняется своими силами). Позиции, которые выгодно заказать из Китая, отмечены на сайте — экономия ~260 тыс. ₸.

| Стадия | Лист | Листов | Квартира 72 · ЖК Buta Zaman · Алматы |
|---|---|---|---|
| РД | 22 | 22 | Смета<br>26.10.2026 · М — · А3 |