ДИЗАЙН-ПРОЕКТ

Квартира № 72 · ЖК Buta Zaman · г. Алматы

Студия 37,4 м² (1 комн., тип 1, этаж 2–7) · высота потолка 3,0 м

Стиль: минимализм · спальня за раздвижной стеклянной перегородкой · шкаф-купе в прихожей · ванна · тёплый пол в прихожей и санузле

Состав альбома


2. Обмерный план
3. Планировочное решение
4. План монтажа перегородок
5. Напольные покрытия
6. План осветительных приборов
7. План розеток
8. План выключателей
9. План потолка
10. План сантехнического оборудования
11. План радиаторов и тёплых полов
12. Развёртка стен: кухня
13. Развёртка стен: санузел
14. Развёртка стен: прихожая
15. Развёртка стен: гостиная
16. Развёртка стен: спальня
17. Визуализация
18. Ведомость материалов
19. Смета

Исполнитель: Claude (ИИ-ассистент) по заданию владельца · 18.10.2026 · Не является официальной проектной документацией: нормы и сечения проверяют исполнители работ.

Стадия	Лист	Листов	Квартира 72 · ЖК Buta Zaman · Алматы
РД	1	19	Титульный лист 18.10.2026 · М — · А3

Обмерный план

КВАРТИРА 72

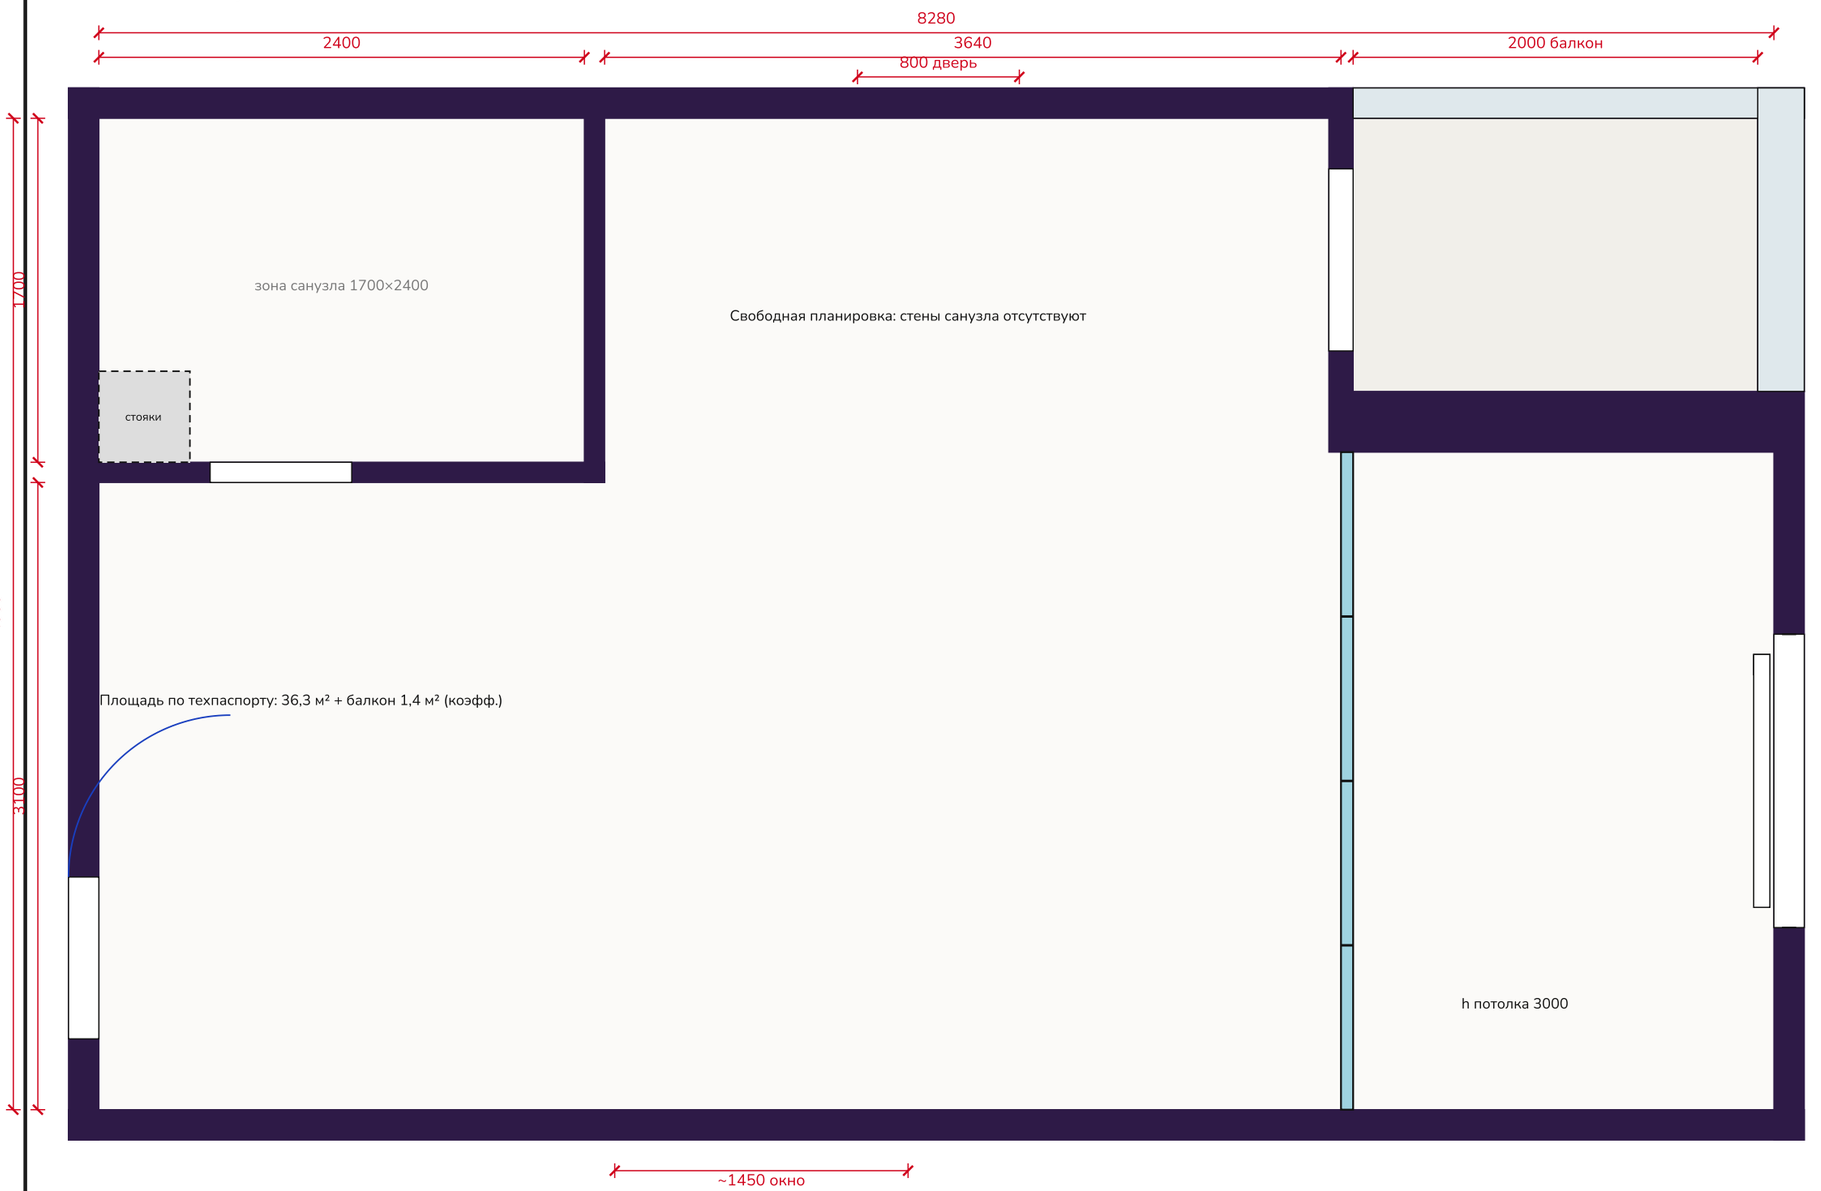

Условные обозначения

- Несущие стены (монолит)
- Возводимые перегородки (газоблок 100 мм)
- Стеклянная перегородка
- Стояки / вентканал (уточнить)


ПРИМЕЧАНИЯ:

1. За отметку 0.000 принят уровень чистового пола.
2. Все размеры уточнить по месту перед началом работ; привязки даны по неоштукатуренным стенам.
3. Положение короба стояков и вентканала уточнить после приёмки квартиры 10.10.2026.
4. Размеры в миллиметрах, площади в м².
5. По техпаспорту: 4,90×8,28; левая стена 6,20; выступ стенки санузла 1,70; балкон 1,35×2,00; ниша спальни 3,25.
6. Глубина санузла 2400 — проектная (стена возводится), ширина 1700 задана готовой стенкой со стояками.
7. Размер окна и балконной двери замерить по факту. Входная дверь открывается наружу.

Стадия	Лист	Листов	Квартира 72 · ЖК Buta Zaman · Алматы
РД	2	19	Обмерный план 18.10.2026 · М 1:30 · А3

Планировочное решение

КВАРТИРА 72

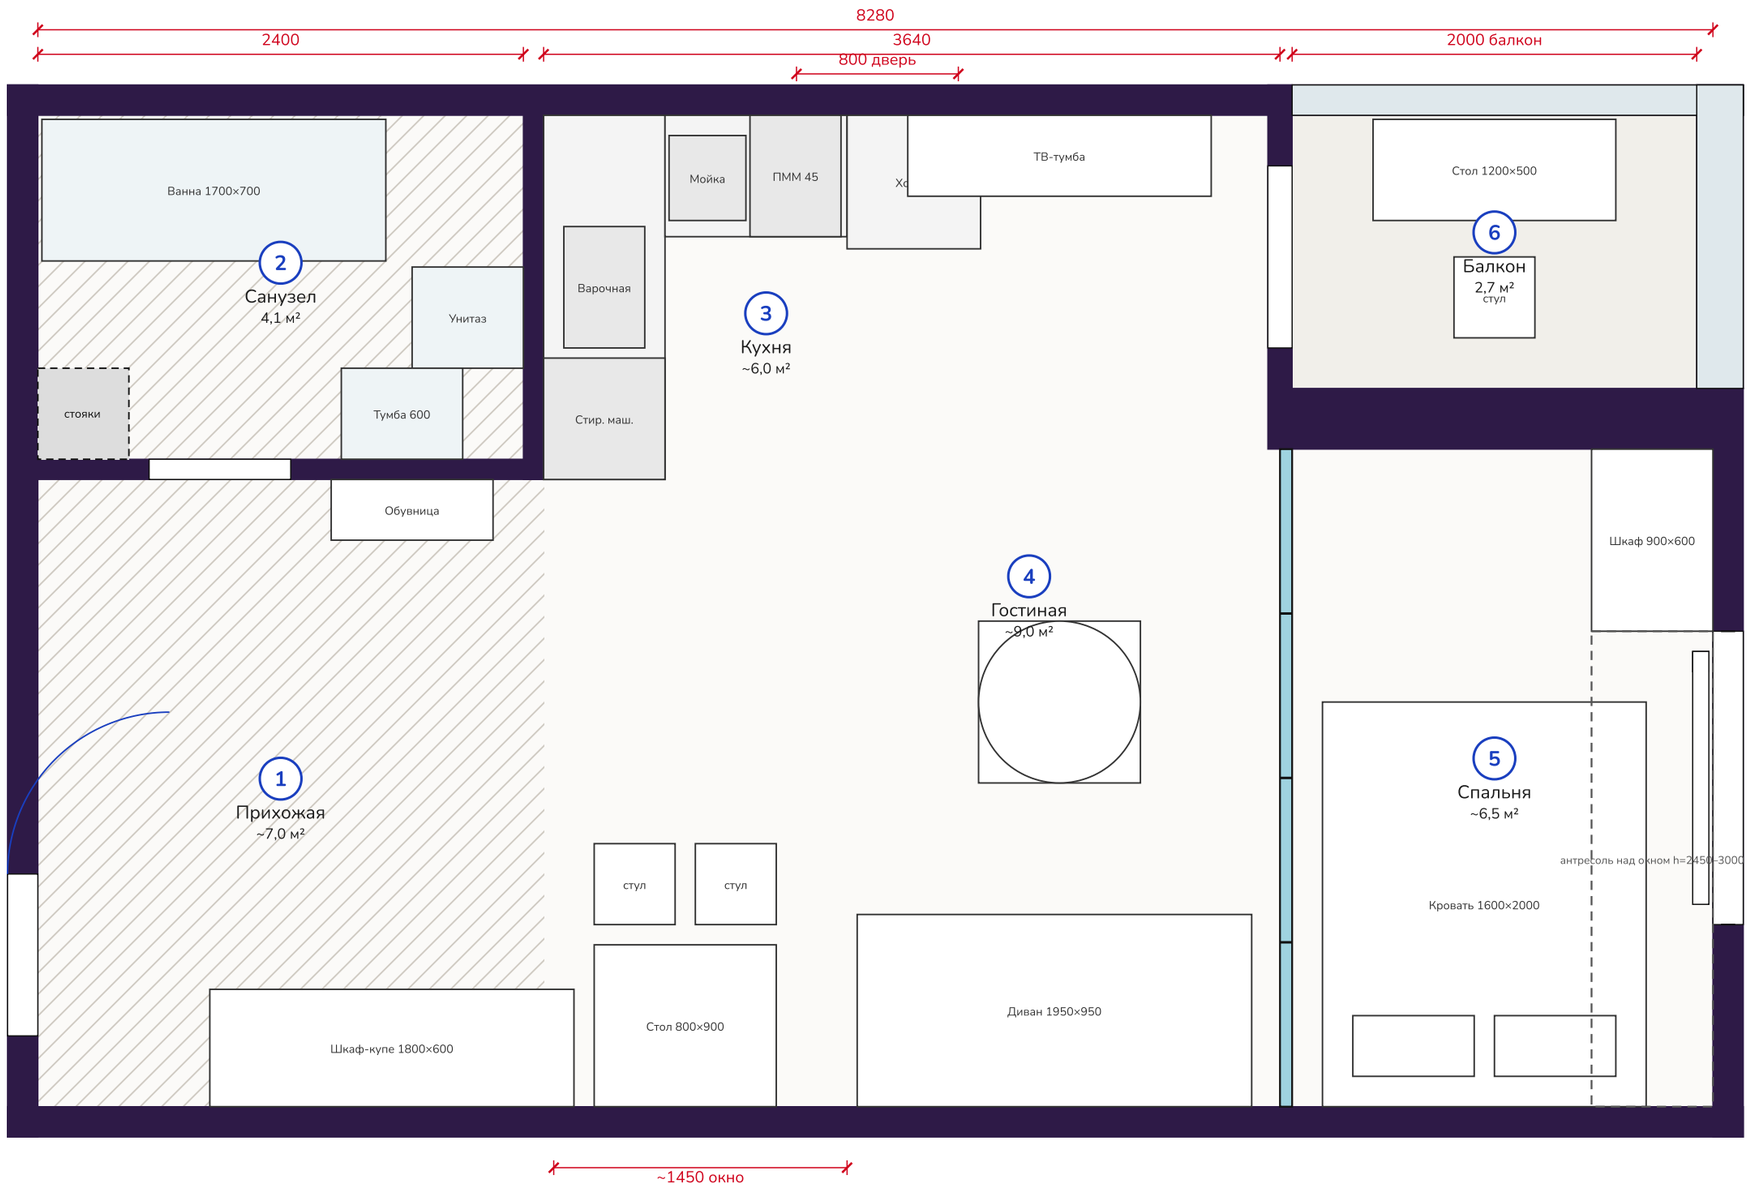

Спецификация помещений

№	Помещение	Площадь
1	Прихожая	~7,0 м²
2	Санузел	4,1 м²
3	Кухня	~6,0 м²
4	Гостиная	~9,0 м²
5	Спальня	~6,5 м²
6	Балкон	2,7 м²
	Итого	37,4 м²

Покрытия пола:

Ламинат 33 кл. — кухня, гостиная, спальня (~27 м²)

Керамогранит 600×600 — прихожая (~5 м²), санузел (~4 м²)

Балкон — керамогранит или плитка (~3 м²)


ПРИМЕЧАНИЯ:

1. За отметку 0.000 принят уровень чистового пола.
2. Все размеры уточнить по месту перед началом работ; привязки даны по неоштукатуренным стенам.
3. Положение короба стояков и вентканала уточнить после приёмки квартиры 10.10.2026.
4. Размеры в миллиметрах, площади в м².
5. Перегородка спальни: 4 раздвижные стеклянные створки в чёрном алюминиевом профиле, высота до потолка.
6. Спальня: шкаф-колонна 900×600 до потолка слева от окна, антресоль над окном 2450–3000, подоконник-полка 300 мм. Балкон: рабочий стол 1200×500 с полками вдоль остекления.

Стадия	Лист	Листов	Квартира 72 · ЖК Buta Zaman · Алматы
РД	3	19	Планировочное решение 18.10.2026 · М 1:30 · А3

План монтажа перегородок

КВАРТИРА 72

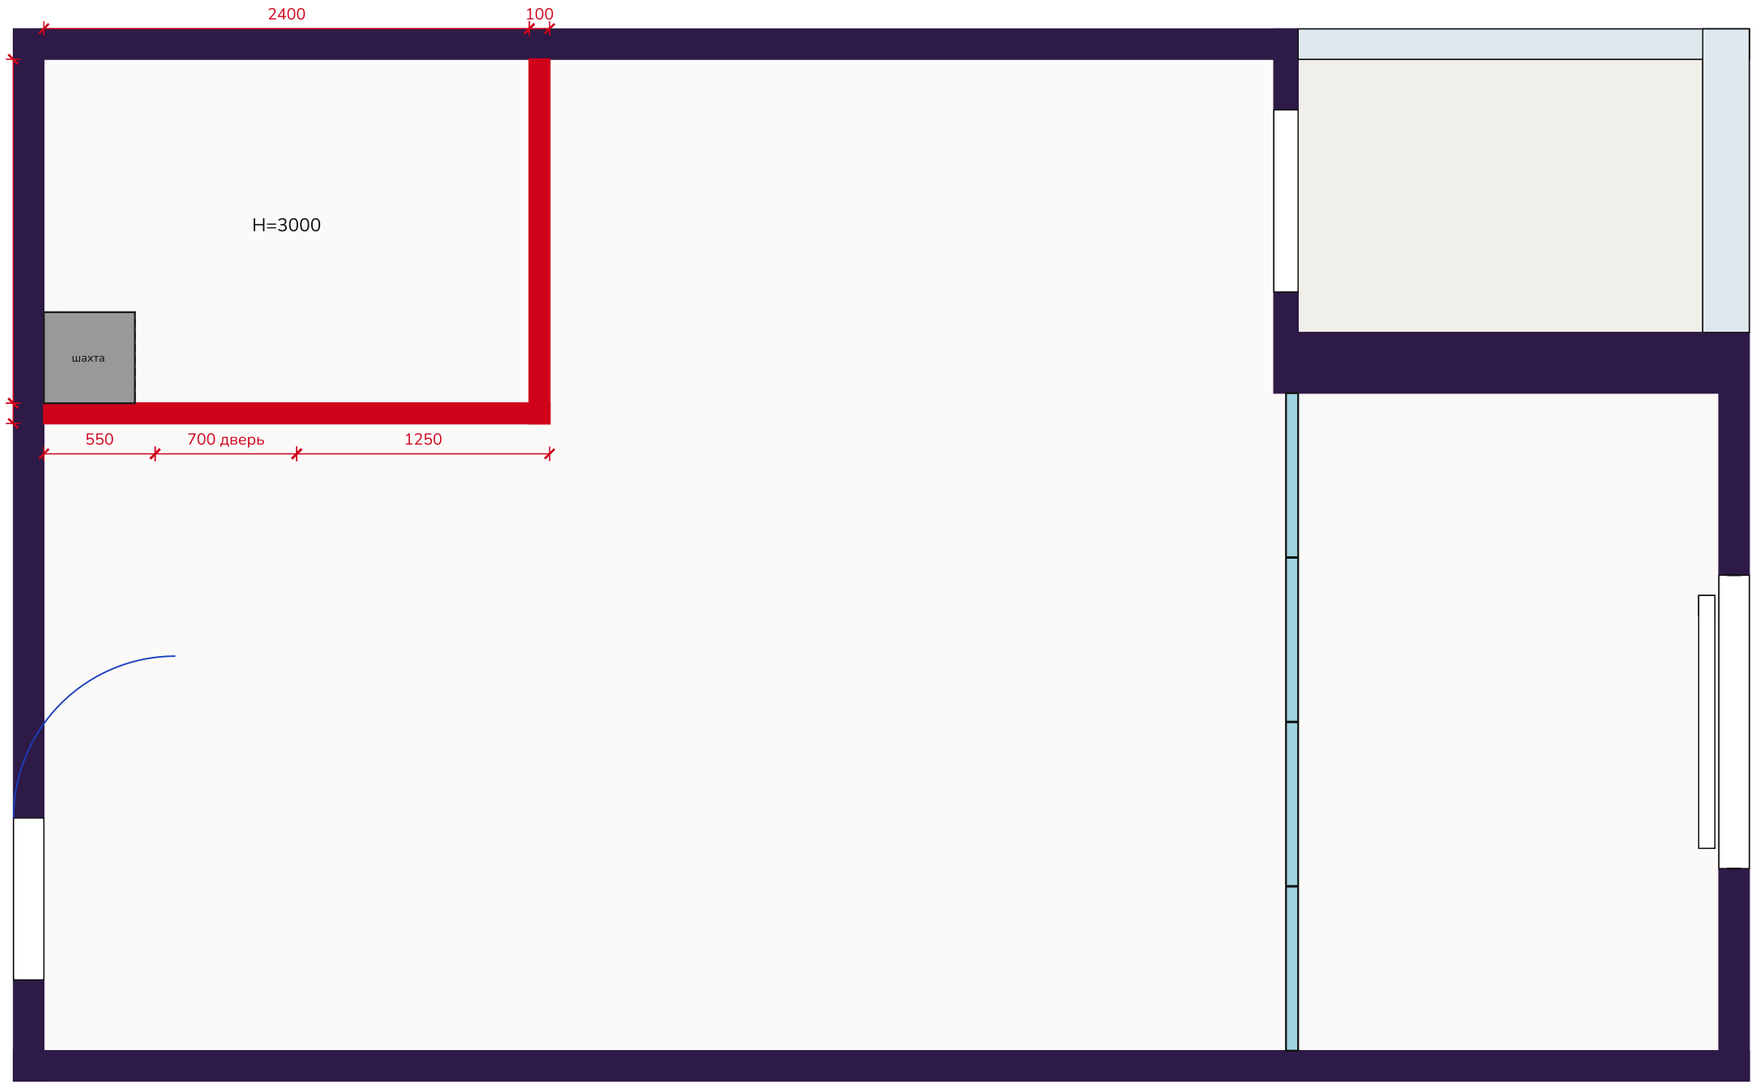

Условные обозначения

- Существующие стены
- Возводимые перегородки, газоблок 100 мм
- Короб стояков / вентшахта (ГКЛ влагостойкий, люк)
- Стеклянная раздвижная перегородка (монтаж на чистовой стадии)

Спецификация перегородок

Элемент	Длина	Высота	Площадь
Стена санузла с дверью	2 500	3 000	6,0 м²
Стена санузла (кухня)	1 800	3 000	5,4 м²
Итого газоблок 600×300×100			~70 шт + 10%


ПРИМЕЧАНИЯ:

1. За отметку 0.000 принят уровень чистового пола.
2. Все размеры уточнить по месту перед началом работ; привязки даны по неоштукатуренным стенам.
3. Положение короба стояков и вентканала уточнить после приёмки квартиры 10.10.2026.
4. Размеры в миллиметрах, площади в м².
5. Кладка на клей, армирование каждого 3-го ряда, примыкание к монолиту через анкеры.
6. Дверной проём 700×2100, перемычка — уголок или армированный ряд.

Стадия	Лист	Листов	Квартира 72 · ЖК Buta Zaman · Алматы
РД	4	19	План монтажа перегородок 18.10.2026 · М 1:30 · А3

Напольные покрытия

КВАРТИРА 72

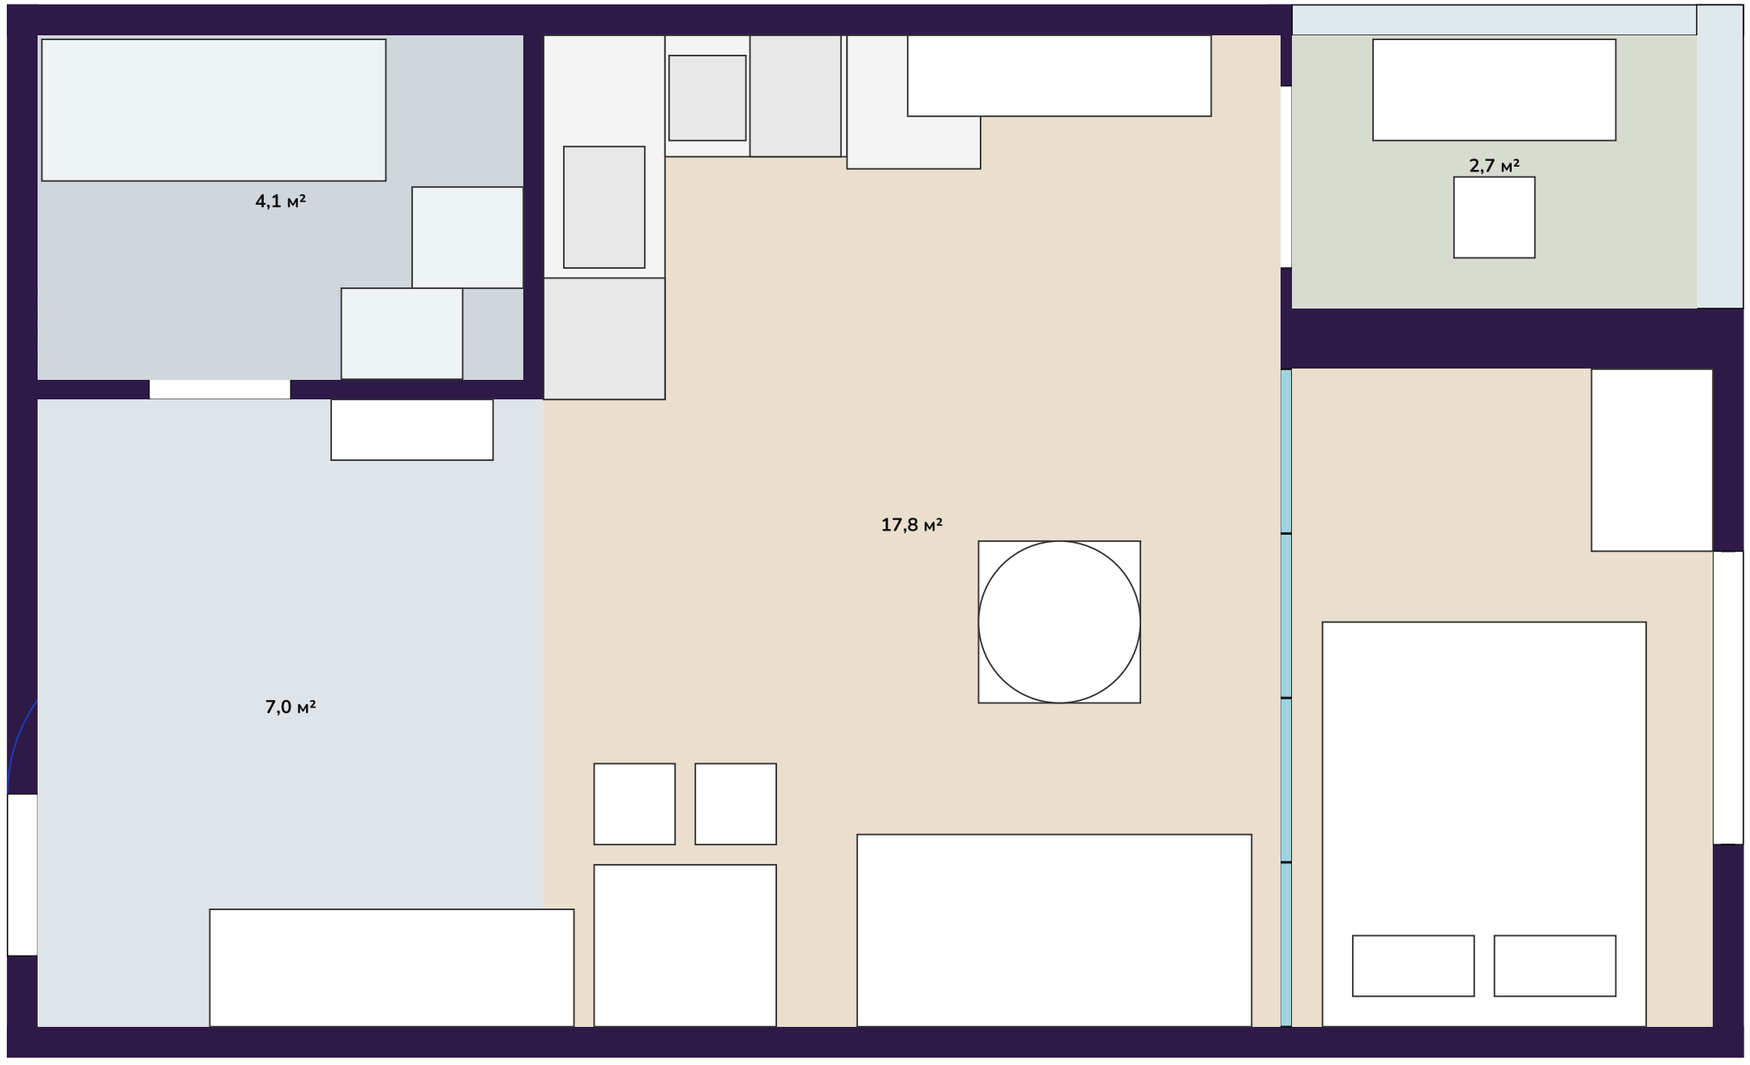

Спецификация

Покрытие	Площадь	С запасом
Ламинат 33 кл., 8 мм	24,6 м²	27 м² (+10%)
Керамогранит 600×600	11,1 м²	12,5 м² (+12%)
Балкон: керамогранит	2,7 м²	3 м²
Подложка 3 мм	24,6 м²	27 м²
Плинтус 60 мм	—	30 м
Порожек плитка/ламинат	—	1 шт (у санузла и прихожей)

Количество указано с запасом на подрезку.


ПРИМЕЧАНИЯ:

1. За отметку 0.000 принят уровень чистового пола.
2. Все размеры уточнить по месту перед началом работ; привязки даны по неоштукатуренным стенам.
3. Положение короба стояков и вентканала уточнить после приёмки квартиры 10.10.2026.
4. Размеры в миллиметрах, площади в м².
5. Ламинат укладывать вдоль длинной стороны (от входа к окну). Плитка прихожей и санузла на одном уровне с ламинатом через порожек.
6. Под плиткой в прихожей и санузле — электрический тёплый пол (см. план тёплых полов).

Стадия	Лист	Листов	Квартира 72 · ЖК Buta Zaman · Алматы
РД	5	19	Напольные покрытия 18.10.2026 · М 1:30 · А3

План осветительных приборов

КВАРТИРА 72

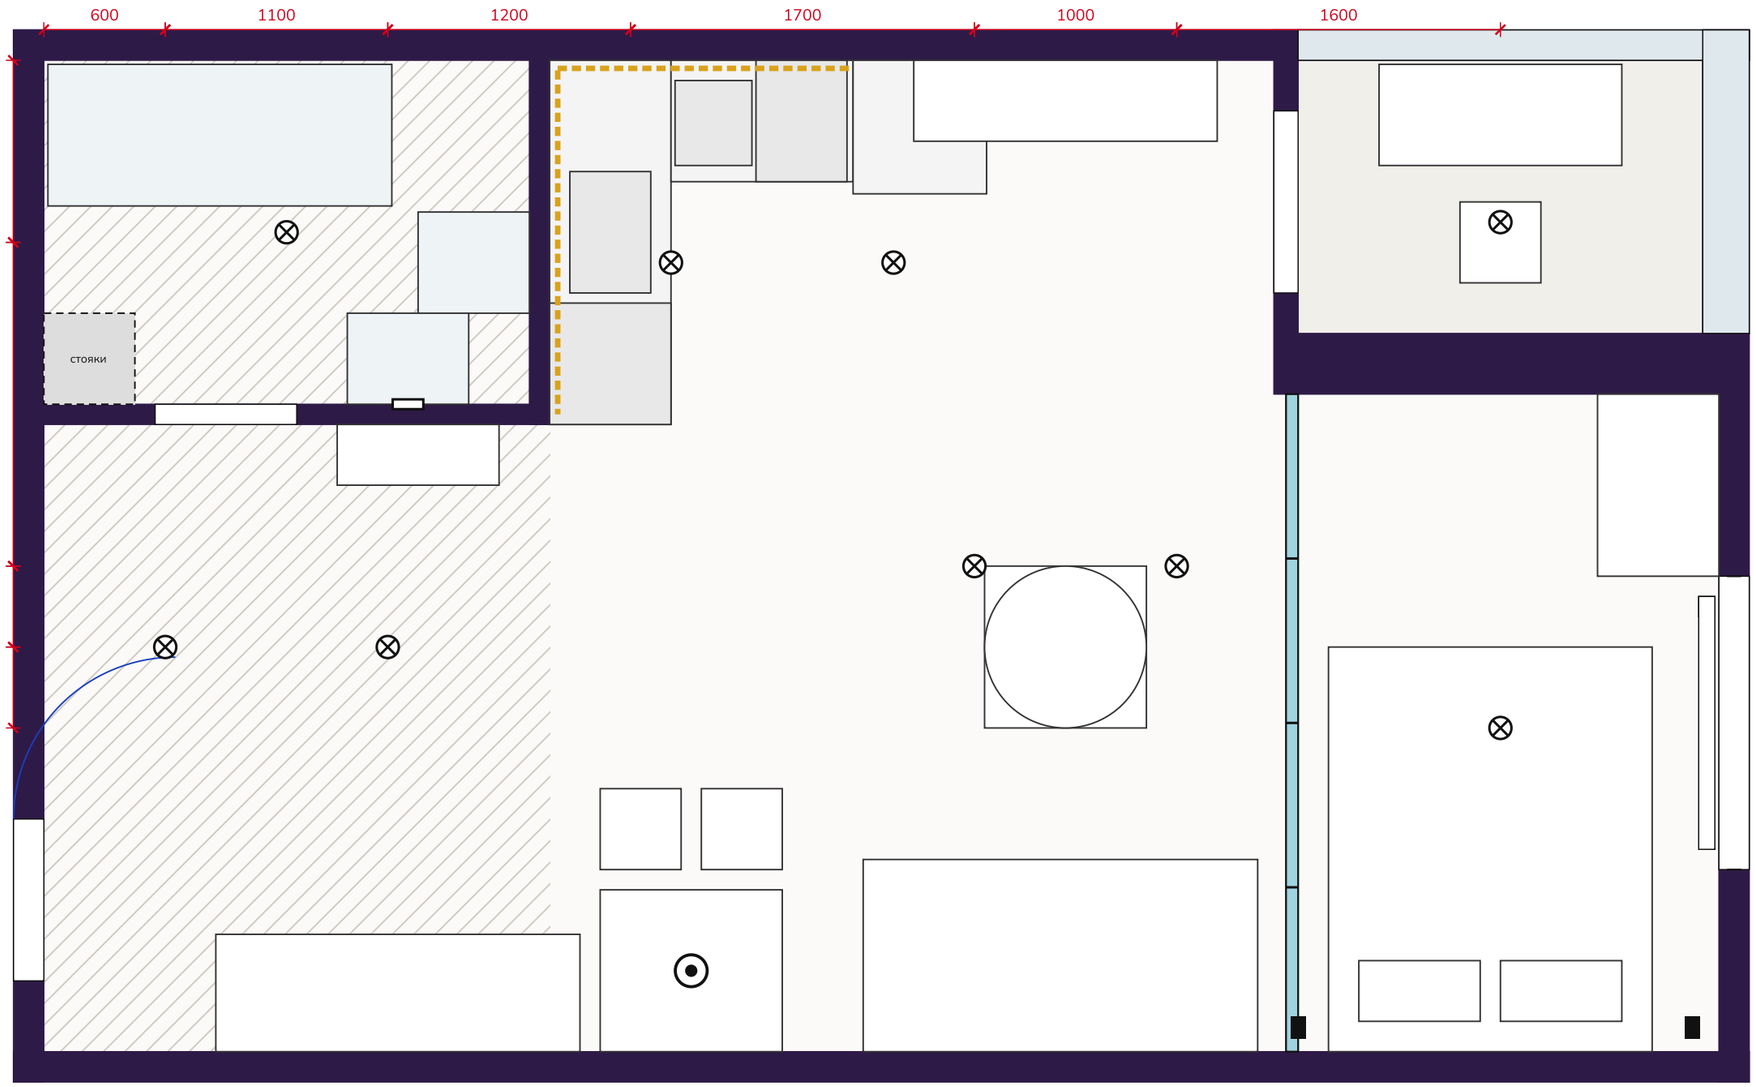

Условные обозначения

- Светильник накладной / встроенный, GX53
- Подвесной светильник над столом
- Бра, h=1300
- Светодиодная лента (подсветка кухни)
- Зеркало с подсветкой

Ведомость осветительных приборов

Наименование	Шт.
Светильник накладной GX53	9
Подвес над столом	1
Бра	2
LED-лента, м	5
Светящиеся полосы в рейках ТВ-стены	4
Зеркало с подсветкой	1
Вентилятор вытяжной	1


ПРИМЕЧАНИЯ:

1. За отметку 0.000 принят уровень чистового пола.
2. Все размеры уточнить по месту перед началом работ; привязки даны по неоштукатуренным стенам.
3. Положение короба стояков и вентканала уточнить после приёмки квартиры 10.10.2026.
4. Размеры в миллиметрах, площади в м².
5. Привязки даны к центру светильника.
6. Споты — на отдельных группах: прихожая+санузел, кухня, гостиная, спальня, балкон.

Стадия	Лист	Листов	Квартира 72 · ЖК Buta Zaman · Алматы
РД	6	19	План осветительных приборов 18.10.2026 · М 1:30 · А3

План розеток

КВАРТИРА 72

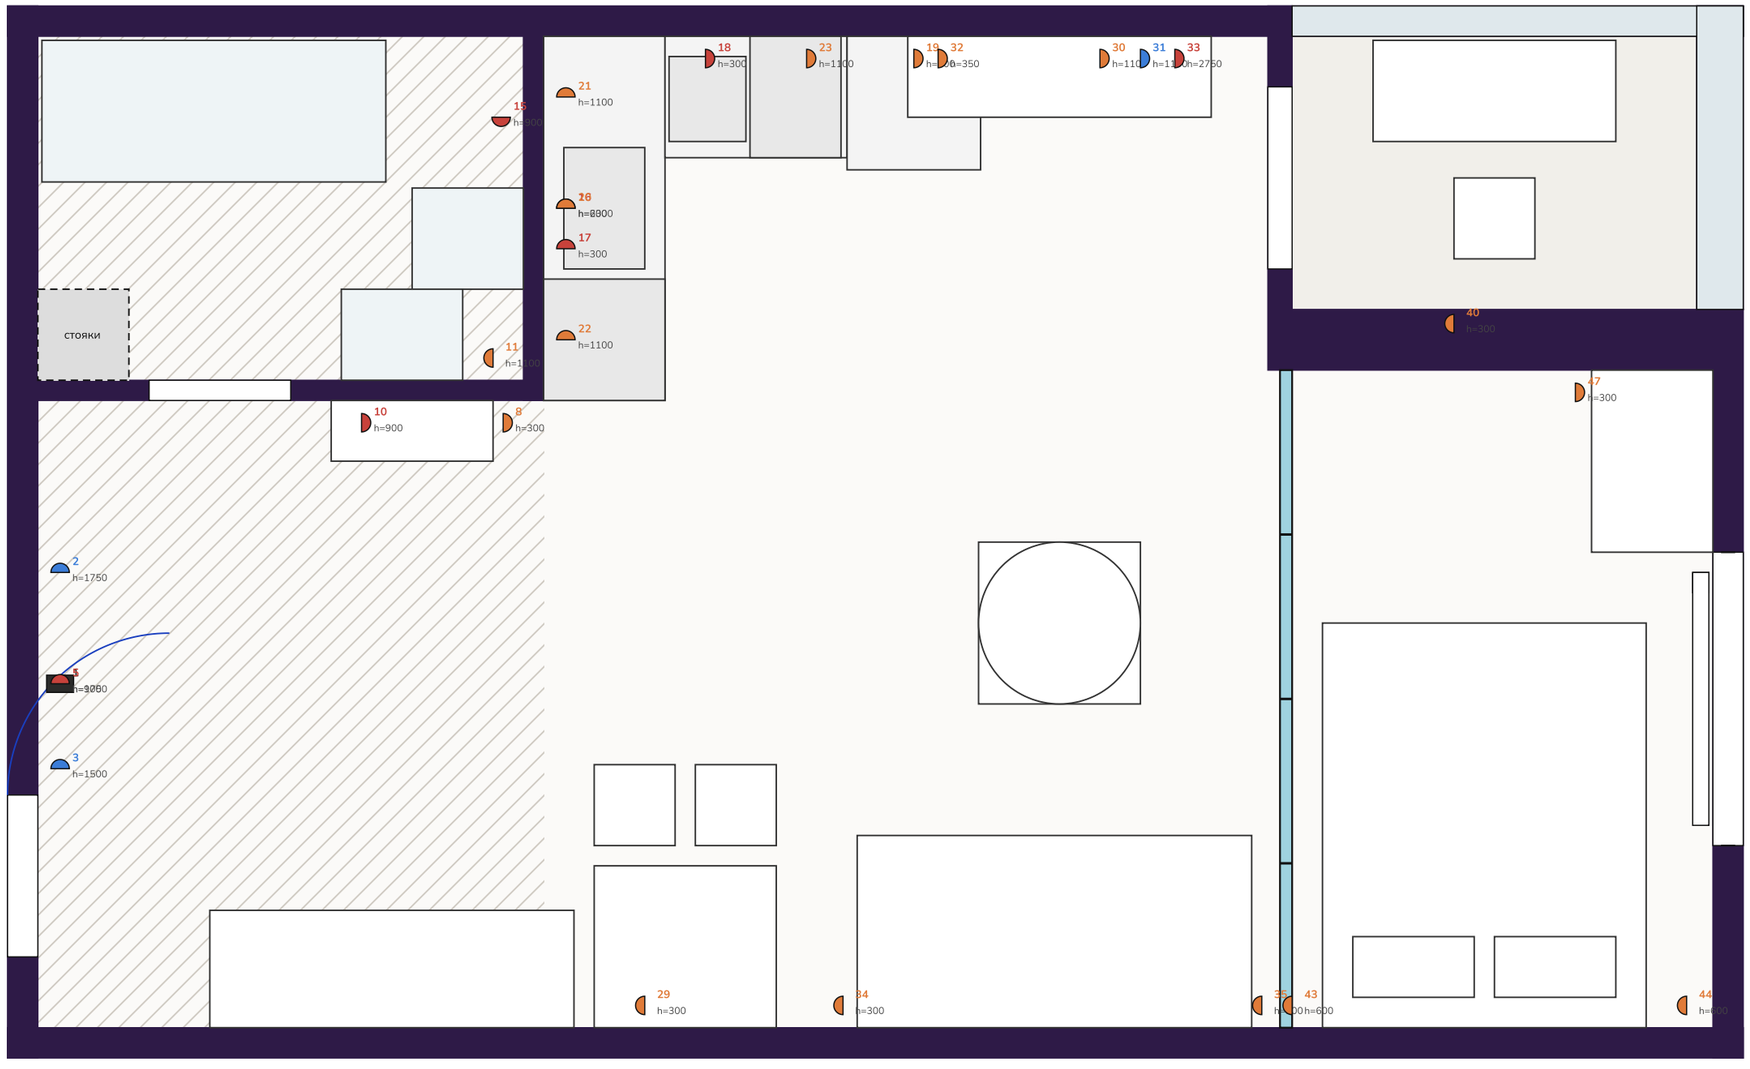

Условные обозначения

- Розетка (одинарная/двойная), h=300 если не указано
- Вывод для техники / отдельная линия
- Интернет, ТВ, домофон
- Электрощиток h=1750

Ведомость

Наименование	Кол-во
Розетки, в т.ч. с USB и IP44	16
Выводы силовых линий (техника, тёплый пол, полотенцесушитель, кондиционер)	7
Слаботочные точки	3
Щиток	1


ПРИМЕЧАНИЯ:

1. За отметку 0.000 принят уровень чистового пола.
2. Все размеры уточнить по месту перед началом работ; привязки даны по неоштукатуренным стенам.
3. Положение короба стояков и вентканала уточнить после приёмки квартиры 10.10.2026.
4. Размеры в миллиметрах, площади в м².
5. Высоты — до центра розетки от чистого пола. Номера точек — см. таблицу на сайте.
6. Отдельные автоматы: плита 32А, стиральная, посудомоечная, кондиционер, каждый тёплый пол. УЗО на все розеточные группы.

Стадия	Лист	Листов	Квартира 72 · ЖК Buta Zaman · Алматы
РД	7	19	План розеток 18.10.2026 · М 1:30 · А3

План выключателей

КВАРТИРА 72

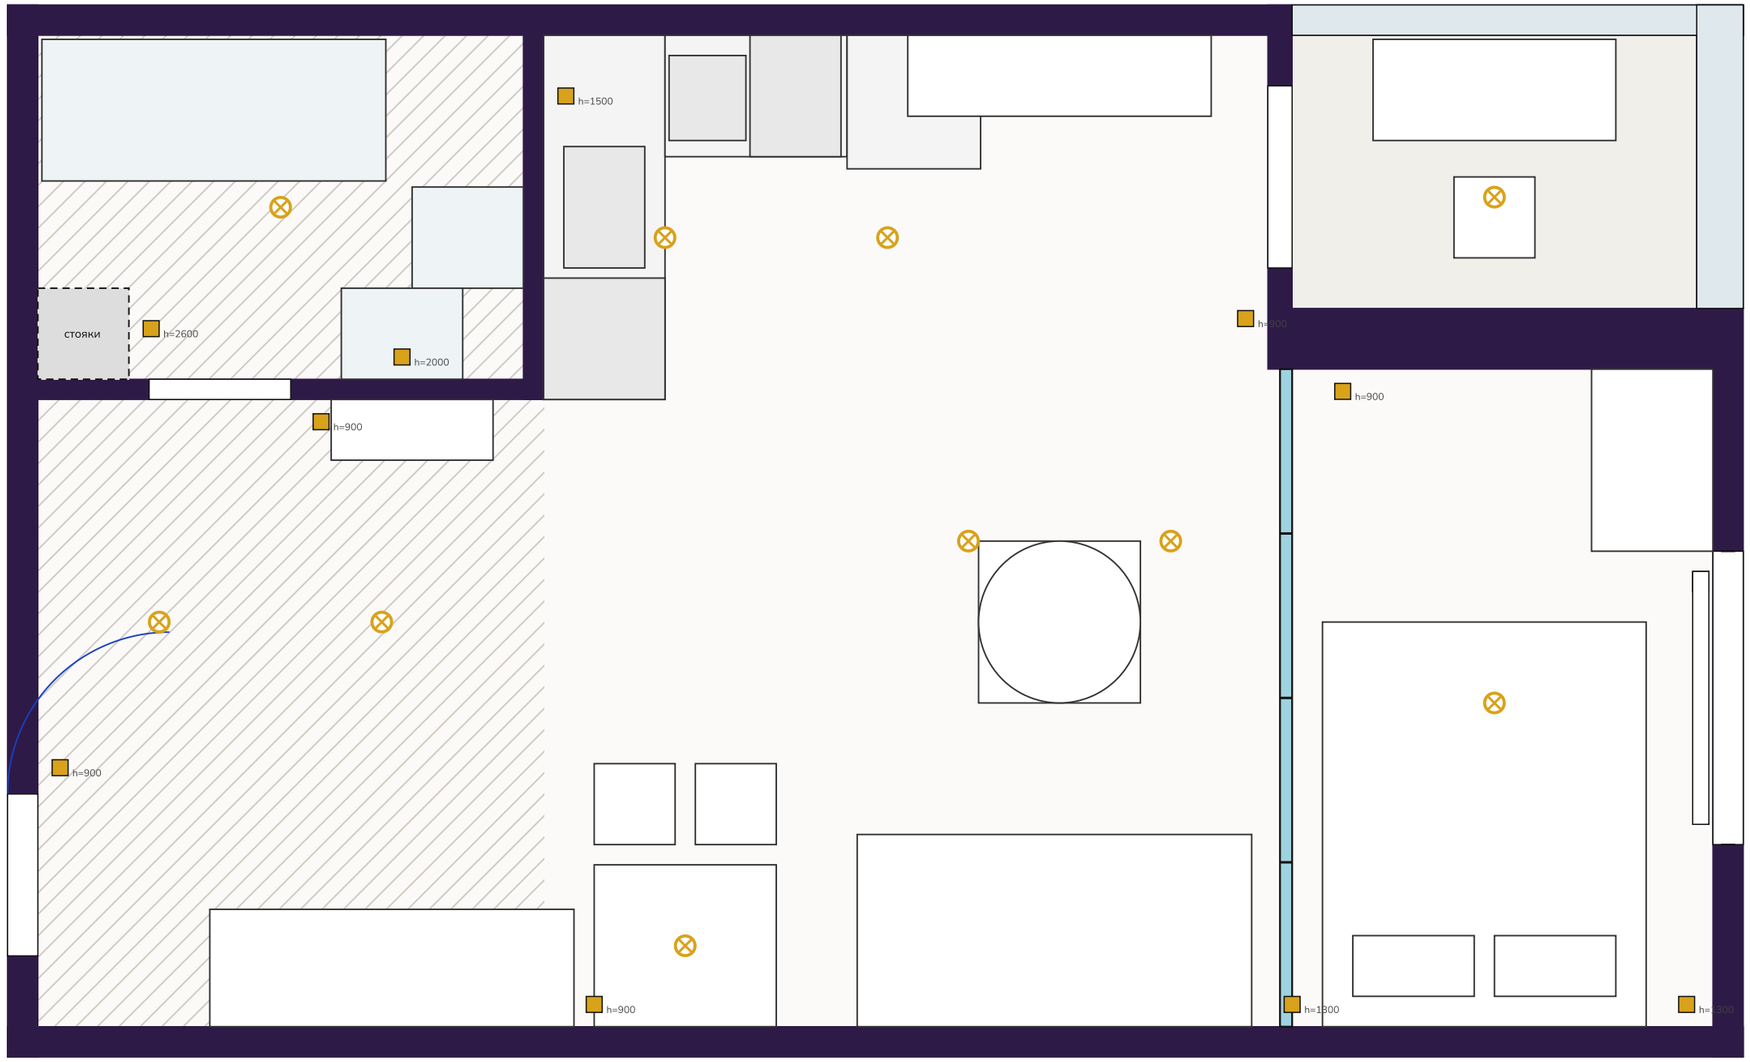

Условные обозначения

- Выключатель, h=900 (если не указано иное)
- Вывод под светильник на потолке

Ведомость выключателей и выводов

Выключатель / вывод	h, мм
Выключатель света прихожей	900
Выключатель санузла + вентилятор	900
Подсветка зеркала	2000
Вытяжной вентилятор (в вентканал)	2600
Подсветка под верхними шкафами	1500
Выключатели: кухня, стол, гостиная	900
Выключатель света балкона	900
Выключатель у двери	900
Бра у кровати	1300
Бра у кровати	1300


ПРИМЕЧАНИЯ:

1. За отметку 0.000 принят уровень чистового пола.
2. Все размеры уточнить по месту перед началом работ; привязки даны по неоштукатуренным стенам.
3. Положение короба стояков и вентканала уточнить после приёмки квартиры 10.10.2026.
4. Размеры в миллиметрах, площади в м².
5. Выключатели у входа в каждую зону со стороны ручки двери. Споты — на отдельных группах: прихожая+санузел, кухня, гостиная, спальня, балкон.

Стадия	Лист	Листов	Квартира 72 · ЖК Buta Zaman · Алматы
РД	8	19	План выключателей 18.10.2026 · М 1:30 · А3

План потолка

КВАРТИРА 72

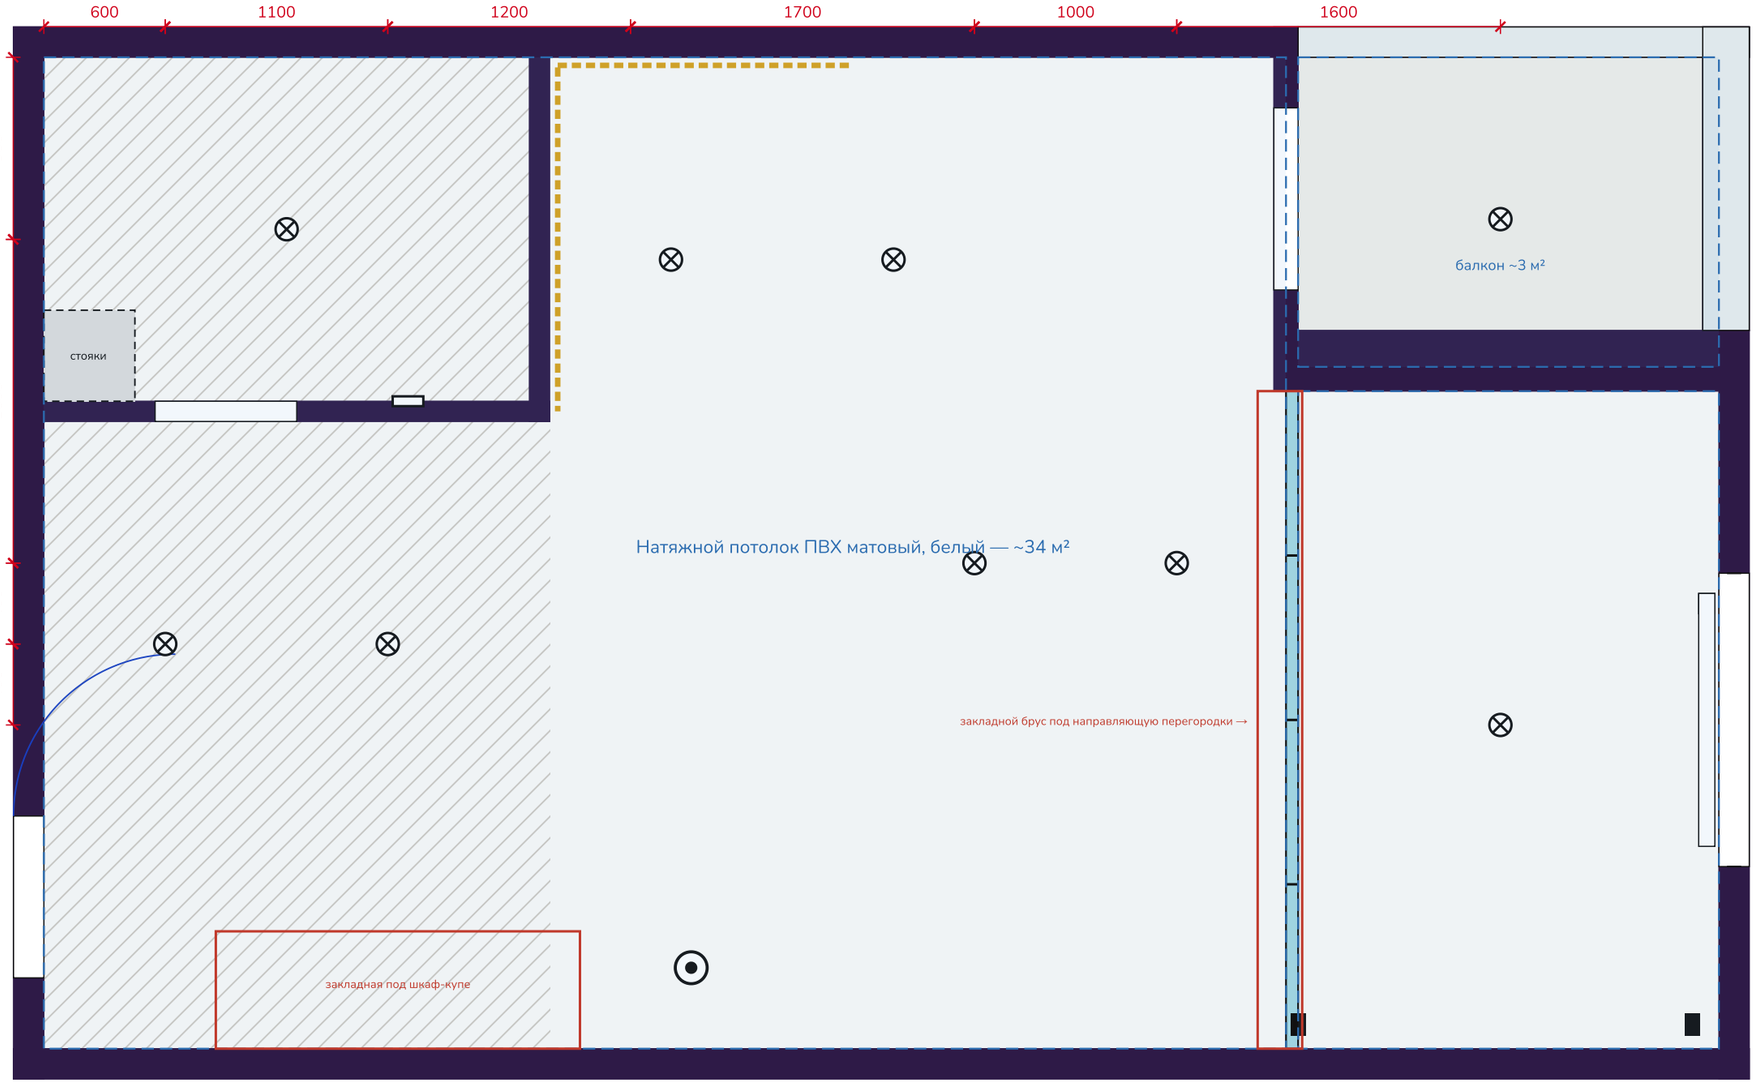

Условные обозначения

- ⊗ Спот накладной GX53, 9 шт.
- Граница натяжного потолка
- Закладные (брус) до монтажа потолка

Высота чистого потолка: 3000 – 40 = ~2960 мм

Перегородка и шкаф-купе крепятся к закладным, не к полотну.


ПРИМЕЧАНИЯ:

1. За отметку 0.000 принят уровень чистового пола.
2. Все размеры уточнить по месту перед началом работ; привязки даны по неоштукатуренным стенам.
3. Положение короба стояков и вентканала уточнить после приёмки квартиры 10.10.2026.
4. Размеры в миллиметрах, площади в м².
5. Монтаж потолка — после покраски стен и до ламината; трасса кондиционера и кабели спотов — до потолка.

Стадия	Лист	Листов	Квартира 72 · ЖК Buta Zaman · Алматы
РД	9	19	План потолка 18.10.2026 · М 1:30 · А3

План сантехнического оборудования

КВАРТИРА 72

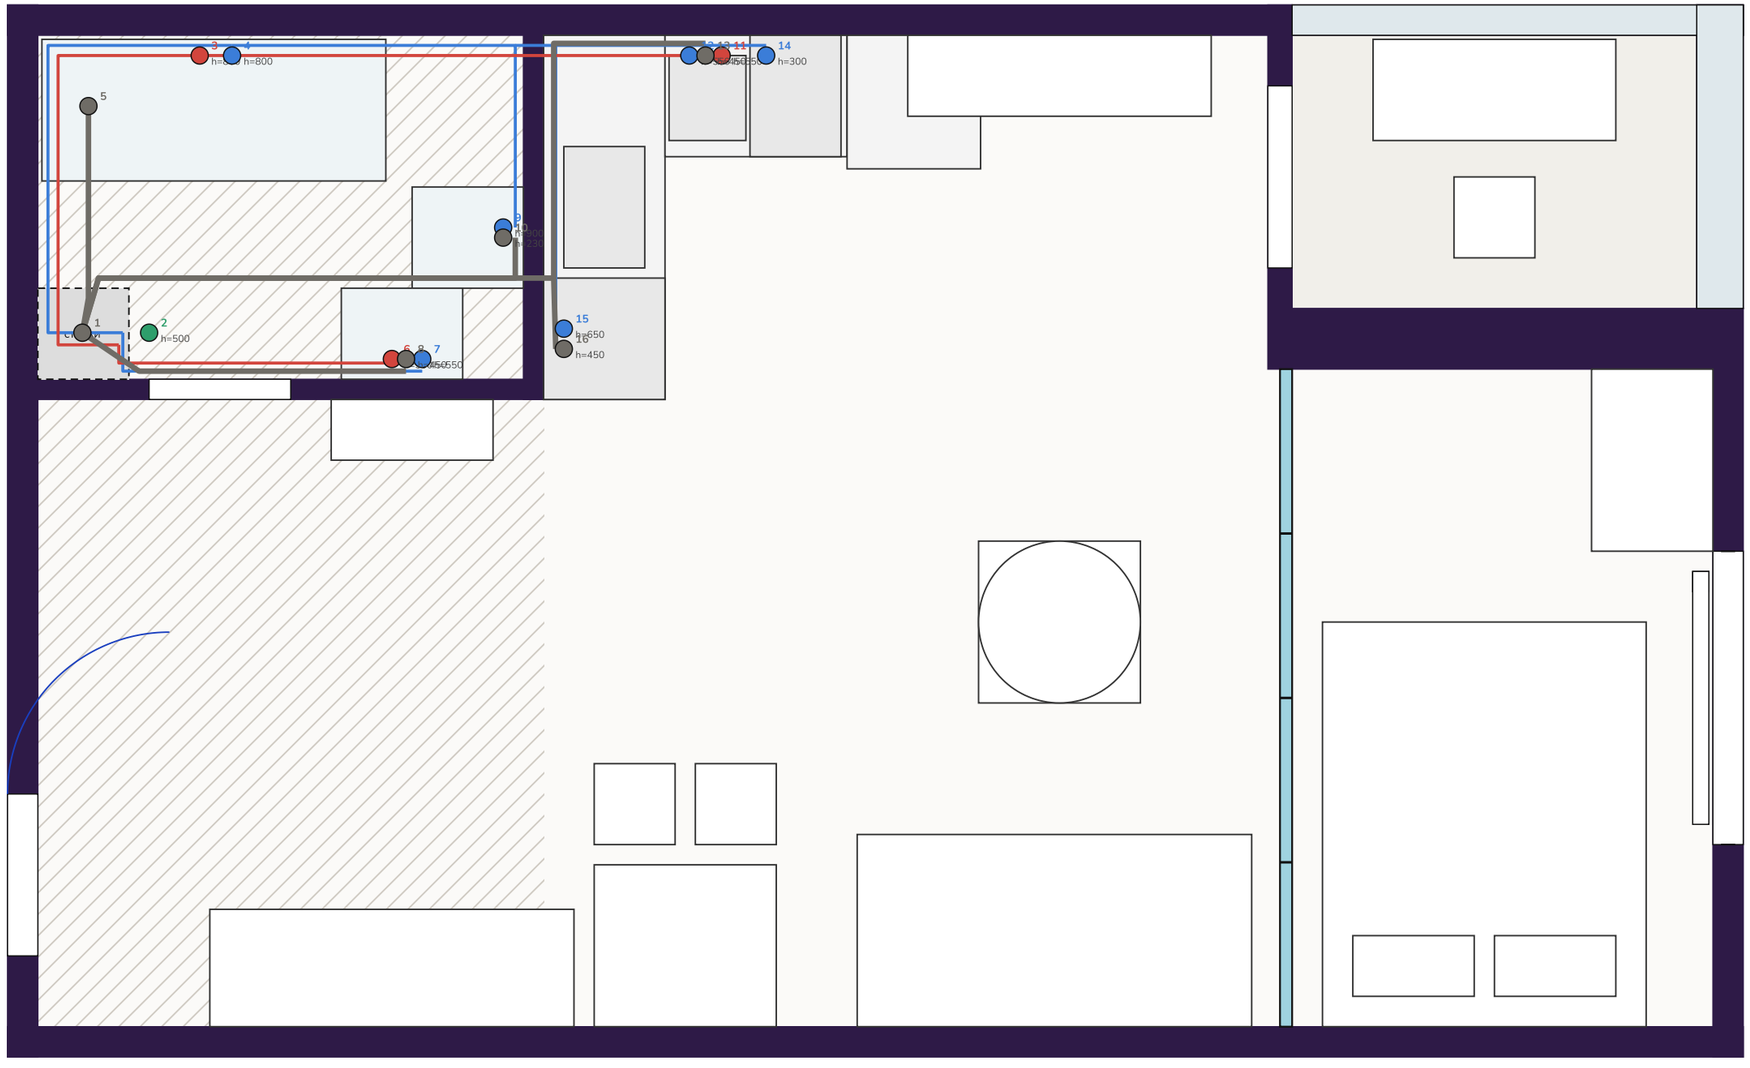

Условные обозначения

- Холодная вода
- Горячая вода
- Канализация Ø50 / Ø110
- Краны, фильтры, счётчики
- Точка вывода (номер — см. таблицу)

Ведомость точек

№	Точка	h, мм
1	Стояки воды и канализации в коробе у входной сте	—
2	Краны, счётчики, фильтры (люк в коробе)	500
3	Ванна: смеситель, горячая	800
4	Ванна: смеситель, холодная	800
5	Ванна: слив Ø50 у торца	в полу
6	Раковина: горячая	550
7	Раковина: холодная	550
8	Раковина: слив Ø50	450
9	Унитаз: вода в инсталляцию	900
10	Унитаз: канализация Ø110	230
11	Мойка: горячая	550
12	Мойка: холодная	550
13	Мойка: слив Ø50	450
14	Посудомойка: кран на холодной, слив в сифон мойк	300
15	Стиральная машина: кран холодной воды	650
16	Стиральная машина: слив Ø50 с сифоном	450


ПРИМЕЧАНИЯ:

1. За отметку 0.000 принят уровень чистового пола.
2. Все размеры уточнить по месту перед началом работ; привязки даны по неоштукатуренным стенам.
3. Положение короба стояков и вентканала уточнить после приёмки квартиры 10.10.2026.
4. Размеры в миллиметрах, площади в м².
5. Горячая — слева, холодная — справа. Уклон канализации 2–3 см/м к стояку.
6. Опрессовка труб до штукатурки. Стиральная и посудомоечная — через краны и сифоны с обратным клапаном.
7. Ванна 1700×700 (при тесном стояке — 1500–1600). Унитаз подвесной на инсталляции.

Стадия	Лист	Листов	Квартира 72 · ЖК Buta Zaman · Алматы
РД	10	19	План сантехнического оборудования 18.10.2026 · М 1:30 · А3

План радиаторов и тёплых полов

КВАРТИРА 72

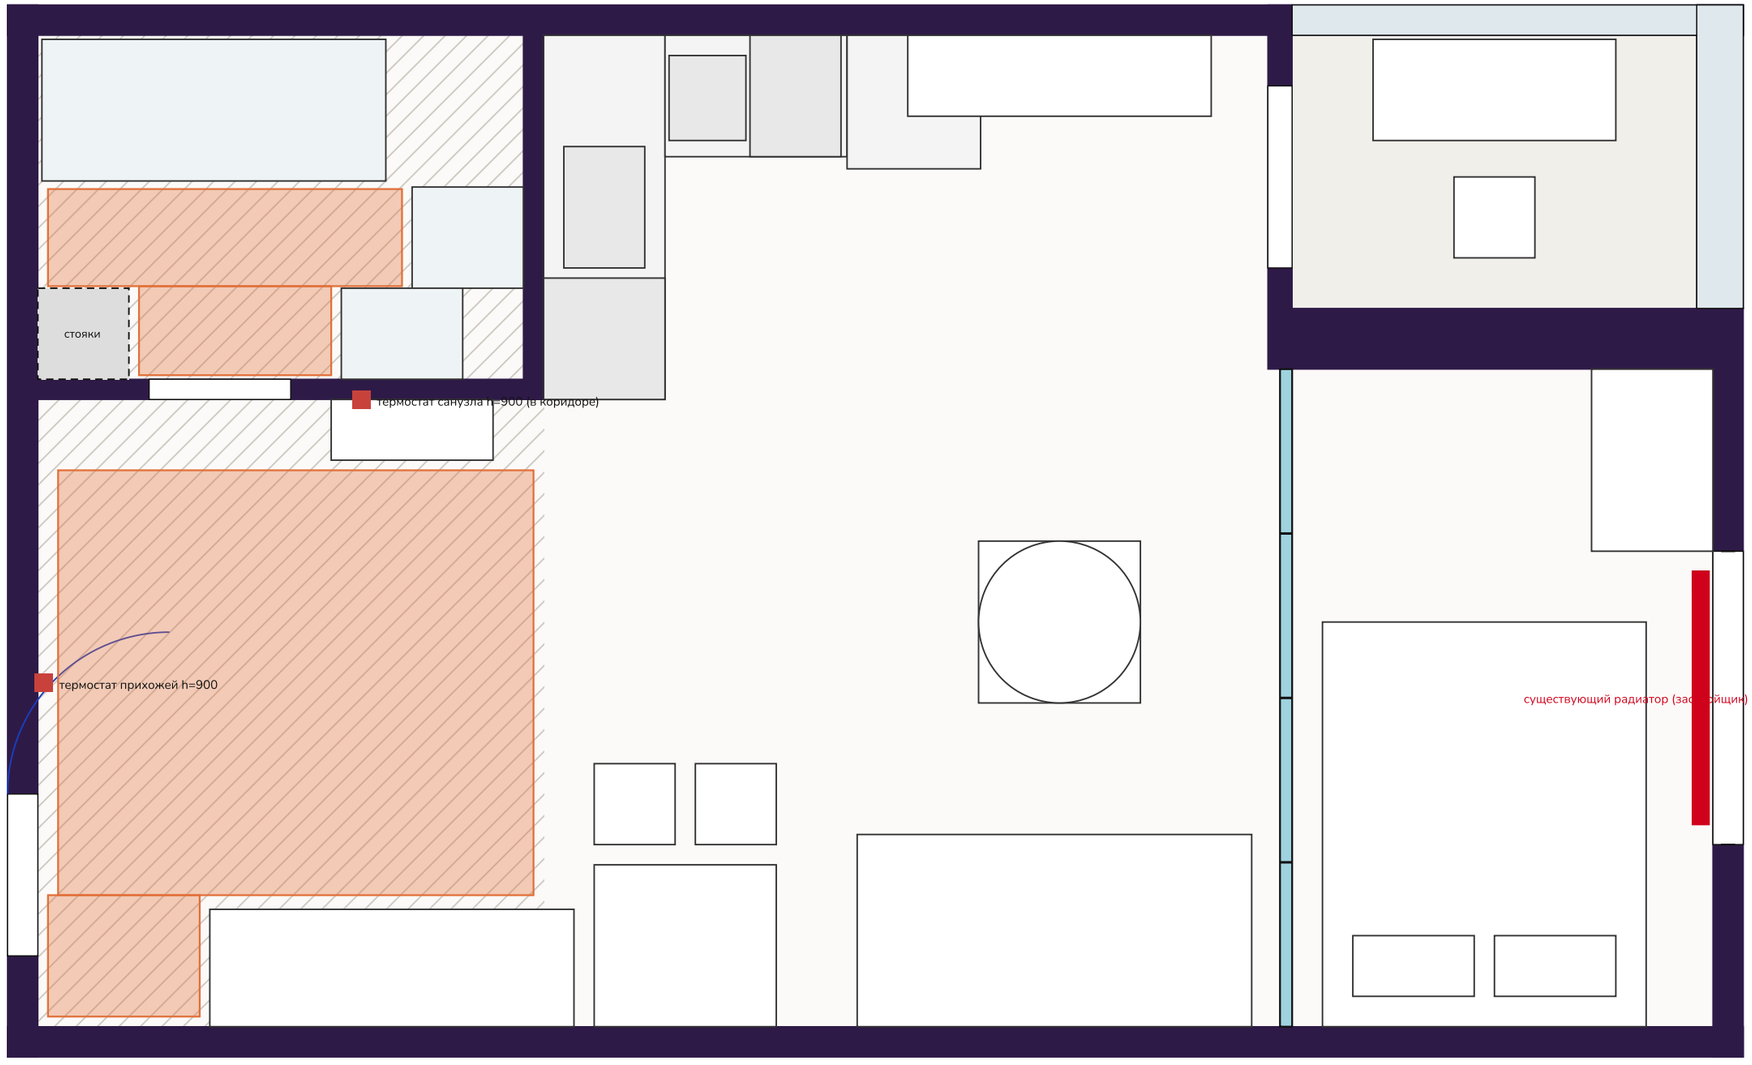

Условные обозначения

- Радиатор отопления (существующий)
- Электрический тёплый пол, мат 150 Вт/м²
- Термостат с датчиком пола

Ведомость

Элемент	Кол-во
Радиатор под окном	1 шт
Тёплый пол прихожая	5,0 м²
Тёплый пол санузел	1,3 м²
Термостаты	2 шт
Полотенцесушитель электрический	1 шт

ПРИМЕЧАНИЯ:


1. За отметку 0.000 принят уровень чистового пола.
2. Все размеры уточнить по месту перед началом работ; привязки даны по неоштукатуренным стенам.
3. Положение короба стояков и вентканала уточнить после приёмки квартиры 10.10.2026.
4. Размеры в миллиметрах, площади в м².
5. Радиатор не переносится; подоконник-полка над ним — с зазором для конвекции не менее 30 мм.
6. Мат под плитку в слой клея, датчик в гофре между витками, включение через 28 дней.

Стадия	Лист	Листов	Квартира 72 · ЖК Buta Zaman · Алматы
РД	11	19	План радиаторов и тёплых полов 18.10.2026 · М 1:30 · А3


КВАРТИРА 72


Развёртка стен: кухня

A — стена санузла (z=2500)

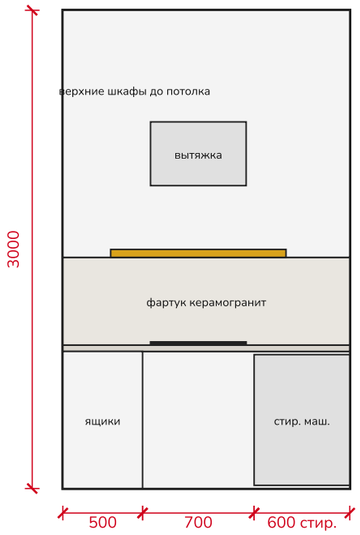

B — левая стена (x=0)

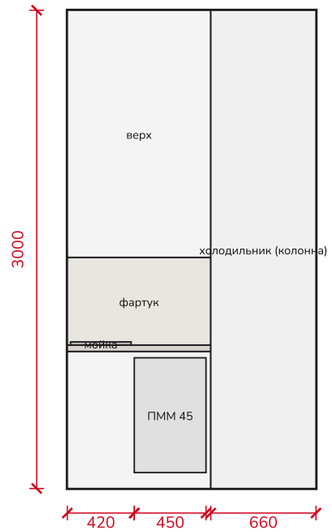

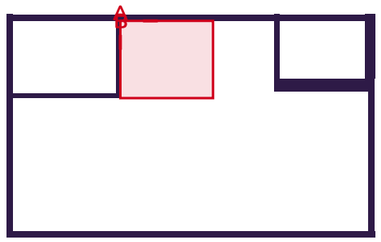

ключ-план

Стена под краску

8,5 м²

стены кухни над фартуком и свободные участки

Отметки: столешница 900 · фартук 900–1450 · верхние шкафы 1450–3000 · розетки над столешницей h=1100 · LED под верхними шкафами · вытяжка h=1900–2250.

Фасады белые матовые без ручек, столешница 38 мм светлый камень, фартук керамогранит 600×1200. Длина кухни 1,8 + 0,9 + колонна 0,66 м.


ПРИМЕЧАНИЯ:

1. За отметку 0.000 принят уровень чистового пола.
2. Все размеры уточнить по месту перед началом работ; привязки даны по неоштукатуренным стенам.
3. Положение короба стояков и вентканала уточнить после приёмки квартиры 10.10.2026.
4. Размеры в миллиметрах, площади в м².
5. Замер кухни — после штукатурки, установка — после пола и потолка.

Стадия	Лист	Листов	Квартира 72 · ЖК Buta Zaman · Алматы
РД	12	19	Развёртка стен: кухня 18.10.2026 · М 1:38 · А3

Развёртка стен: санузел



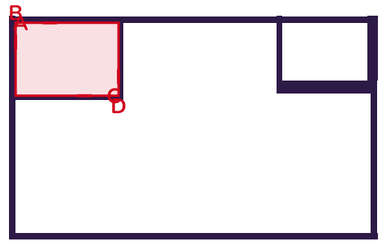

ключ-план

Санузел 1700 × 2400, h 2400 (натяжной потолок). Плитка керамогранит 600×600 стены и пол, швы 2 мм. Площади: стены ~19 м², пол 4,1 м², запас 10%.

Отметки: смеситель ванны 900 · штанга шторки 1900 · верх унитаза 400 · тумба 850 · зеркало 1200–1900 · розетка у зеркала 1100 (IP44) · вентилятор 2300 в вентканал короба.

Гидроизоляция обмазочная: пол + стены на 300 мм, зона ванны — на 1800 мм. Короб стояков — влагостойкий ГКЛ с ревизионным люком.

Стена под краску

0 м²

все стены — керамогранит 600×600, ~19 м²


ПРИМЕЧАНИЯ:

1. За отметку 0.000 принят уровень чистового пола.
2. Все размеры уточнить по месту перед началом работ; привязки даны по неоштукатуренным стенам.
3. Положение короба стояков и вентканала уточнить после приёмки квартиры 10.10.2026.
4. Размеры в миллиметрах, площади в м².
5. Положение короба стояков уточнить по месту; ванна остаётся вдоль левой стены.


Стадия	Лист	Листов	Квартира 72 · ЖК Buta Zaman · Алматы
РД	13	19	Развёртка стен: санузел 18.10.2026 · М 1:50 · А3

Развёртка стен: прихожая


A — правая стена (x=4900): шкаф-купе

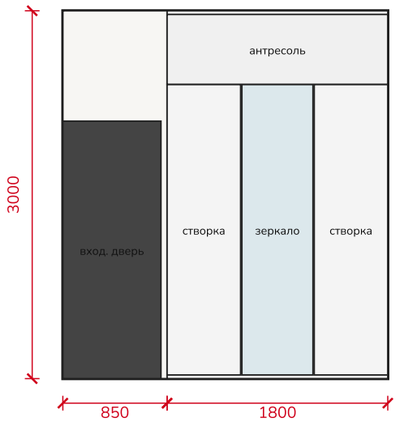


B — стена санузла (x=1800)

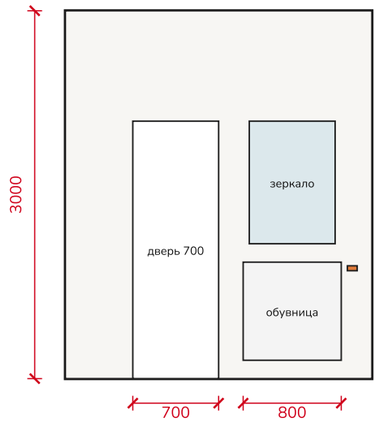

C — входная стена (z=0)

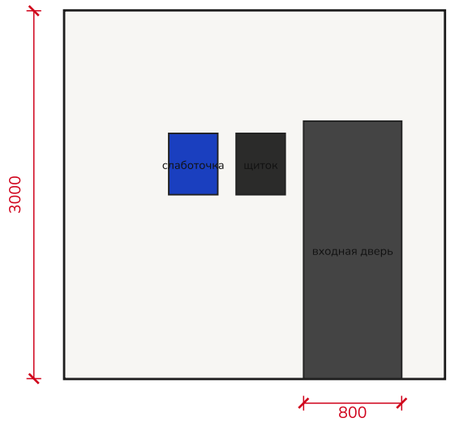

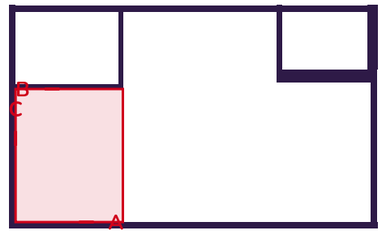

ключ-план

Стена под краску

11,0 м²

стены прихожей без шкафа и двери

Шкаф-купе: 3 створки по 600, средняя — зеркало, глубина 600, антресоль от 2400, направляющая к закладному брусу. Обувница подвесная 800×300, h 150–950, зеркало над ней 700×1000.

Щиток 24 модуля h=1750 и слаботочный щиток — на входной стене за дверью; домофон h=1500; выключатели прихожей и термостаты h=900.


ПРИМЕЧАНИЯ:

1. За отметку 0.000 принят уровень чистового пола.
2. Все размеры уточнить по месту перед началом работ; привязки даны по неоштукатуренным стенам.
3. Положение короба стояков и вентканала уточнить после приёмки квартиры 10.10.2026.
4. Размеры в миллиметрах, площади в м².
5. Пол прихожей — керамогранит с тёплым полом; порожек на границе с ламинатом.


Стадия	Лист	Листов	Квартира 72 · ЖК Buta Zaman · Алматы
РД	14	19	Развёртка стен: прихожая 18.10.2026 · М 1:50 · А3

Развёртка стен: гостиная


A — левая стена (x=0): ТВ-зона

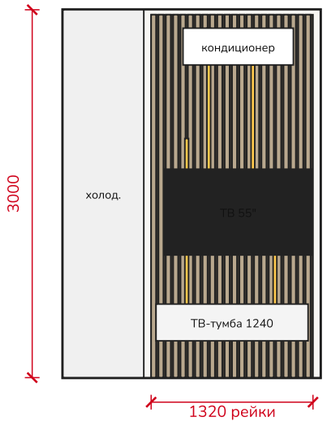


B — правая стена (x=4900)

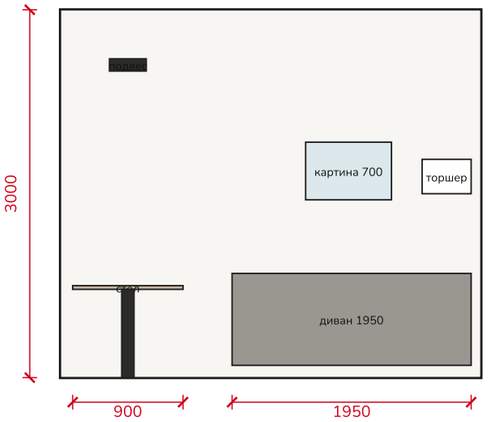

C — стеклянная перегородка (z=6140)

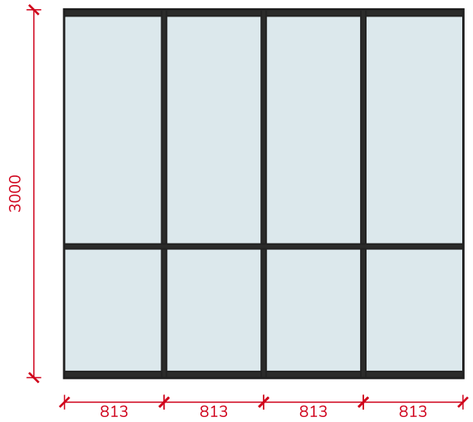

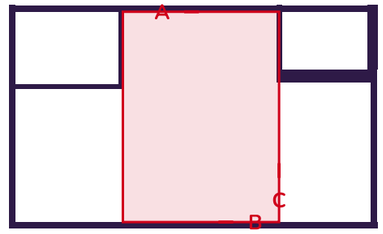

ключ-план

Стена под краску

20,5 м²

стены гостиной и кухонной зоны

ТВ-стена 1320×2960: рейки 40 мм с шагом 60 мм на тёмной подложке, 4 светящиеся полосы 3000K между рейками, вывод кабеля h=2900 за рейками.

Тумба 1240, ТВ 55", кондиционер крепить сквозь рейки в стену; розетки ×2 + интернет/ТВ h=1100, розетка у тумбы h=350.

Перегородка: 4 створки ~813 мм в чёрном алюминиевом профиле, высота до потолка, верхняя направляющая к закладному брусу; створки собираются у правой стены.


ПРИМЕЧАНИЯ:

1. За отметку 0.000 принят уровень чистового пола.
2. Все размеры уточнить по месту перед началом работ; привязки даны по неоштукатуренным стенам.
3. Положение короба стояков и вентканала уточнить после приёмки квартиры 10.10.2026.
4. Размеры в миллиметрах, площади в м².


Стадия	Лист	Листов	Квартира 72 · ЖК Buta Zaman · Алматы
РД	15	19	Развёртка стен: гостиная 18.10.2026 · М 1:50 · А3

Развёртка стен: спальня


A — стена с окном (z=8280)

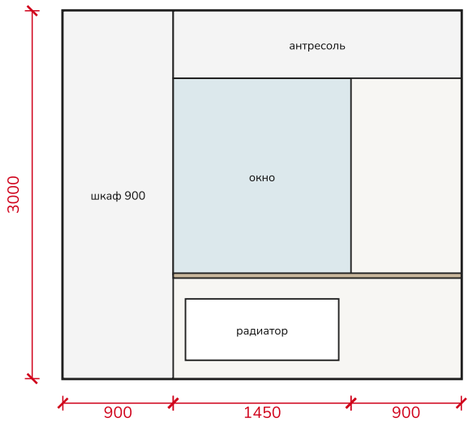


B — правая стена (x=4900)

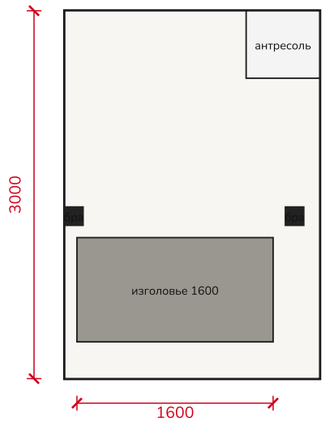

C — стена балкона (x=1650)

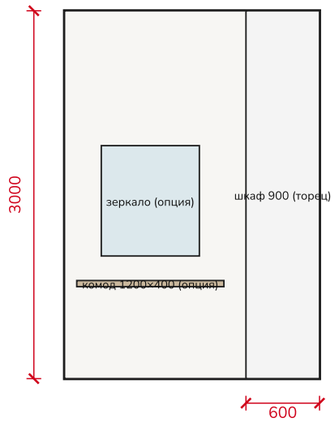

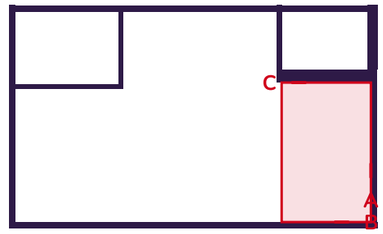

ключ-план

Стена под краску

12,5 м²

стены спальни без шкафа и окна

Шкаф-колонна 900×600×3000 слева от окна, антресоль над окном 2450–3000, подоконник-полка 300 мм, карниз штор под антресолью. Изголовье 1600×850, бра h=1300, розетки USB h=600.

Стена балкона: опционально комод 1200×400 с зеркалом (туалетный столик) — проход к кровати остаётся 800 мм.


ПРИМЕЧАНИЯ:

1. За отметку 0.000 принят уровень чистового пола.
2. Все размеры уточнить по месту перед началом работ; привязки даны по неоштукатуренным стенам.
3. Положение короба стояков и вентканала уточнить после приёмки квартиры 10.10.2026.
4. Размеры в миллиметрах, площади в м².


Стадия	Лист	Листов	Квартира 72 · ЖК Buta Zaman · Алматы
РД	16	19	Развёртка стен: спальня 18.10.2026 · M 1:50 · A3

КВАРТИРА 72


Визуализация

 


Общий вид (3D)

 


Гостиная, вид на спальню

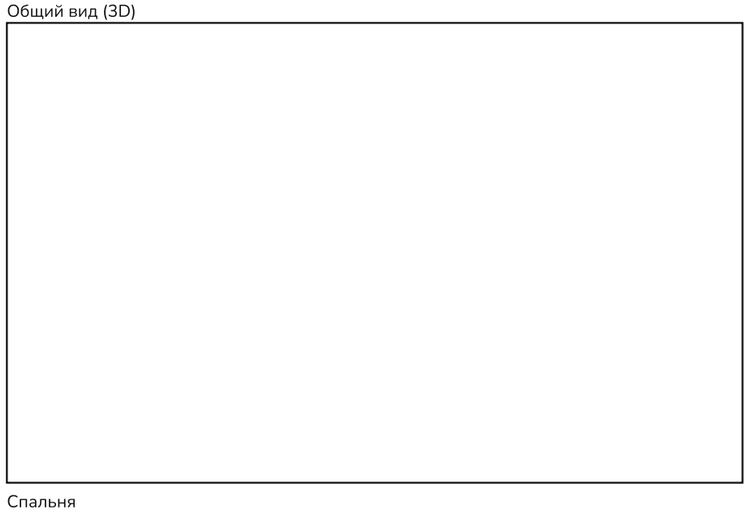

Спальня

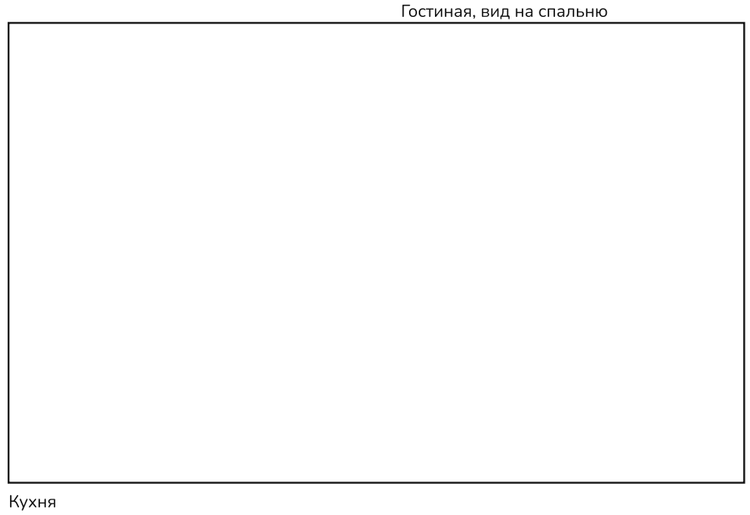

Кухня

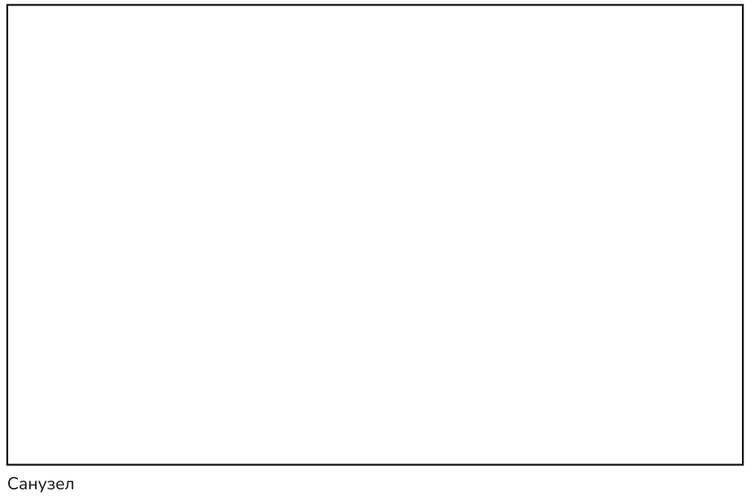

Санузел

Визуализации выполнены в Blender (Cycles) по рабочей 3D-модели. Материалы и мебель — схематичные, по палитре проекта: стены светло-серые, пол светлый дуб, фасады белые матовые, акценты чёрные.

Стадия	Лист	Листов	Квартира 72 · ЖК Buta Zaman · Алматы
РД	17	19	Визуализация 18.10.2026 · M — · A3

Ведомость материалов

Отделка помещений

№	Помещение	Пол	Стены	Потолок	Площадь
1	Прихожая	Керамогранит 600×600 + тёплый пол	Краска	Натяжной	~7,0 м²
2	Санузел	Керамогранит 600×600 + тёплый пол	Керамогранит 600×600	Натяжной влагост.	4,1 м²
3	Кухня	Ламинат 33 кл.	Краска; фартук керамогранит	Натяжной	~6,0 м²
4	Гостиная	Ламинат 33 кл.	Краска	Натяжной	~9,0 м²
5	Спальня	Ламинат 33 кл.	Краска	Натяжной	~6,5 м²
6	Балкон	Керамогранит	Краска	Натяжной / покраска	2,7 м²

Ведомость отделки

Элемент	Кол-во
Ламинат (с запасом 7%)	29 м²
Керамогранит пол	13 м²
Керамогранит стены санузла	20 м²
Фартук кухни	2,5 м²
Стены под покраску	~90 м²
Натяжной потолок	~36 м²
Плинтус	30 м
Нагревательный мат	6 м²

Ведомость электрики

Электрика	Кол-во
Розетки	16
Силовые выводы	7
Выключатели / выводы света	20
Слаботочные точки	3
Споты GX53	9
Подвес / бра	1 / 2
LED-лента	5 м
Терморегуляторы	2

Ведомость сантехники

Сантехника	Кол-во
Ванна акриловая 1700×700	1
Унитаз подвесной + инсталляция	1
Тумба с раковиной 750	1
Смесители (ванна, раковина, кухня)	3
Мойка кухонная	1
Полотенцесушитель эл.	1
Точки воды / канализации	17

Палитра

Стены: светло-серый тёплый

Потолок, фасады: молочно-белый

Пол: светлый дуб

Столешница, плитка: светлый камень

Текстиль: серо-бежевый

Рама, ручки, светильники: чёрный матовый

Встроенная мебель: шкаф-купе 1800×600×3000 (3 створки, зеркало); кухня 3,36 пог. м, верх до потолка, фасады без ручек; стеклянная раздвижная перегородка 3250×3000, 4 створки, чёрный профиль.

Техника: холодильник (колонна), варочная индукционная, вытяжка встраиваемая, микроволновка, стиральная машина, посудомойка 45 см, кондиционер, телевизор 55".

Стадия	Лист	Листов	Квартира 72 · ЖК Buta Zaman · Алматы
РД	18	19	Ведомость материалов 18.10.2026 · M — · A3

Смета

Сводная смета (цены satu.kz, Алматы, 29.09.2026; работа мастеров — ориентировочно)

Раздел	Когда	Сумма, ₸
1. Стены санузла, штукатурка, стяжка	недели 1–3	574 100
2. Сантехника черновая	недели 1–2	230 000
3. Электрика черновая	неделя 2	760 000
4. Тёплый пол	неделя 5	78 000
5. Плитка	неделя 5	444 000
6. Стены, потолок, пол	недели 6–7	977 800
7. Электрика чистовая	неделя 8	170 500
8. Сантехника чистовая	неделя 8	485 000
9. Встроенная мебель	замер — неделя 4, установка — неделя 8	1 440 000
10. Техника	к установке кухни	1 270 000
11. Мебель и текстиль	в конце	1 020 000
12. Прочее	весь ремонт	288 000
Итого		7 737 400
Запас 10 %		773 740
Всего с запасом		8 511 140

Крупнейшие позиции	Кол-во	Цена	Сумма	Разд.
Стеклянная раздвижная перегородка ~10 м² (от 6	1 шт	700 000	700 000	9
Кухонный гарнитур ~4 пог. м, эконом (от 40–80	1 шт	450 000	450 000	9
Работа электрика: ~50 точек, штробы, щиток, чи	1 усл	350 000	350 000	3
Диван	1 шт	300 000	300 000	11
Кондиционер с монтажом и трассой	1 шт	280 000	280 000	10
Шпаклёвка и покраска стен (работа) — уточнить	90 м²	3 000	270 000	6
Шкаф-купе 1,8 × 0,6 × 3 м (от 190 000 ₸)	1 шт	250 000	250 000	9
Холодильник	1 шт	250 000	250 000	10
Ламинат 33 класс (Tarkett / Navigator)	28 м²	8 300	232 400	6
Укладка плитки (работа) — уточнить	31 м²	7 000	217 000	5
Штукатурка стен машинная (работа)	100 м²	2 000	200 000	1
Посудомоечная машина 45 см встраиваемая	1 шт	200 000	200 000	10
Стиральная машина	1 шт	180 000	180 000	10
Керамогранит 60×60 / 60×120: санузел стены и п	34 м²	5 000	170 000	5
Натяжной потолок матовый с монтажом — уточнить	36 м²	4 500	162 000	6
Телевизор	1 шт	150 000	150 000	10
Кровать 160×200	1 шт	150 000	150 000	11
Матрас 160×200	1 шт	150 000	150 000	11
Кабель ВВГнг-LS 3×2,5 (розетки, техника, тёплы	200 м	720	144 000	3
Тумба с раковиной подвесная 60 см	1 шт	120 000	120 000	8
Варочная панель индукционная	1 шт	120 000	120 000	10
Стяжка пола полусухая (материал + работа)	34 м²	3 500	119 000	1
Стол + 2 стула	1 компл	100 000	100 000	11
Вывоз мусора, доставка, подъём материалов	1 усл	100 000	100 000	12

Полная смета по всем позициям (с редактированием цен) — на сайте проекта: leylagxx.github.io/kvartira72

Работа по сантехнике не учтена (выполняется своими силами). Позиции, которые выгодно заказать из Китая, отмечены на сайте — экономия ~260 тыс. ₸.