

ДИЗАЙН-ПРОЕКТ

Квартира № 72 · ЖК Buta Zaman · г. Алматы

Студия 37,4 м² (1 комн., тип 1, этаж 2–7) · высота потолка 3,0 м

Стиль: минимализм · спальня за раздвижной стеклянной перегородкой · шкаф-купе в прихожей · ванна · тёплый пол в прихожей и санузле


Состав альбома

- | | |
|--------------------------------------|--|
| 2. Обмерный план | 9. Развёртка стен: кухня |
| 3. Планировочное решение | 10. Развёртка стен: санузел |
| 4. План осветительных приборов | 11. Развёртки: прихожая, гостиная, спальня |
| 5. Сводный план электрических цепей | 12. Визуализация |
| 6. План потолка | 13. Ведомость материалов |
| 7. План сантехнического оборудования | 14. Смета |
| 8. План тёплых полов | |

Исполнитель: Claude (ИИ-ассистент) по заданию владельца · 01.10.2026 · Не является официальной проектной документацией: нормы и сечения проверяют исполнители работ.

Квартира 72 · ЖК Buta Zaman, Алматы · Дизайн-проект студии 37,4 м²	Лист	Листов
Титульный лист Стадия: рабочие чертежи · Дата: 01.10.2026 · Масштаб — · Формат А3	1	14

Обмерный план

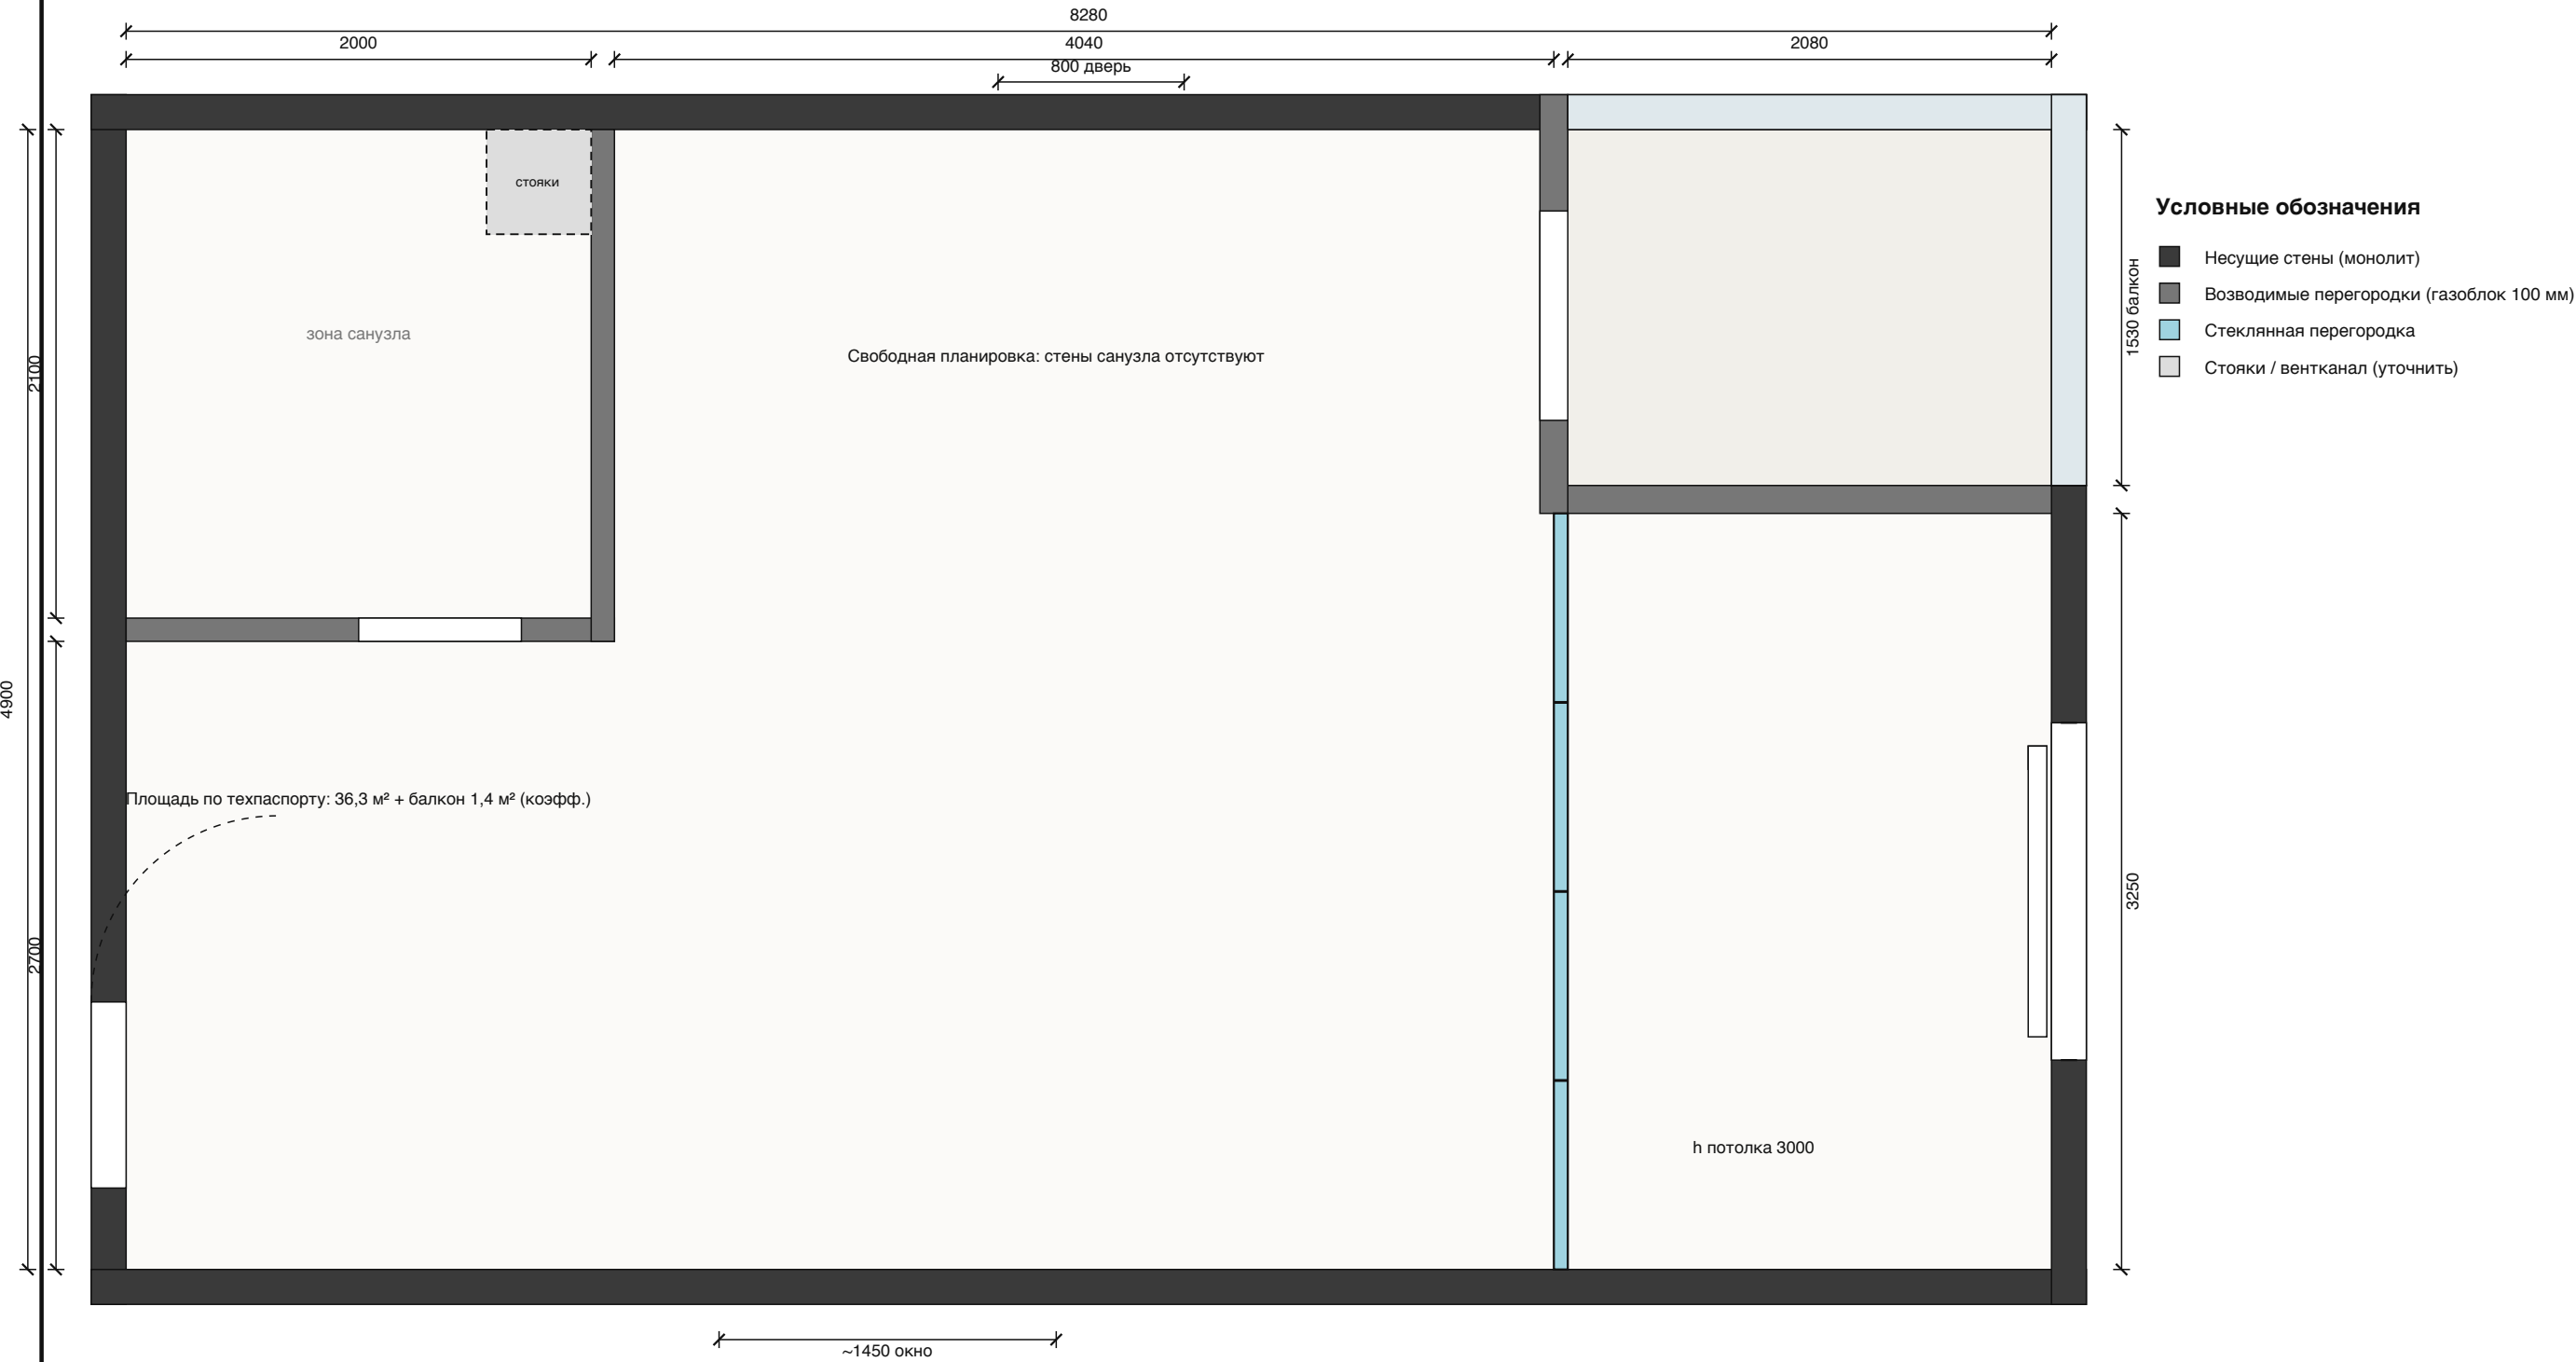


ПРИМЕЧАНИЯ

- 1. За отметку 0.000 принят уровень чистового пола.
- 2. Все размеры уточнить по месту перед началом работ; привязки даны по неоштукатуренным стенам.
- 3. Положение стояков, вентканала и размер санузла уточнить после приёмки квартиры 10.10.2026.
- 4. Размеры в миллиметрах, площади в м².
- 5. Размер окна и балконной двери замерить по факту.
- 6. Входная дверь открывается наружу.

Квартира 72 · ЖК Buta Zaman, Алматы · Дизайн-проект студии 37,4 м²	ЛистЛистов	
Обмерный план	2	14
Стадия: рабочие чертежи · Дата: 01.10.2026 · Масштаб 1:30 · Формат A3		

Планировочное решение

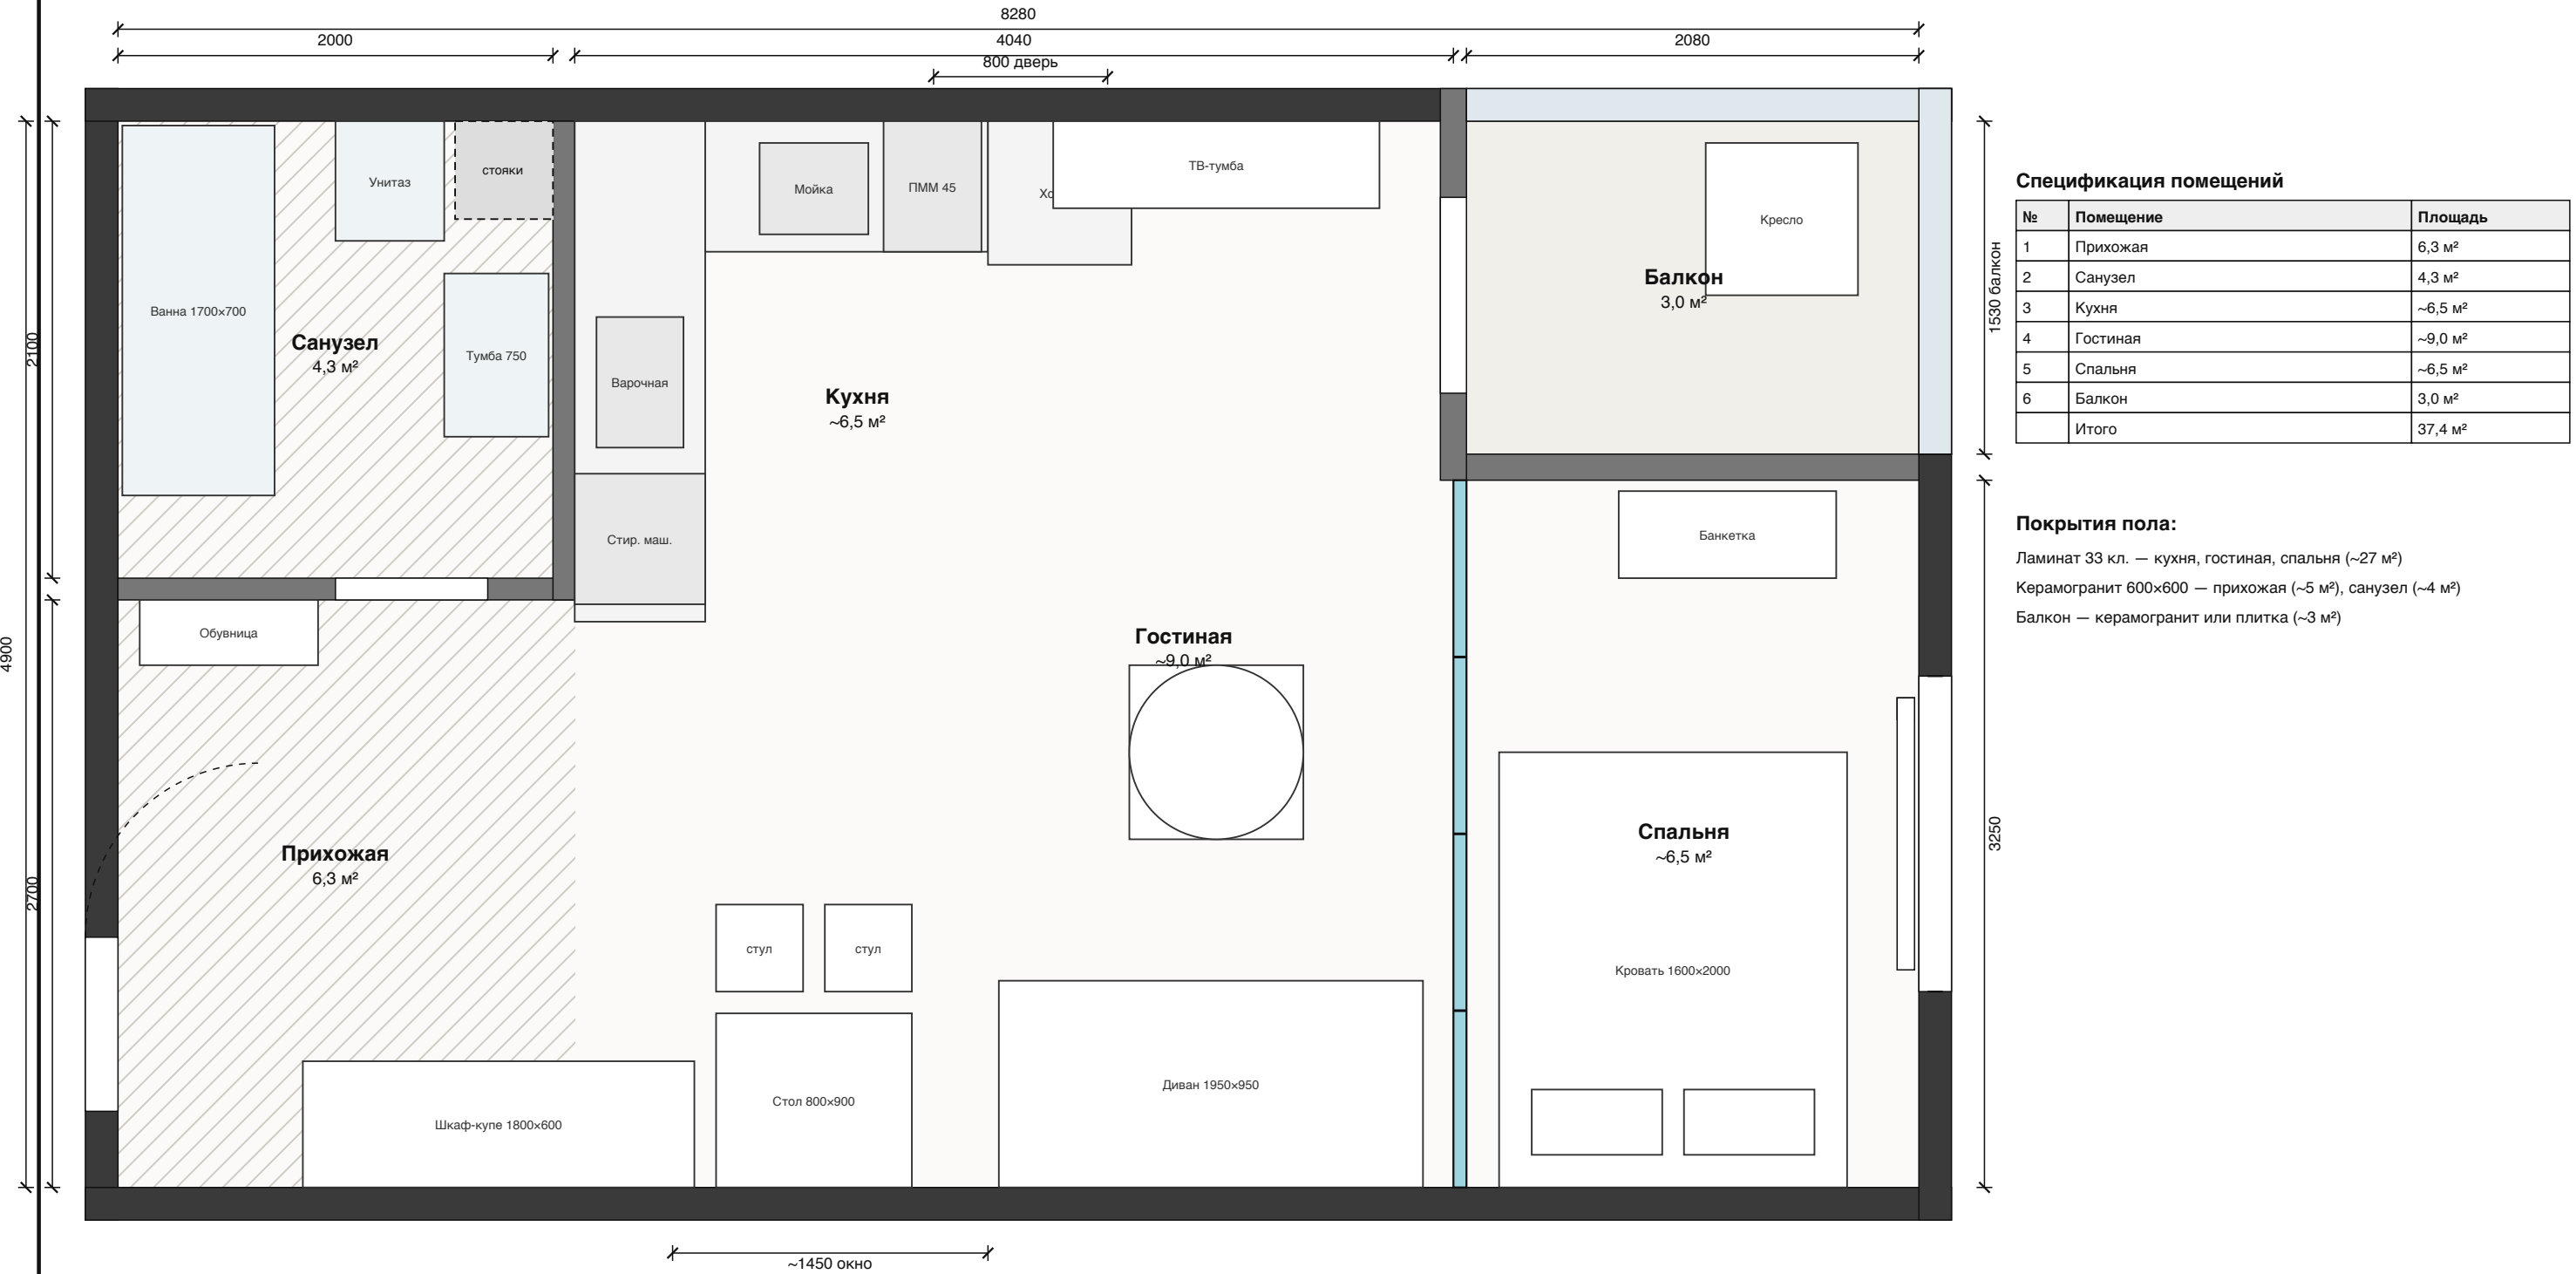


ПРИМЕЧАНИЯ

- 1. За отметку 0.000 принят уровень чистового пола.
- 2. Все размеры уточнить по месту перед началом работ; привязки даны по неоштукатуренным стенам.
- 3. Положение стояков, вентканала и размер санузла уточнить после приёмки квартиры 10.10.2026.
- 4. Размеры в миллиметрах, площади в м².
- 5. Перегородка спальни: 4 раздвижные стеклянные створки в чёрном алюминиевом профиле, высота до потолка.

Квартира 72 · ЖК Buta Zaman, Алматы · Дизайн-проект студии 37,4 м²	ЛистЛистов	
Планировочное решение	3	14
Стадия: рабочие чертежи · Дата: 01.10.2026 · Масштаб 1:30 · Формат А3		

План осветительных приборов

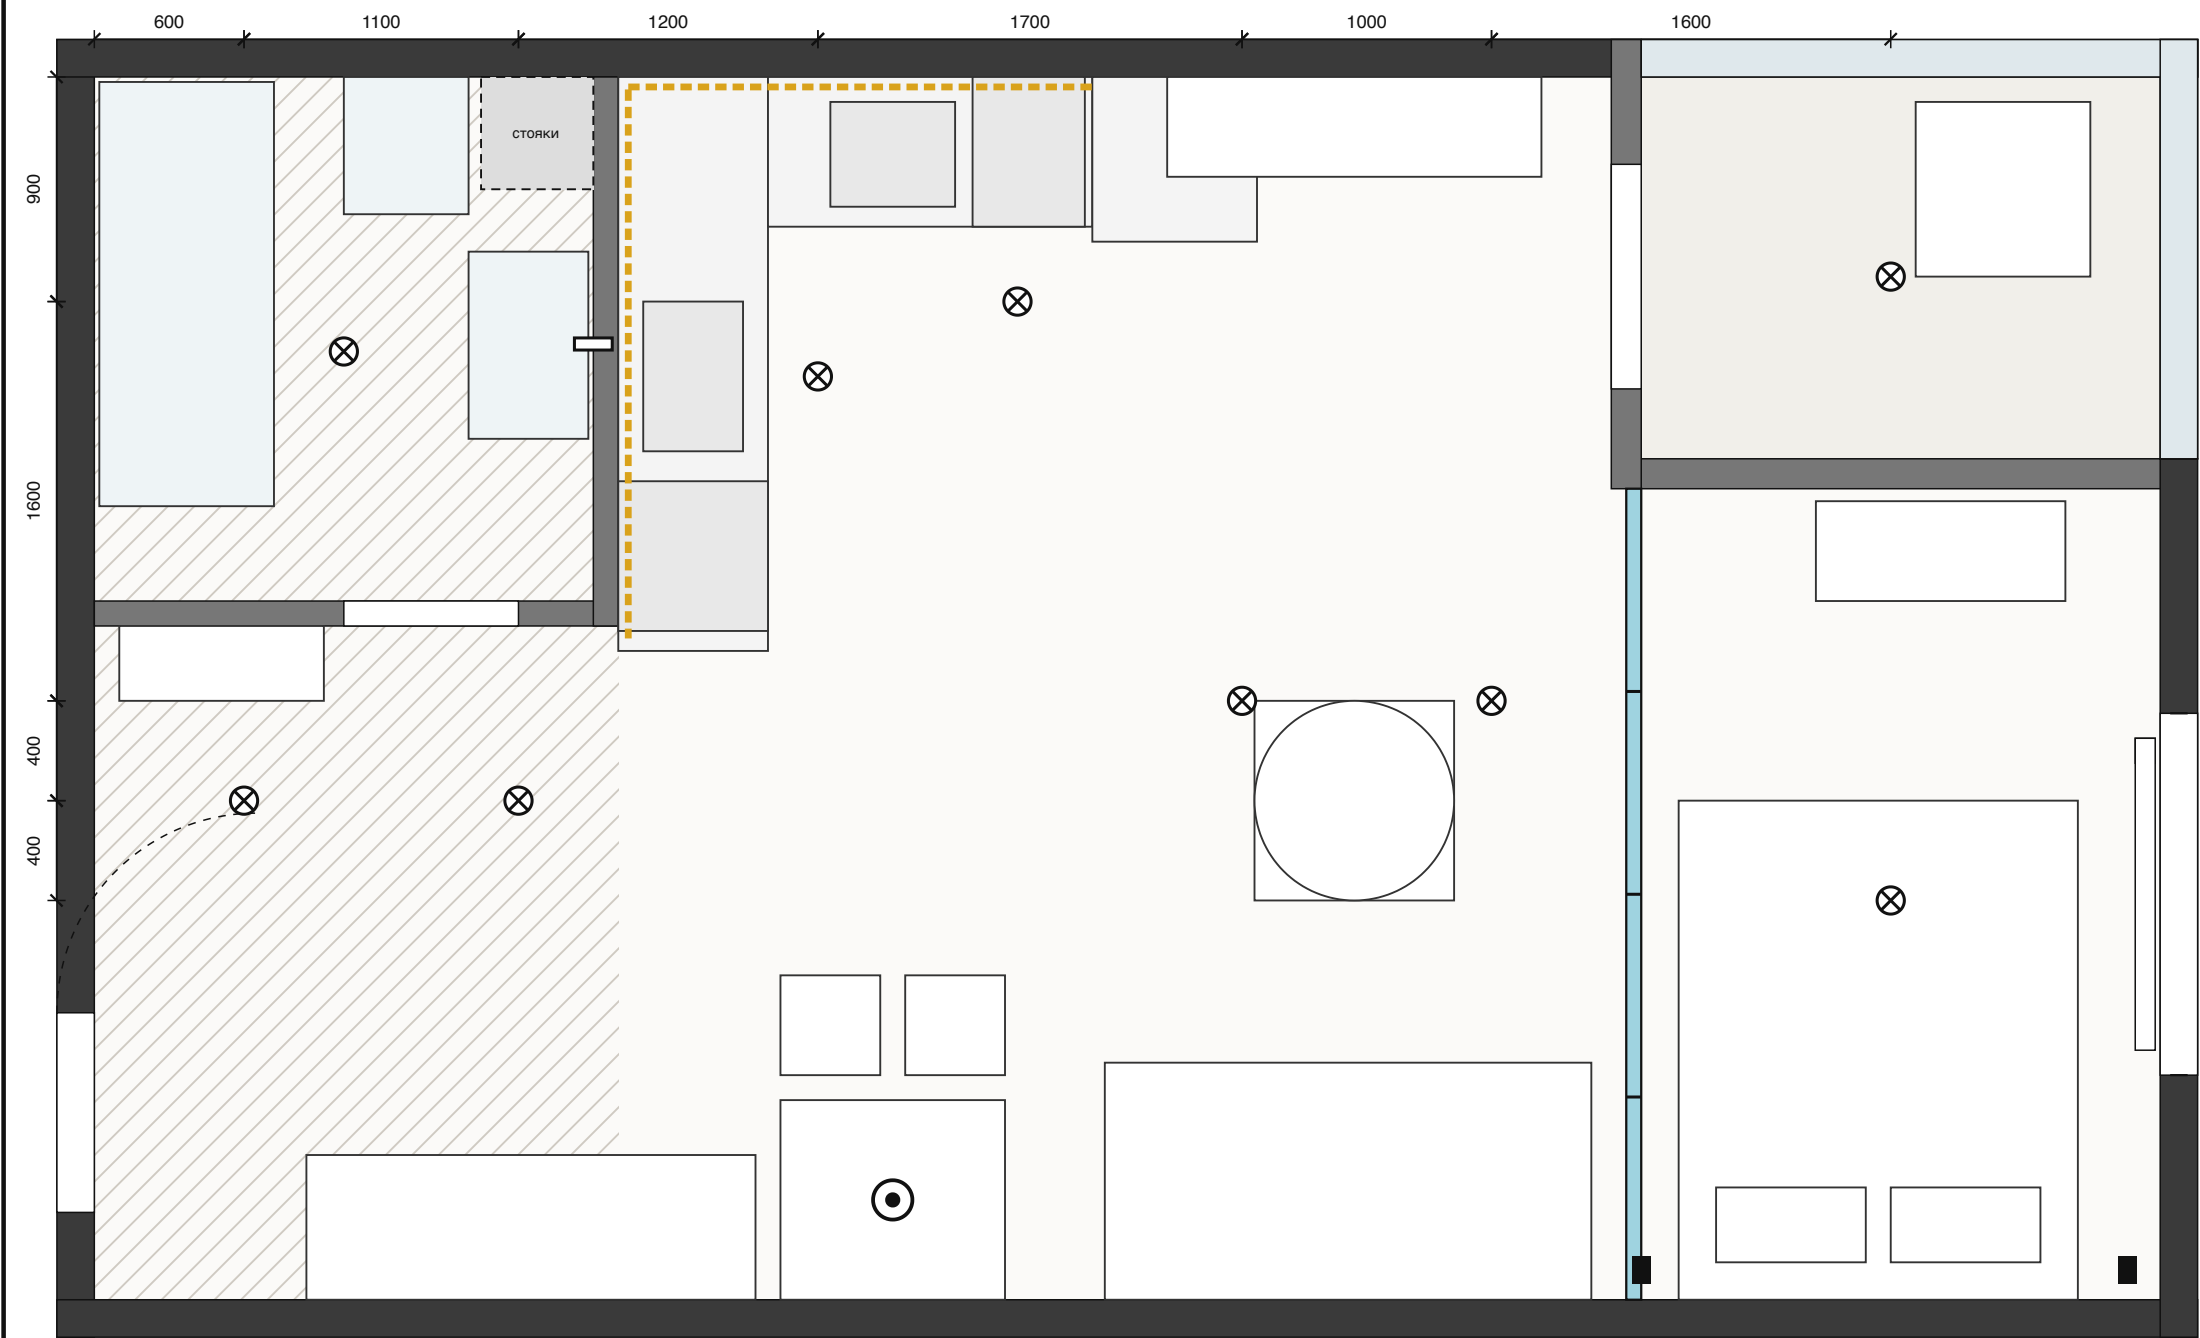

Условные обозначения

- ⊗ Светильник накладной / встроенный, GX53
- ⊙ Подвесной светильник над столом
- Бра, h=1300
- - - Светодиодная лента (подсветка кухни)
- ▭ Зеркало с подсветкой

Ведомость осветительных приборов

Наименование	Шт.
Светильник накладной GX53	9
Подвес над столом	1
Бра	2
LED-лента, м	5
Зеркало с подсветкой	1
Вентилятор вытяжной	1

ПРИМЕЧАНИЯ

1. За отметку 0.000 принят уровень чистового пола.
2. Все размеры уточнить по месту перед началом работ; привязки даны по неоштукатуренным стенам.
3. Положение стояков, вентканала и размер санузла уточнить после приёмки квартиры 10.10.2026.
4. Размеры в миллиметрах, площади в м².
5. Привязки даны к центру светильника.
6. Слоты — на отдельных группах: прихожая+санузел, кухня, гостиная, спальня, балкон.

Квартира 72 · ЖК Buta Zaman, Алматы · Дизайн-проект студии 37,4 м²


Лист

Листов

План осветительных приборов

Стадия: рабочие чертежи · Дата: 01.10.2026 · Масштаб 1:30 · Формат А3

Сводный план электрических цепей

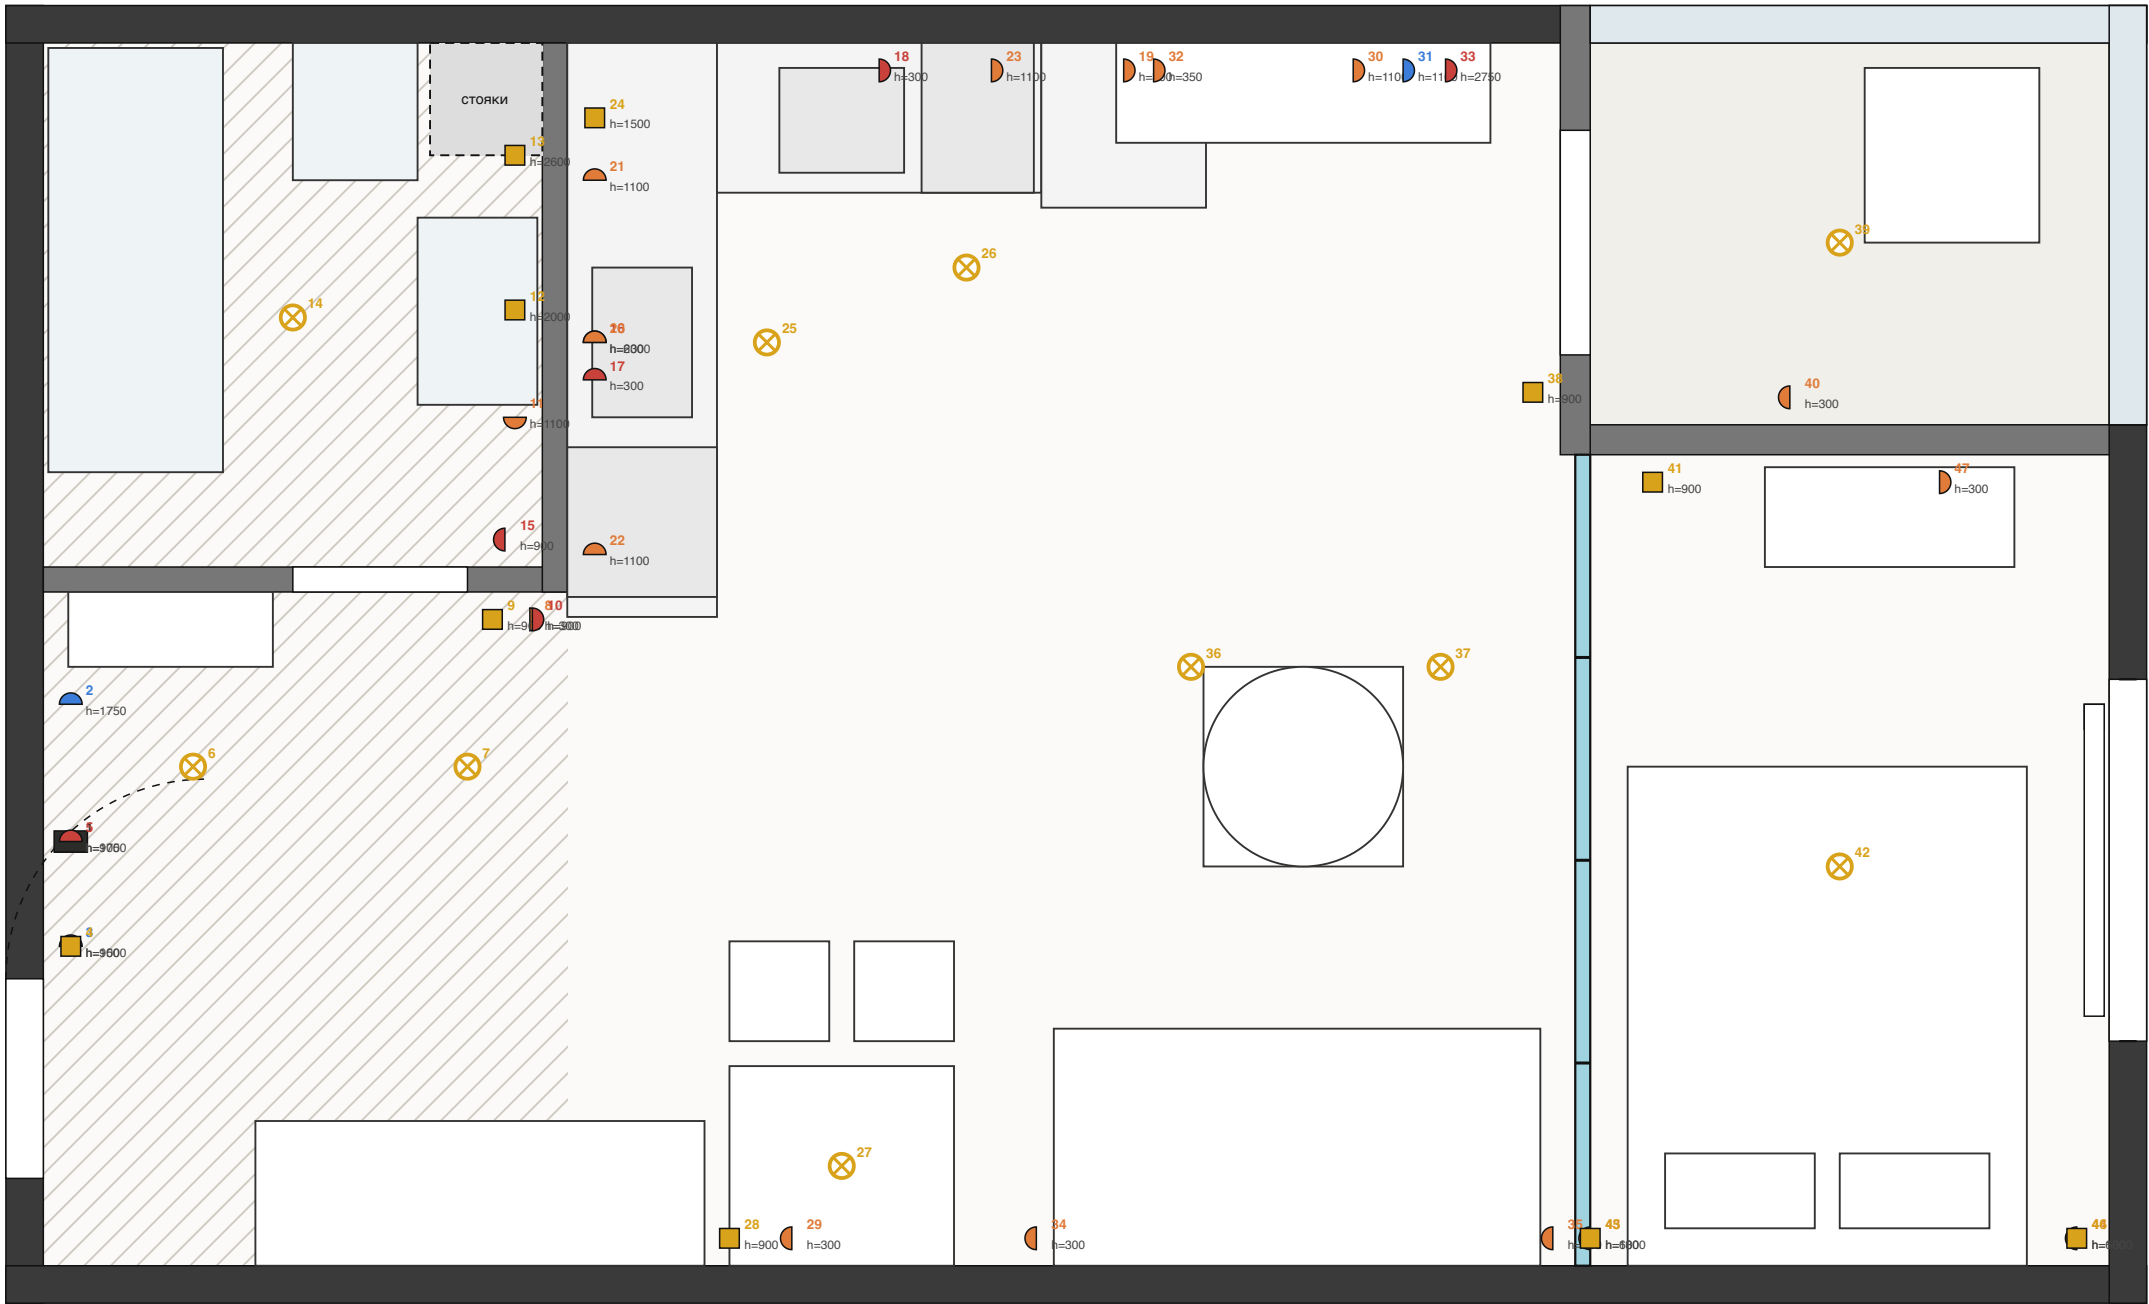

Условные обозначения

- Розетка (h=300, если не указано иное)
- Отдельная линия: техника, тёплый пол, кондиционер
- Интернет / ТВ / домофон
- Выключатель (h=900) / вывод под светильник
- Электрощиток h=1750

Ведомость электроточек

Наименование	Шт.
Розетки, в т.ч. с USB и IP44	16
Выводы силовых линий (техника, тёплый пол, бойлер/полотенцесуш.)	7
Выключатели и выводы света	20
Слаботочные точки	3
Щиток	1
Всего точек	47

ПРИМЕЧАНИЯ

- За отметку 0.000 принят уровень чистового пола.
- Все размеры уточнить по месту перед началом работ; привязки даны по неоштукатуренным стенам.
- Положение стояков, вентканала и размер санузла уточнить после приёмки квартиры 10.10.2026.
- Размеры в миллиметрах, площади в м².
- Высоты — до центра розетки/выключателя. Номера точек — см. таблицу на сайте и в приложении.
- Отдельные автоматы: плита 32А, стиральная, посудомоечная, кондиционер, каждый тёплый пол. УЗО/дифавтоматы на все розеточные группы.
- Кабели — по потолку в гофре, спуски вертикально. Трасса кондиционера — до штукатурки.

Квартира 72 · ЖК Buta Zaman, Алматы · Дизайн-проект студии 37,4 м²

Лист

Листов


Сводный план электрических цепей

Стадия: рабочие чертежи · Дата: 01.10.2026 · Масштаб 1:30 · Формат А3

5

14

План потолка

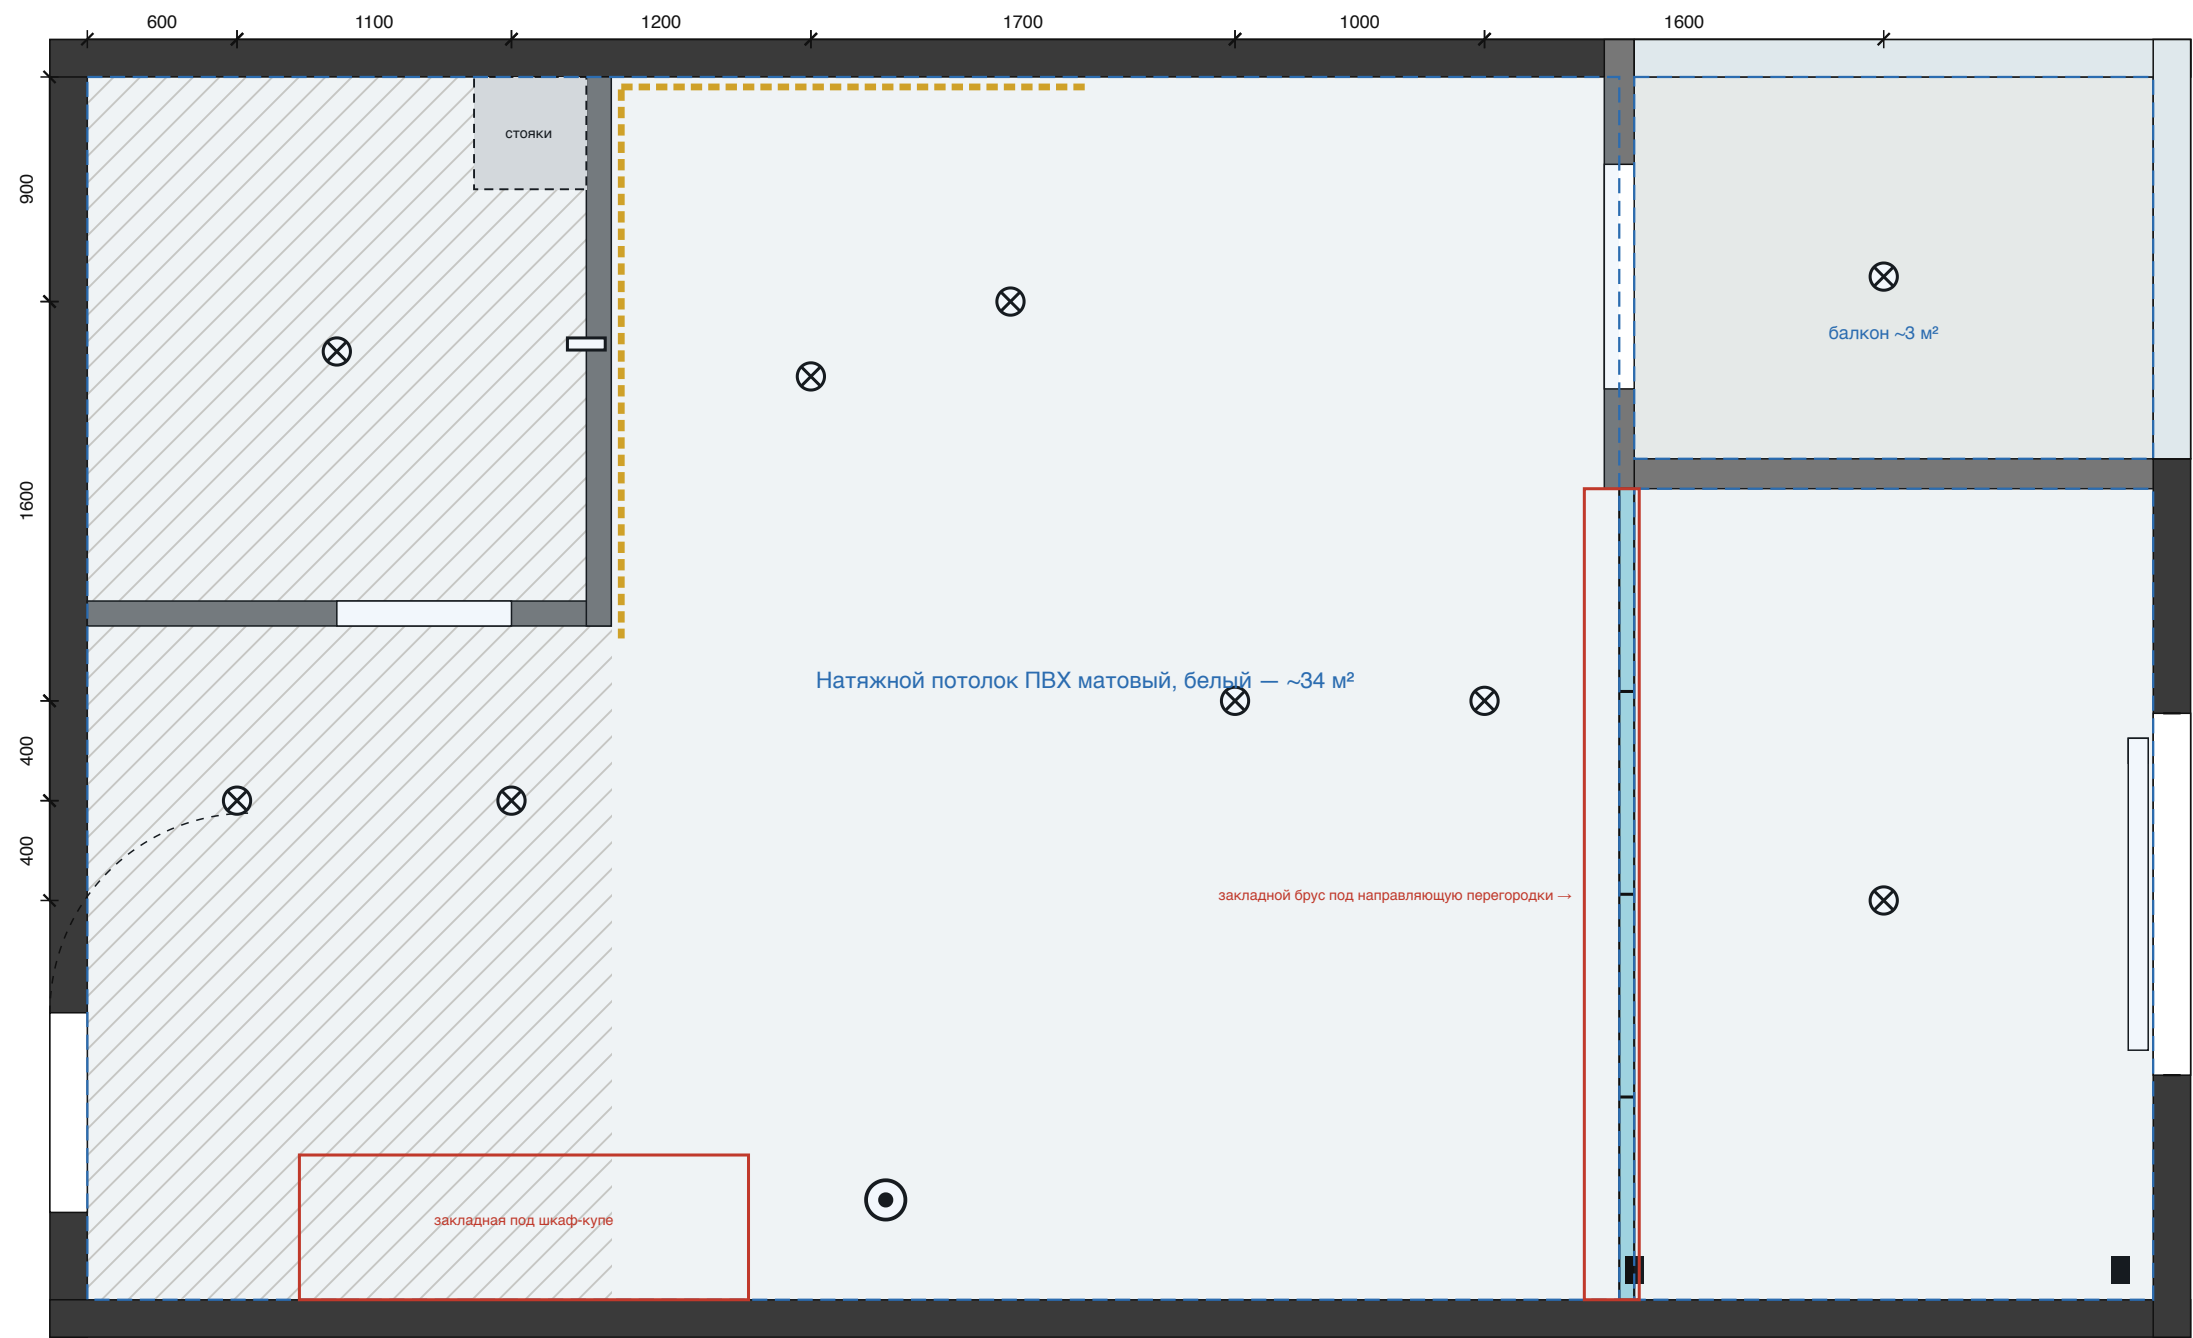

Условные обозначения

- ⊗ Спот накладной GX53, 9 шт.
- Граница натяжного потолка
- Закладные (брус) до монтажа потолка


Высота чистого потолка: 3000 – 40 = ~2960 мм
Перегородка и шкаф-купе крепятся к закладным, не к полотну.

ПРИМЕЧАНИЯ

1. За отметку 0.000 принят уровень чистового пола.
2. Все размеры уточнить по месту перед началом работ; привязки даны по неоштукатуренным стенам.
3. Положение стояков, вентканала и размер санузла уточнить после приёмки квартиры 10.10.2026.
4. Размеры в миллиметрах, площади в м².
5. Монтаж потолка — после покраски стен и до ламината; трасса кондиционера и кабели спотов — до потолка.

Квартира 72 · ЖК Bura Zaman, Алматы · Дизайн-проект студии 37,4 м²	ЛистЛистов	
План потолка	6	14
Стадия: рабочие чертежи · Дата: 01.10.2026 · Масштаб 1:30 · Формат А3		

План сантехнического оборудования

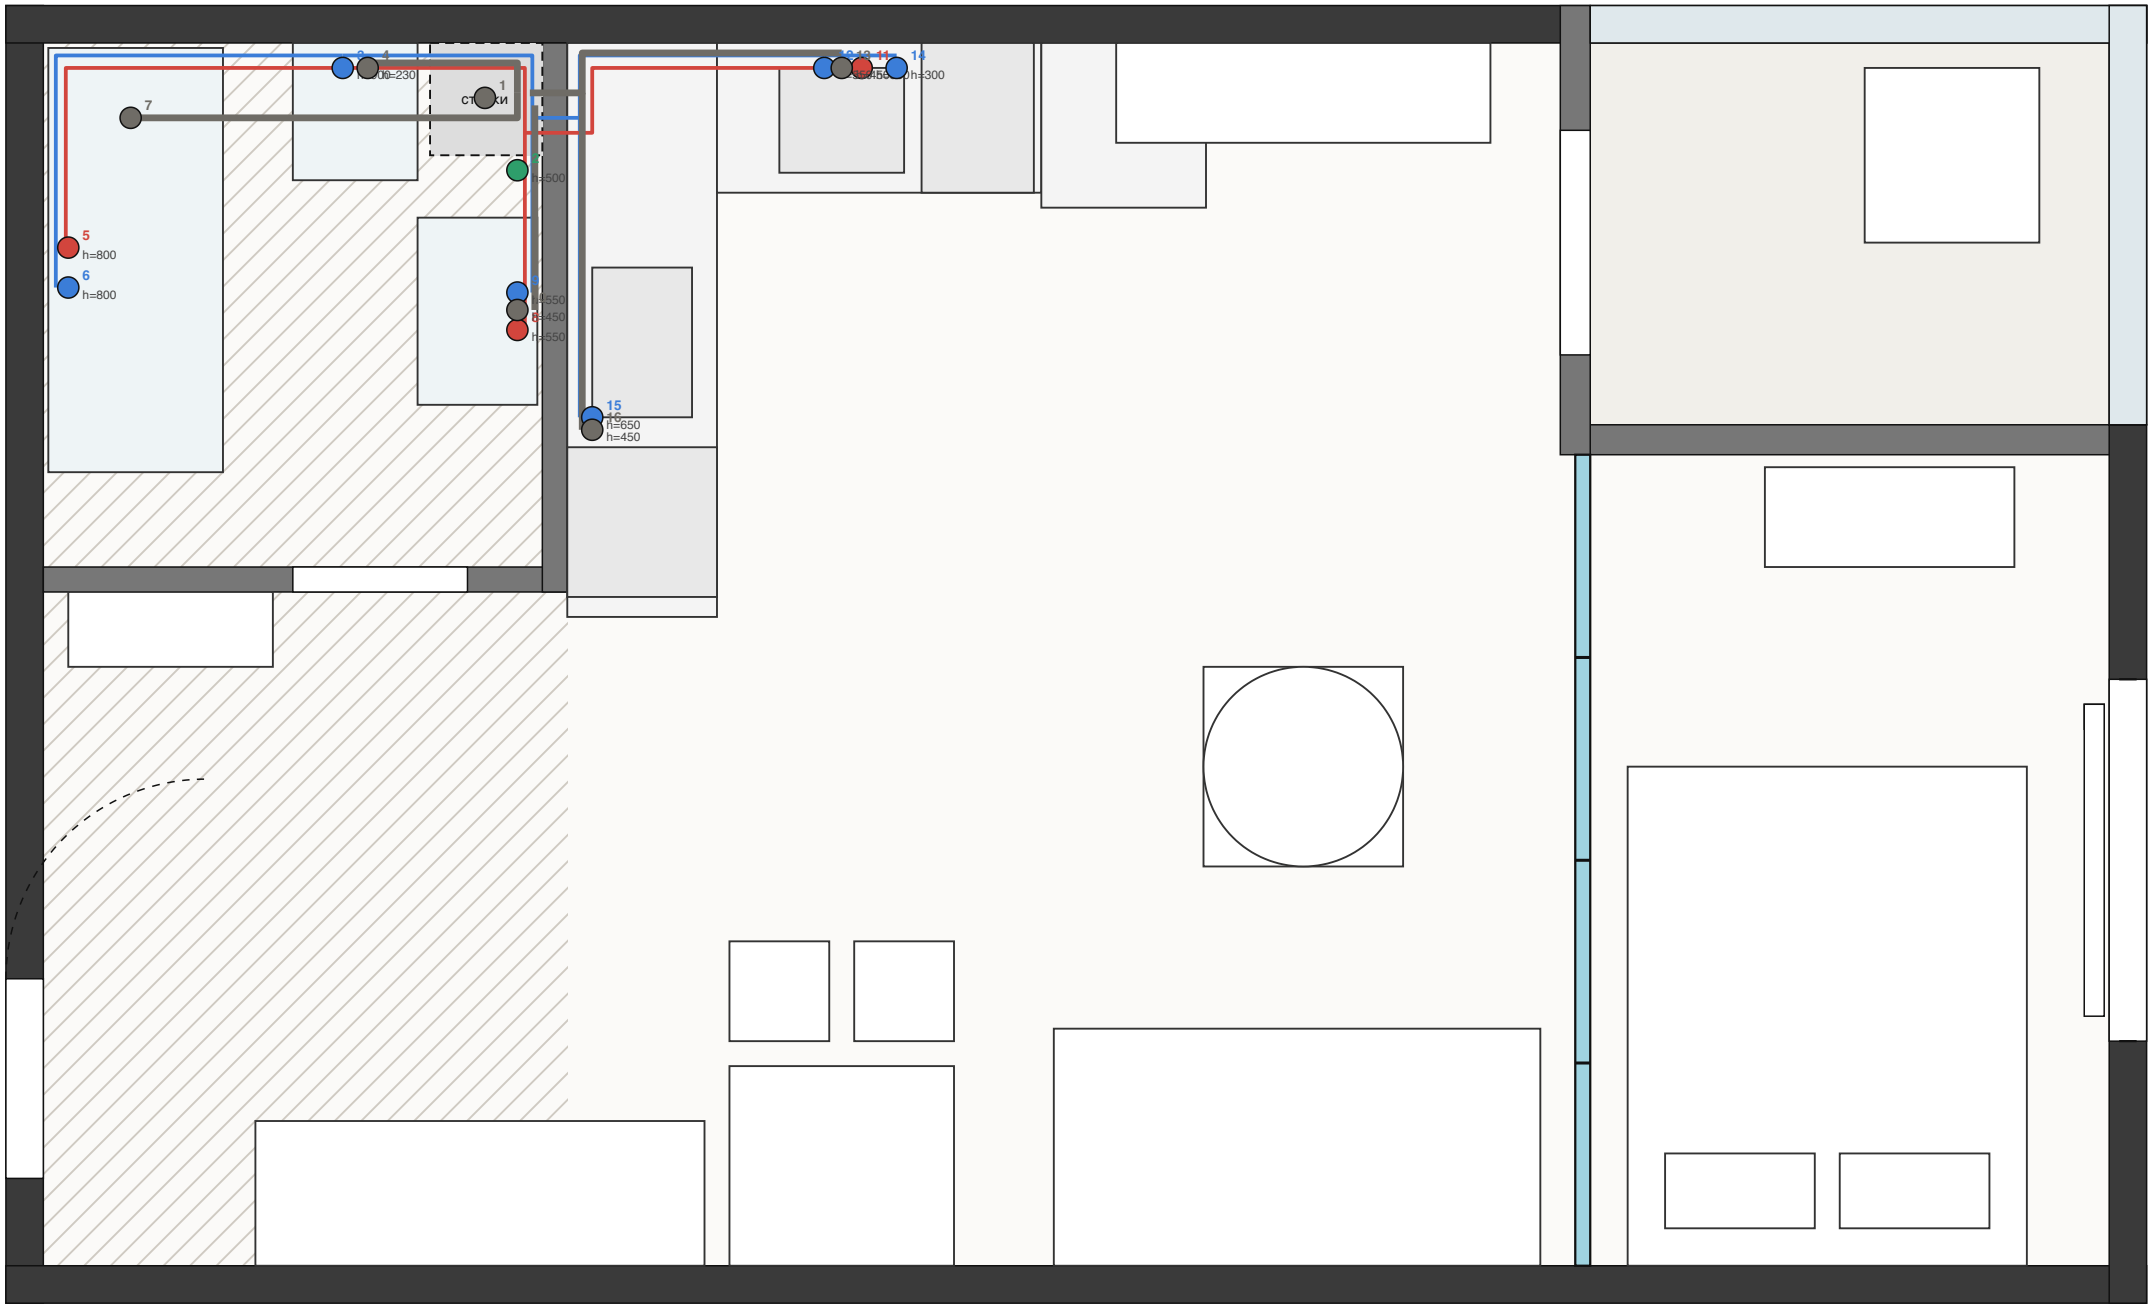

Условные обозначения

- Холодная вода
- Горячая вода
- Канализация Ø50 / Ø110
- Краны, фильтры, счётчики
- Точка вывода (номер — см. таблицу)

Ведомость точек

№	Точка	h, мм
1	Стояки воды и канализации — положение уточнить п	—
2	Краны, счётчики, фильтры	500
3	Унитаз: вода в установку	900
4	Унитаз: канализация Ø110	230
5	Ванна: смеситель, горячая	800
6	Ванна: смеситель, холодная	800
7	Ванна: слив Ø50 у торца	в полу
8	Раковина: горячая	550
9	Раковина: холодная	550
10	Раковина: слив Ø50	450
11	Мойка: горячая	550
12	Мойка: холодная	550
13	Мойка: слив Ø50	450
14	Посудомойка: кран на холодной, слив в сифон мойк	300
15	Стиральная машина: кран холодной воды	650
16	Стиральная машина: слив Ø50 с сифоном	450

ПРИМЕЧАНИЯ

- За отметку 0.000 принят уровень чистового пола.
- Все размеры уточнить по месту перед началом работ; привязки даны по неоштукатуренным стенам.
- Положение стояков, вентканала и размер санузла уточнить после приёмки квартиры 10.10.2026.
- Размеры в миллиметрах, площади в м².
- Горячая — слева, холодная — справа. Уклон канализации 2–3 см/м к стояку.
- Опрессовка труб до штукатурки. Стиральная и посудомоечная — через краны и сифоны с обратным клапаном.
- Ванна 1700×700 (при тесном стояке — 1500–1600). Унитаз подвесной на инсталляции.

Квартира 72 · ЖК Buta Zaman, Алматы · Дизайн-проект студии 37,4 м²

Лист

Листов


План сантехнического оборудования

Стадия: рабочие чертежи · Дата: 01.10.2026 · Масштаб 1:30 · Формат А3

7

14

План тёплых полов

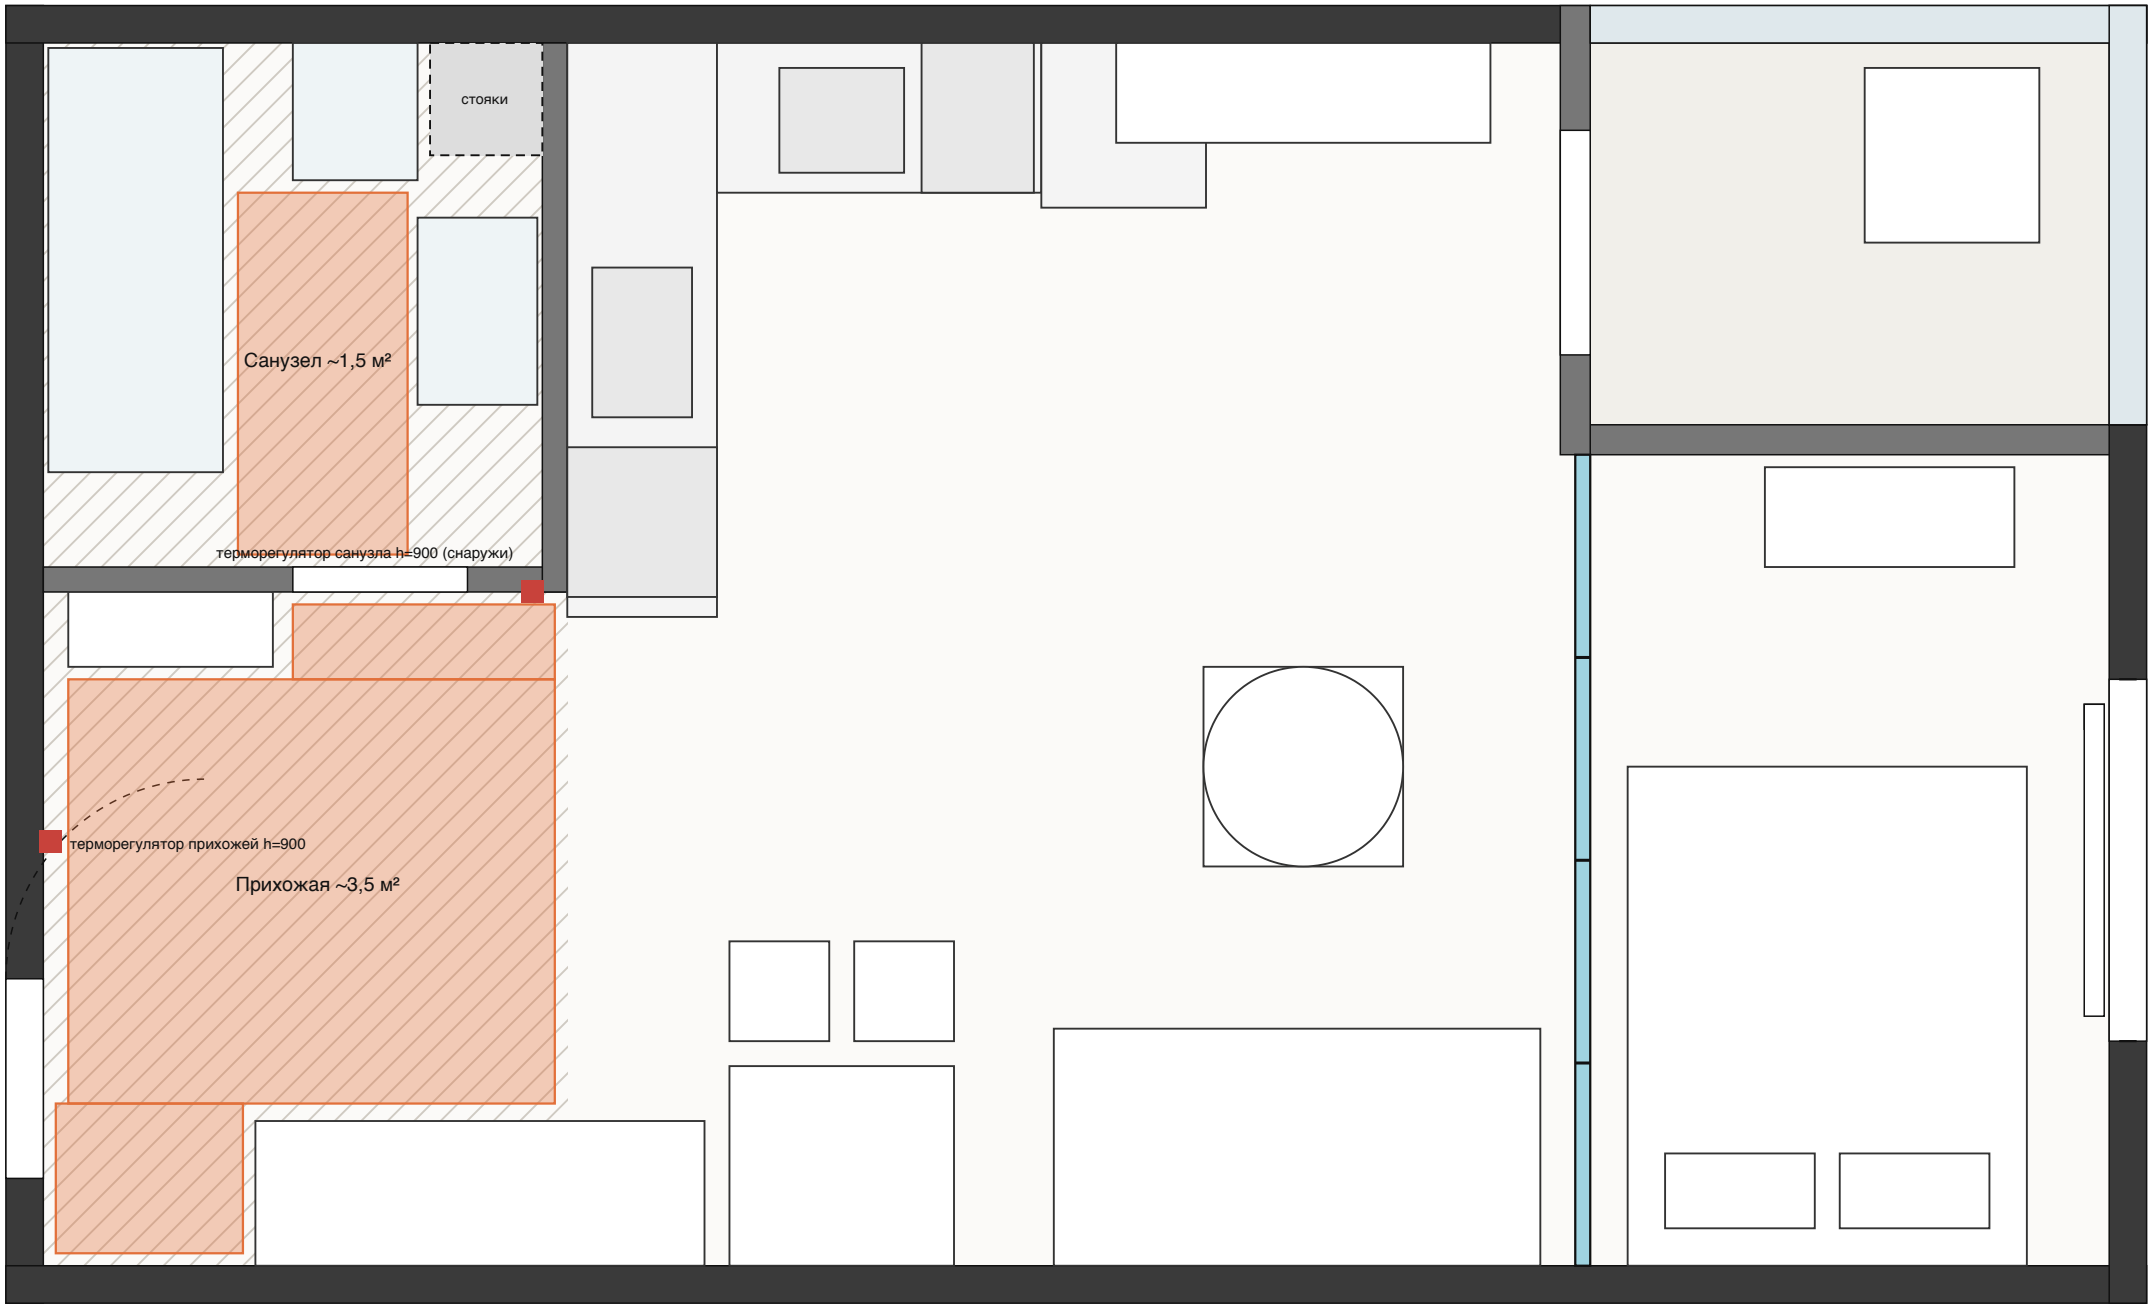

Условные обозначения

- Нагревательный мат 150 Вт/м² под плитку
- Терморегулятор с датчиком пола


Общая площадь матов: ~5 м² (прихожая 3,5 + санузел 1,5)
Мощность: ~750 Вт, две отдельные линии 3×2,5 от щитка.
Мат не кладут под шкаф, обувницу, ванну, унитаз и тумбу.

ПРИМЕЧАНИЯ

- За отметку 0.000 принят уровень чистового пола.
- Все размеры уточнить по месту перед началом работ; привязки даны по неоштукатуренным стенам.
- Положение стояков, вентканала и размер санузла уточнить после приёмки квартиры 10.10.2026.
- Размеры в миллиметрах, площади в м².
- Датчик пола — в гофре между витками мата. Проверить сопротивление мата до и после укладки плитки.
- Укладка: гидроизоляция → мат в слой клея → плитка. Включать не раньше чем через 28 дней после укладки.

Квартира 72 · ЖК Buta Zaman, Алматы · Дизайн-проект студии 37,4 м²	ЛистЛистов	
План тёплых полов	8	14
Стадия: рабочие чертежи · Дата: 01.10.2026 · Масштаб 1:30 · Формат А3		

Развёртка стен: кухня

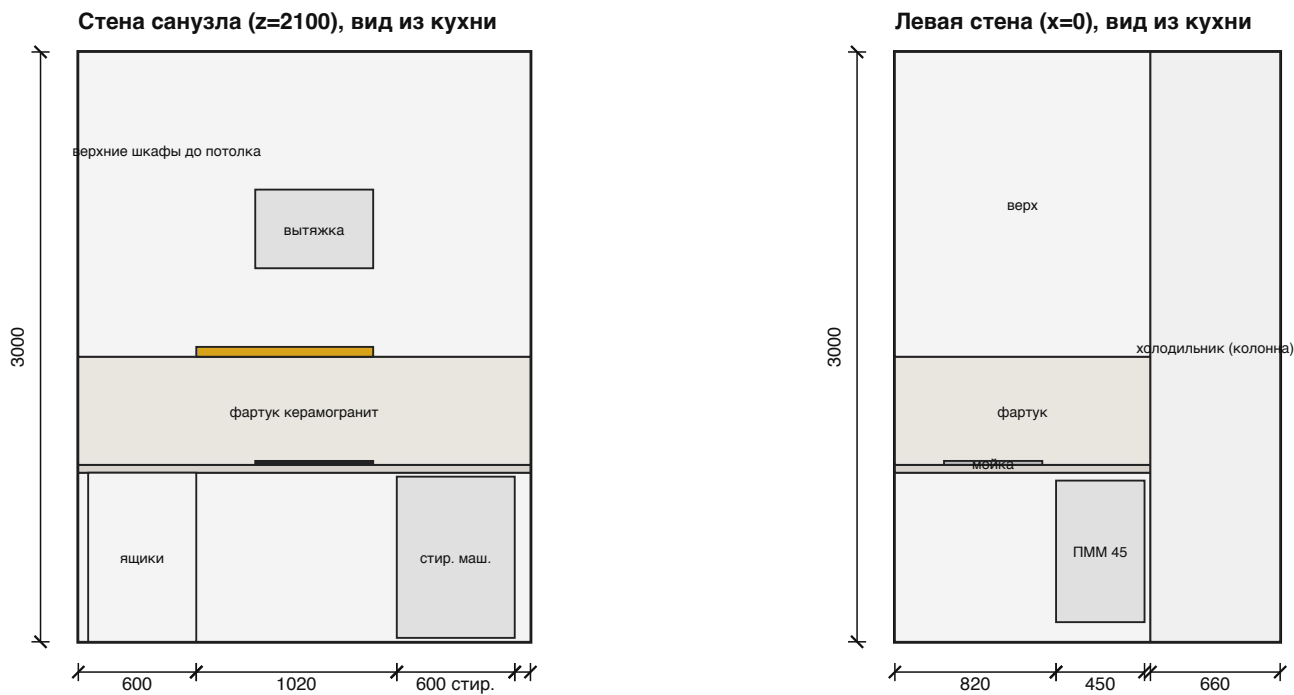

Отметки (от чистого пола):

столешница 900 · фартук 900–1450 · верхние шкафы 1450–3000 · розетки над столешницей h=1100 · LED-подсветка под верхними шкафами

Варочная панель — силовая розетка h=300 за соседним шкафом · стиральная и посудомоечная — розетки h=300 за соседними шкафами · вытяжка — розетка h=2300 внутри шкафа

Фасады: белый матовый, без ручек (push-to-open или интегрированная ручка). Столешница 38 мм, светлый камень/бетон. Фартук — керамогранит 600×1200 в тон столешницы.


Длина кухни: 2,3 + 1,96 = 4,26 пог. м (включая колонну холодильника).

ПРИМЕЧАНИЯ

1. За отметку 0.000 принят уровень чистового пола.
2. Все размеры уточнить по месту перед началом работ; привязки даны по неоштукатуренным стенам.
3. Положение стояков, вентканала и размер санузла уточнить после приёмки квартиры 10.10.2026.
4. Размеры в миллиметрах, площади в м².
5. Замер кухни — после штукатурки, установка — после пола и потолка.

Квартира 72 · ЖК Buta Zaman, Алматы · Дизайн-проект студии 37,4 м²	ЛистЛистов	
Развёртка стен: кухня	9	14
Стадия: рабочие чертежи · Дата: 01.10.2026 · Масштаб 1:38 · Формат A3		

Развѐртка стен: санузел

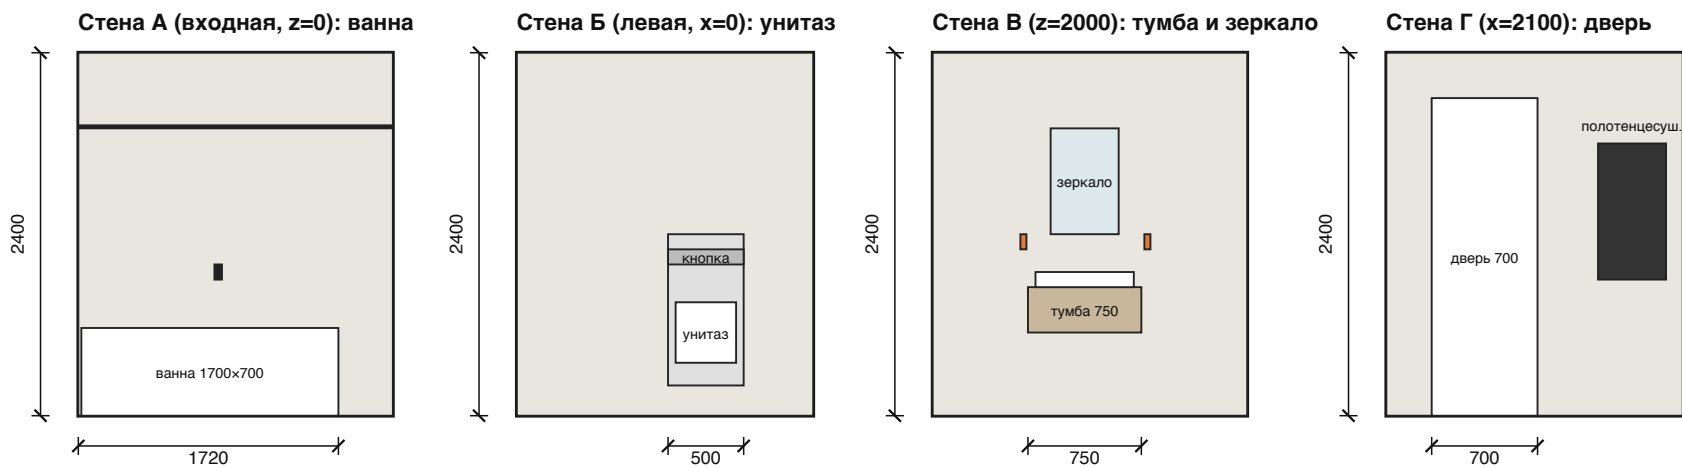

Санузел 2100 x 2000, h 2400 (натяжной потолок). Плитка керамогранит 600x600, стены и пол — одна коллекция. Швы 2 мм, затирка в тон.

Площади: стены ~19 м² (за вычетом двери), пол 4,2 м². Запас плитки 10%.

Отметки: смеситель ванны 900 · штанга шторки 1900 · верх унитаза 400 · тумба 850 · зеркало 1200–1900 · розетка у зеркала 1100 (IP44) · вентилятор 2300 в вентканал.


Гидроизоляция обмазочная: пол + стены на 300 мм, зона ванны — на 1800 мм. Тёплый пол — свободная зона 1,5 м².

ПРИМЕЧАНИЯ

- 1. За отметку 0.000 принят уровень чистового пола.
- 2. Все размеры уточнить по месту перед началом работ; привязки даны по неоштукатуренным стенам.
- 3. Положение стояков, вентканала и размер санузла уточнить после приёмки квартиры 10.10.2026.
- 4. Размеры в миллиметрах, площади в м².
- 5. Размер санузла и положение стояков уточнить по месту — при столбе стояков в углу у ванны взять ванну 1500–1600.

Квартира 72 · ЖК Buta Zaman, Алматы · Дизайн-проект студии 37,4 м²	ЛистЛистов	
Развѐртка стен: санузел	10	14
Стадия: рабочие чертежи · Дата: 01.10.2026 · Масштаб 1:50 · Формат А3		

Развёртки: прихожая, гостиная, спальня

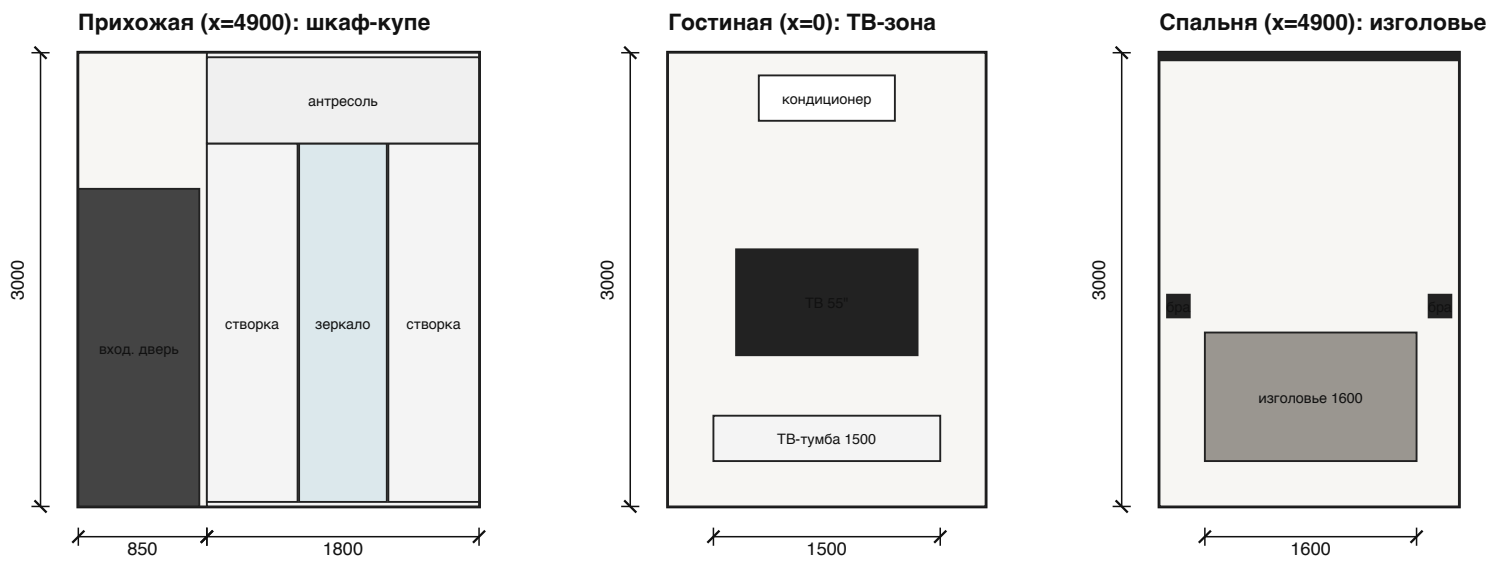

Шкаф-купе: 3 створки 600 мм, средняя — зеркало; глубина 600; наполнение: штанга 1100, полки, ящики, обувь внизу, антресоль от 2400. Направляющая — к закладной.

ТВ-зона: подвесная тумба, провода в штробе за ТВ (розетки x2 + интернет/ТВ h=1100, розетка у тумбы h=350). Кондиционер — вывод h=2750, трасса на балкон.

Спальня: изголовье мягкое 1600x850, бра h=1300 с выключателями у кровати, розетки с USB h=600 с обеих сторон, шторы от потолка (скрытый карниз в нише).

Цвет стен: светло-серый тёплый (RAL 9002 / 7047 или аналог), потолок белый. Плинтус белый 60 мм. Двери и рамы — чёрный матовый.

- ПРИМЕЧАНИЯ
- 1. За отметку 0.000 принят уровень чистового пола.
 - 2. Все размеры уточнить по месту перед началом работ; привязки даны по неоштукатуренным стенам.
 - 3. Положение стояков, вентканала и размер санузла уточнить после приёмки квартиры 10.10.2026.
 - 4. Размеры в миллиметрах, площади в м².

Квартира 72 · ЖК Buta Zaman, Алматы · Дизайн-проект студии 37,4 м²	ЛистЛистов	
Развёртки: прихожая, гостиная, спальня	11	14
Стадия: рабочие чертежи · Дата: 01.10.2026 · Масштаб 1:50 · Формат А3		

Визуализация



Общий вид (3D)



Гостиная, вид на спальню



Спальня



Кухня



Санузел

Визуализации выполнены в Blender (Cycles) по рабочей 3D-модели. Материалы и мебель — схематичные, по палитре проекта: стены светло-серые, пол светлый дуб, фасады белые матовые, акценты чёрные.

Квартира 72 · ЖК Bura Zaman, Алматы · Дизайн-проект студии 37,4 м²	ЛистЛистов	
Визуализация	12	14
Стадия: рабочие чертежи · Дата: 01.10.2026 · Масштаб — · Формат A3		

Ведомость материалов

Отделка помещений

№	Помещение	Пол	Стены	Потолок	Площадь
1	Прихожая	Керамогранит 600х600 + тёплый пол	Краска	Натяжной	6,3 м²
2	Санузел	Керамогранит 600х600 + тёплый пол	Керамогранит 600х600	Натяжной влагост.	4,3 м²
3	Кухня	Ламинат 33 кл.	Краска; фартук керамогранит	Натяжной	~6,5 м²
4	Гостиная	Ламинат 33 кл.	Краска	Натяжной	~9,0 м²
5	Спальня	Ламинат 33 кл.	Краска	Натяжной	~6,5 м²
6	Балкон	Керамогранит	Краска	Натяжной / покраска	3,0 м²

Ведомость отделки

Элемент	Кол-во
Ламинат (с запасом 7%)	29 м²
Керамогранит пол	13 м²
Керамогранит стены санузла	20 м²
Фартук кухни	2,5 м²
Стены под покраску	~90 м²
Натяжной потолок	~36 м²
Плинтус	30 м
Нагревательный мат	5 м²

Ведомость электрики

Электрика	Кол-во
Розетки	16
Силовые выводы	7
Выключатели / выводы света	20
Слаботочные точки	3
Споты GX53	9
Подвес / бра	1 / 2
LED-лента	5 м
Терморегуляторы	2

Ведомость сантехники

Сантехника	Кол-во
Ванна акриловая 1700х700	1
Унитаз подвесной + инсталляция	1
Тумба с раковиной 750	1
Смесители (ванна, раковина, кухня)	3
Мойка кухонная	1
Полотенцесушитель эл.	1
Точки воды / канализации	17

Палитра



Стены: светло-серый тёплый



Потолок, фасады: молочно-белый



Пол: светлый дуб



Столешница, плитка: светлый камень



Текстиль: серо-бежевый



Рама, ручки, светильники: чёрный матовый

Встроенная мебель: шкаф-купе 1800х600х3000 (3 створки, зеркало); кухня 4,26 пог. м, верх до потолка, фасады без ручек; стеклянная раздвижная перегородка 3250х3000, 4 створки, чёрный профиль.

Техника: холодильник (колонна), варочная индукционная, вытяжка встраиваемая, микроволновка, стиральная машина, посудомойка 45 см, кондиционер, телевизор 55".

Смета

Сводная смета (цены satu.kz, Алматы, 29.09.2026; работа мастеров — ориентировочно)

Раздел	Когда	Сумма, ₸
1. Стены санузла, штукатурка, стяжка	недели 1–3	574 100
2. Сантехника черновая	недели 1–2	230 000
3. Электрика черновая	неделя 2	760 000
4. Тёплый пол	неделя 5	78 000
5. Плитка	неделя 5	444 000
6. Стены, потолок, пол	недели 6–7	977 800
7. Электрика чистовая	неделя 8	170 500
8. Сантехника чистовая	неделя 8	485 000
9. Встроенная мебель	замер — неделя 4, установка — неделя 8	1 440 000
10. Техника	к установке кухни	1 270 000
11. Мебель и текстиль	в конце	1 020 000
12. Прочее	весь ремонт	288 000
Итого		7 737 400
Запас 10 %		773 740
Всего с запасом		8 511 140

Крупнейшие позиции	Кол-во	Цена	Сумма	Разд.
Стекланная раздвижная перегородка ~10 м² (от 6	1 шт	700 000	700 000	9
Кухонный гарнитур ~4 пог. м, эконом (от 40–80	1 шт	450 000	450 000	9
Работа электрика: ~50 точек, штробы, щиток, чи	1 усл	350 000	350 000	3
Диван	1 шт	300 000	300 000	11
Кондиционер с монтажом и трассой	1 шт	280 000	280 000	10
Шпаклёвка и покраска стен (работа) — уточнить	90 м²	3 000	270 000	6
Шкаф-купе 1,8 × 0,6 × 3 м (от 190 000 ₸)	1 шт	250 000	250 000	9
Холодильник	1 шт	250 000	250 000	10
Ламинат 33 класс (Tarkett / Navigator)	28 м²	8 300	232 400	6
Укладка плитки (работа) — уточнить	31 м²	7 000	217 000	5
Штукатурка стен машинная (работа)	100 м²	2 000	200 000	1
Посудомоечная машина 45 см встраиваемая	1 шт	200 000	200 000	10
Стиральная машина	1 шт	180 000	180 000	10
Керамогранит 60х60 / 60х120: санузел стены и п	34 м²	5 000	170 000	5
Натяжной потолок матовый с монтажом — уточнить	36 м²	4 500	162 000	6
Телевизор	1 шт	150 000	150 000	10
Кровать 160х200	1 шт	150 000	150 000	11
Матрас 160х200	1 шт	150 000	150 000	11
Кабель ВВГнг-LS 3х2,5 (розетки, техника, тёплы	200 м	720	144 000	3
Тумба с раковиной подвесная 60 см	1 шт	120 000	120 000	8
Варочная панель индукционная	1 шт	120 000	120 000	10
Стяжка пола полусухая (материал + работа)	34 м²	3 500	119 000	1
Стол + 2 стула	1 компл	100 000	100 000	11
Вывоз мусора, доставка, подъём материалов	1 усл	100 000	100 000	12

Полная смета по всем позициям (с редактированием цен) — на сайте проекта: leylagxx.github.io/kvartira72

Работа по сантехнике не учтена (выполняется своими силами). Позиции, которые выгодно заказать из Китая, отмечены на сайте — экономия ~260 тыс. ₸.

Квартира 72 · ЖК Buta Zaman, Алматы · Дизайн-проект студии 37,4 м²	ЛистЛистов	
Смета	14	14
Стадия: рабочие чертежи · Дата: 01.10.2026 · Масштаб — · Формат А3		