ДИЗАЙН-ПРОЕКТ

Квартира № 72 · ЖК Buta Zaman · г. Алматы

Студия 4,94 × 8,31 м (37,4 м²) · высота потолка 2,90 м · планировка по эскизу владельца от 09.11.2026

Санузел 2,8 × 2,3 с колонной стиралка + сушилка · кухня Г 1,6 + 2,17 м с двумя колоннами · ТВ на стене санузла в бамбуке · шкаф 2,4 м с сиденьем и зеркалом у входа

Спальня за стеклянной раздвижной перегородкой 4 м с карманом · изголовье 3 м до потолка · балкон с рабочей зоной · тёплые полы в прихожей и санузле · мастер-выключатель у входа


Состав альбома

2. Обмерный план
3. Планировочное решение
4. План монтажа перегородок
5. Напольные покрытия
6. План осветительных приборов
7. План розеток
8. План выключателей и мастер-выключателя
9. План потолка
10. План сантехнического оборудования
11. План радиаторов и тёплых полов
12. Развёртка стен: кухня
13. Развёртка стен: санузел
14. Развёртка стен: прихожая
15. Развёртка стен: гостиная
16. Развёртка стен: спальня
17. Мебель: схема
18. Мебель: размеры для мебельщика
19. Визуализация 1
20. Визуализация 2
21. Ведомость материалов

Исполнитель: Claude (ИИ-ассистент) по заданию владельца · 09.11.2026 · Не является официальной проектной документацией: нормы, сечения и крепления проверяют исполнители работ.

Обмерный план

КВАРТИРА 72

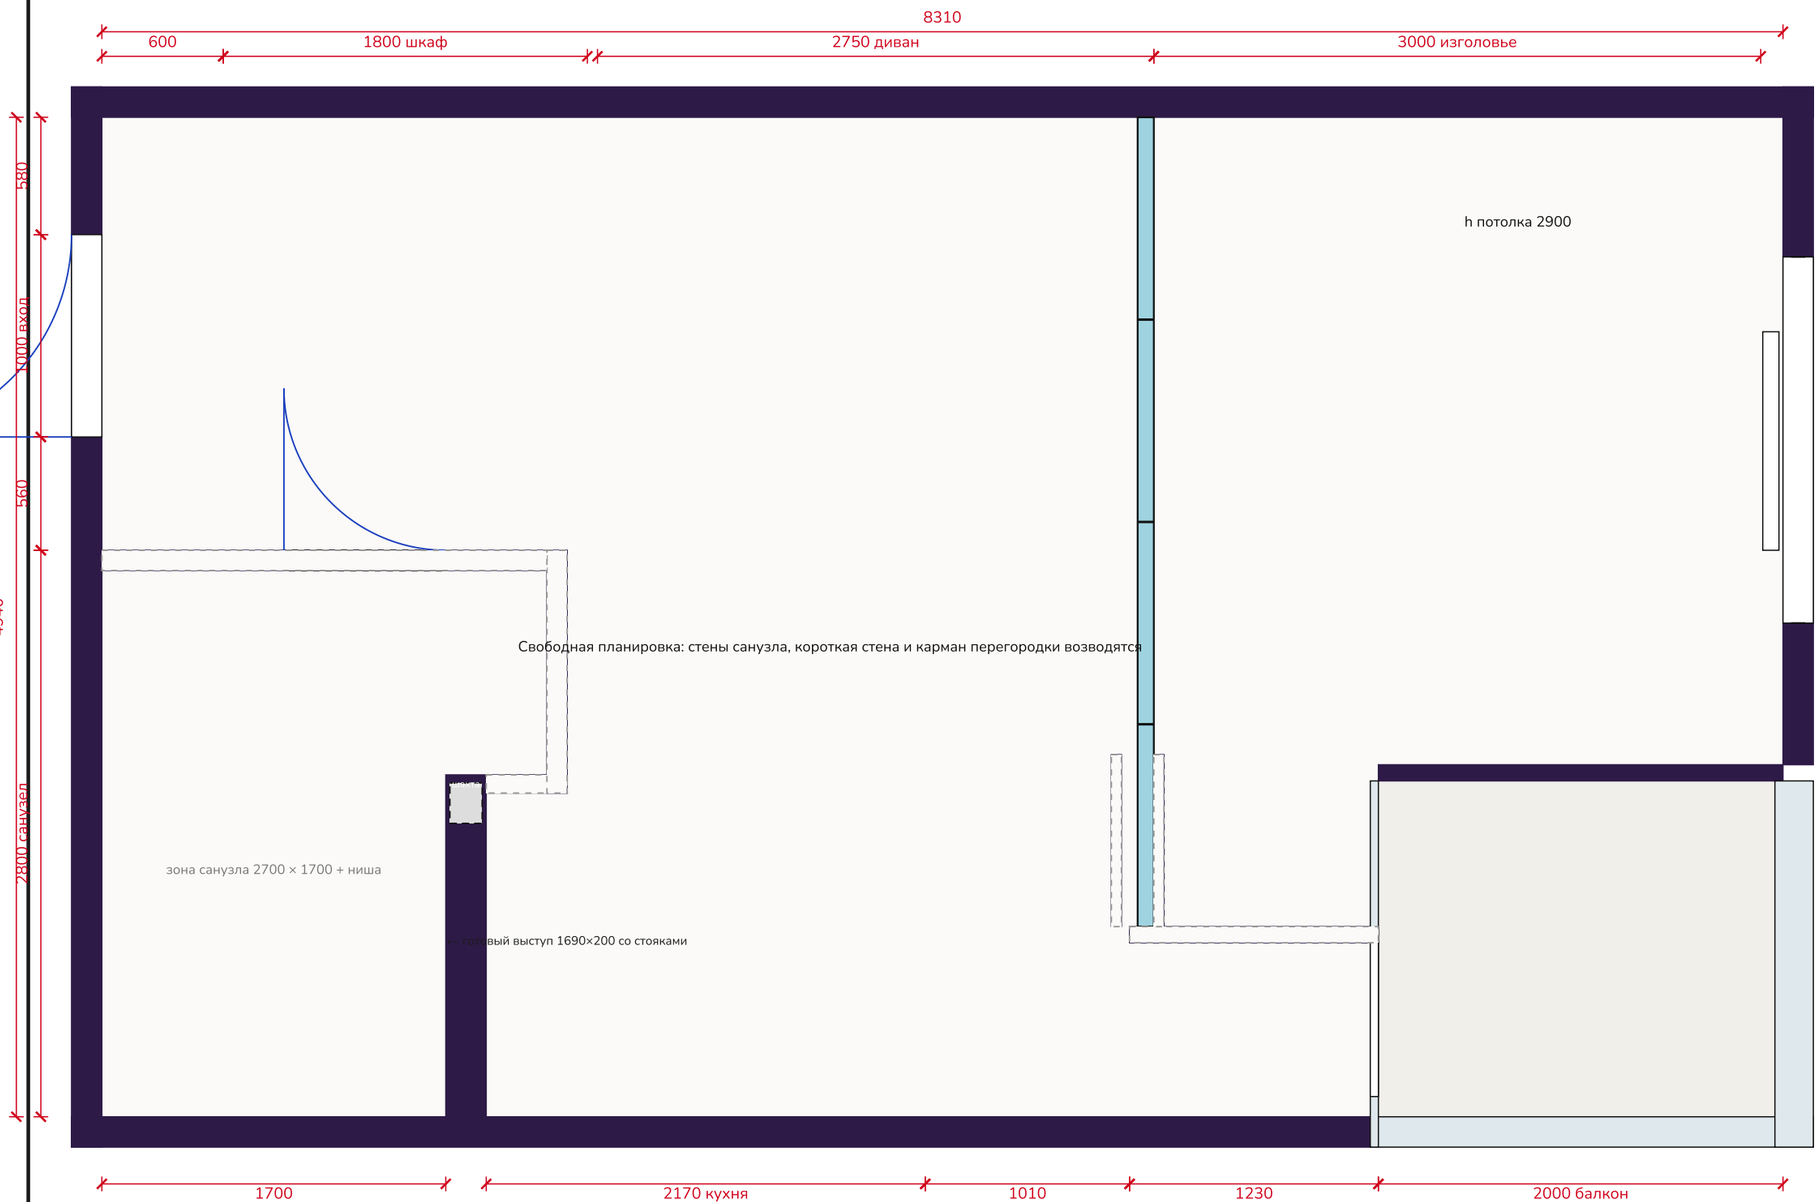

Условные обозначения

- Несущие стены (монолит) и готовый выступ
- Возводимые каркасные перегородки (пунктир)
- Стеклянная раздвижная перегородка 4 м
- Стояки / вентканал в выступе
- Остекление балкона и вход на балкон


ПРИМЕЧАНИЯ:

1. За отметку 0.000 принят уровень чистового пола.
2. Все размеры уточнить по месту перед началом работ; привязки даны по неоштукатуренным стенам.
3. Размеры в миллиметрах, площади в м². Планировка — по эскизу владельца от 09.11.2026.
4. Эскиз 09.11.2026: 4 940 × 8 310; по входной стене 600 | дверь 1 000 | 560 | санузел 2 800; по правой стене выступ 1 700 | кухня 2 170 | 1 010 | короткая стена 1 230 | балкон 2 000.
5. Балкон внутри 1 660 × 2 000, стена балкон/спальня ~80; окно 1 810 (простенки 700 и 690). Входная дверь открывается наружу.

Стадия	Лист	Листов	Квартира 72 · ЖК Buta Zaman · Алматы
РД	2	21	Обмерный план 09.11.2026 · М 1:30 · А3

Планировочное решение

КВАРТИРА 72

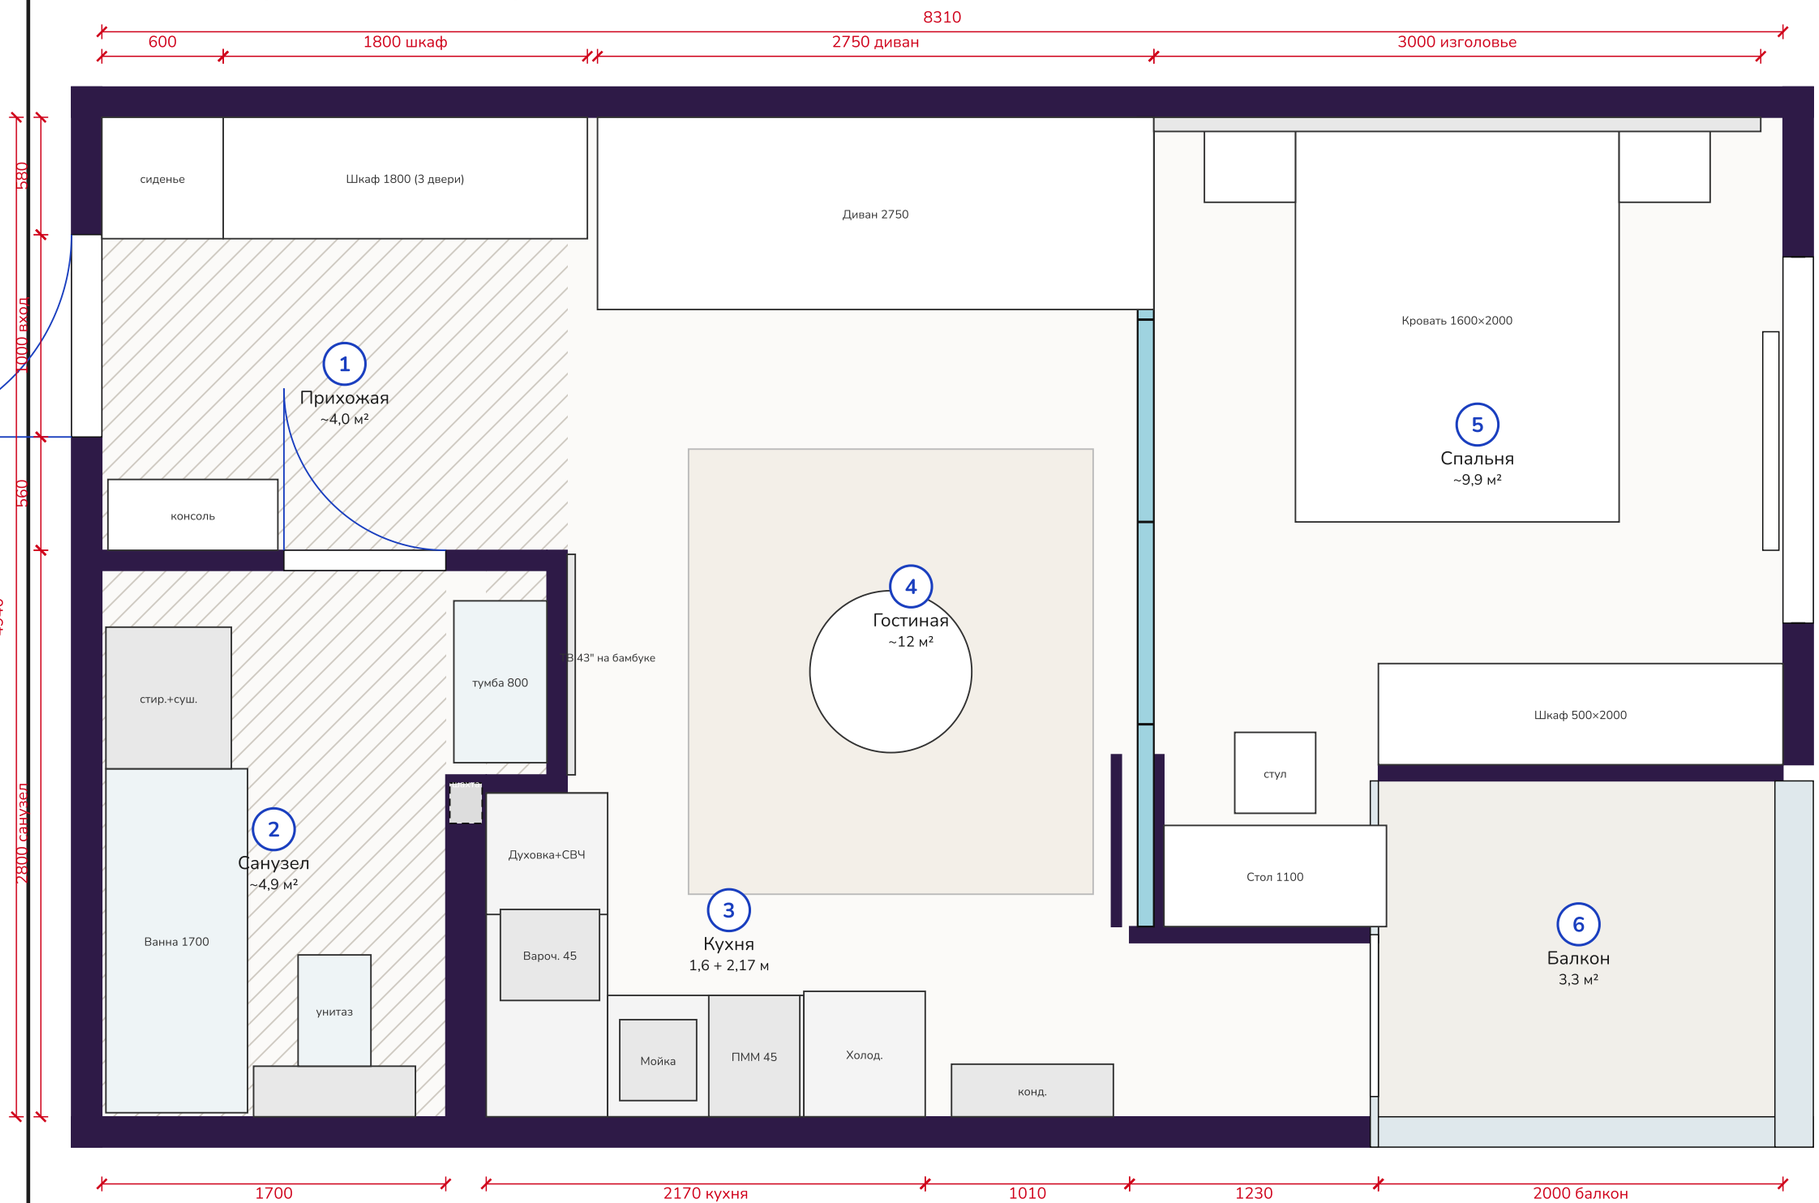

Спецификация помещений

№	Помещение	Площадь
1	Прихожая (без шкафа)	~4,0 м²
2	Санузел с нишей	~4,9 м²
3	Кухня	~5,5 м²
4	Гостиная	~12 м²
5	Спальня	~9,9 м²
6	Балкон	3,3 м²
	Итого по техпаспорту	37,4 м²

Покрытия пола:

Ламинат 33 кл. — кухня, гостиная, спальня (~27 м²)

Керамогранит: прихожая 200×200 PM213460 (~4,3 м²), санузел 600×1200 (~4,9 м²)

Балкон — керамогранит (~3,3 м²)


ПРИМЕЧАНИЯ:

1. За отметку 0.000 принят уровень чистового пола.
2. Все размеры уточнить по месту перед началом работ; привязки даны по неоштукатуренным стенам.
3. Размеры в миллиметрах, площади в м². Планировка — по эскизу владельца от 09.11.2026.
4. Перегородка спальни 4 м: 4 стеклянные створки по 1 000 в чёрном профиле, уезжают в карман 850 у короткой стены.
5. Дверь санузла 800 открывается в прихожую, петли со стороны консоли — открытая дверь встаёт к консоли и не закрывает выключатели за ней.
6. Проход к балкону вдоль правой стены — 950 (между короткой стеной и кухонной колонной 1 010).

Стадия	Лист	Листов	Квартира 72 · ЖК Buta Zaman · Алматы
РД	3	21	Планировочное решение 09.11.2026 · М 1:30 · А3

План монтажа перегородок

КВАРТИРА 72

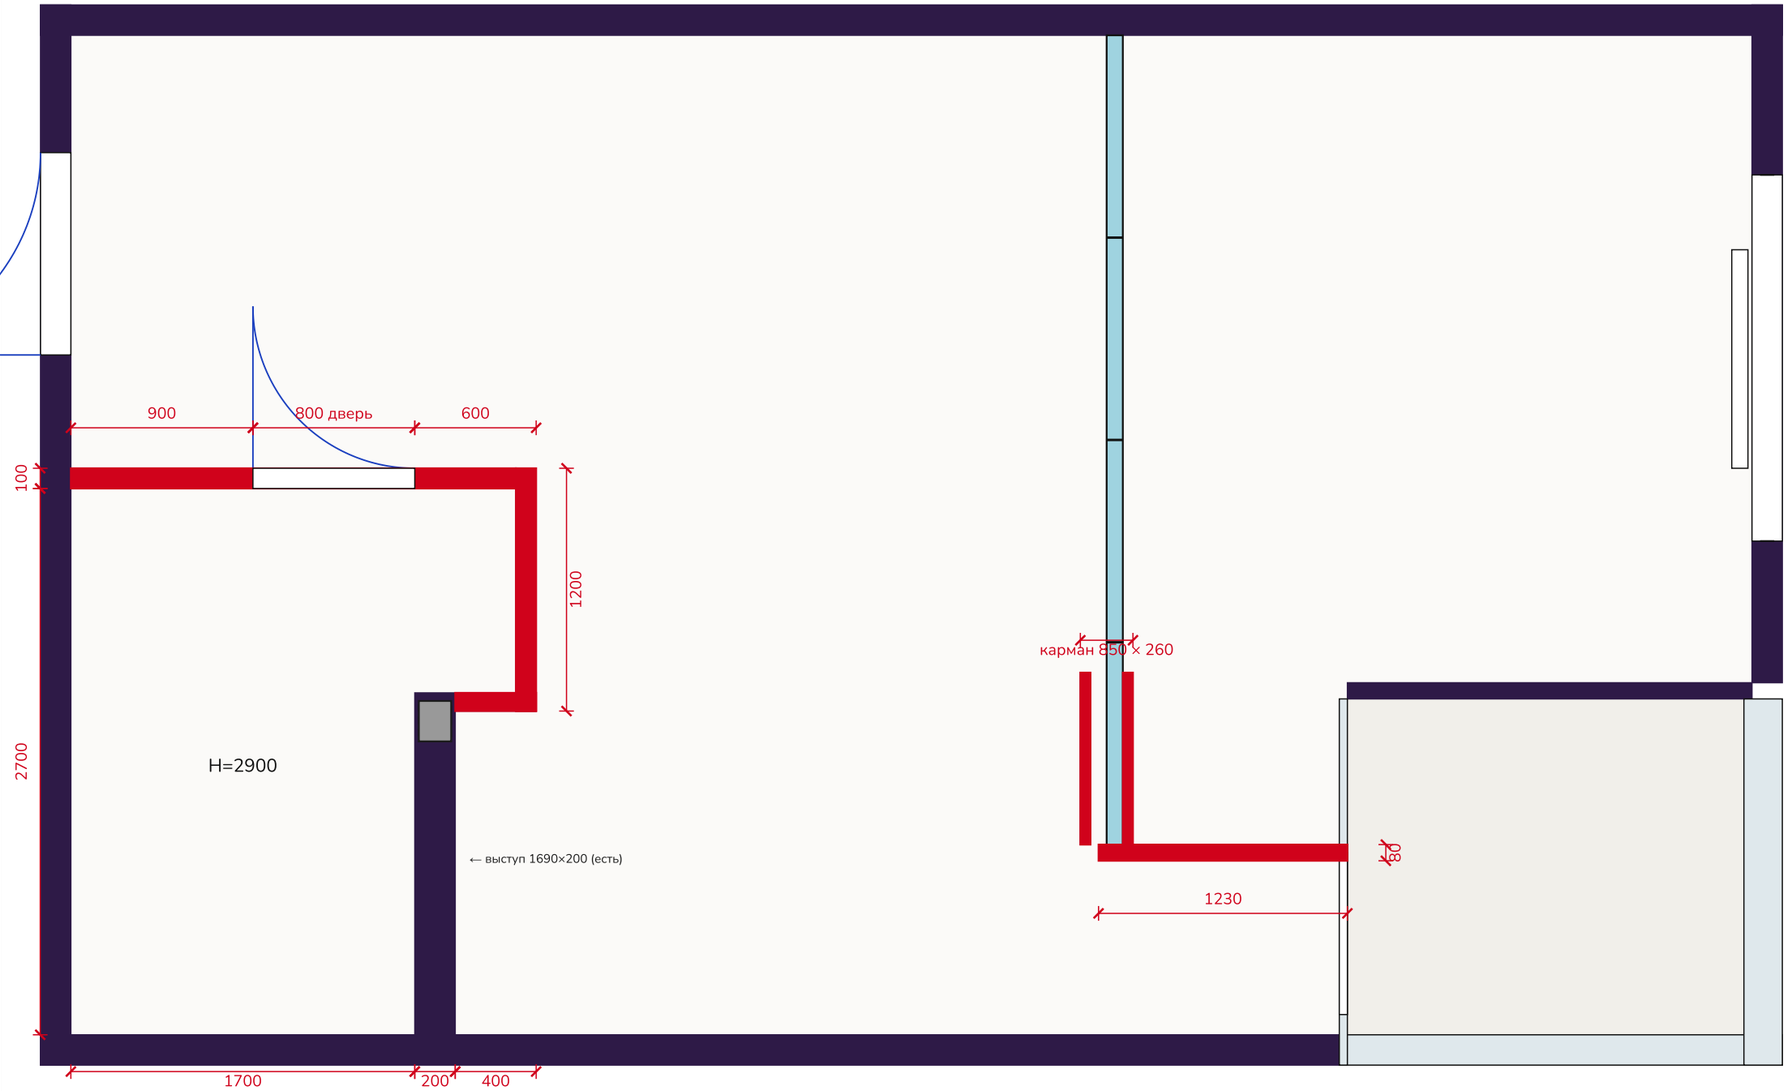

Условные обозначения

- Существующие стены и выступ
- Возводимые перегородки: ГКЛ влагостойкий на профиле ПС 75
- Стояки / вентшахта в выступе
- Стеклянная раздвижная перегородка (чистовая стадия)

Спецификация перегородок

Элемент	Длина	Слои ГКЛ	Примечание
Санузел, стена с дверью (x=2,7)	2 200	2+2	закладные под ТВ и консоль
Стенка за ТВ (z=2,2)	1 200	2+2	закладные под ТВ
Борт ниши раковины	300	2+1	
Короткая стена у балкона	1 230	1+1	каркас 75
Карман перегородки	2 × 850	1 | 1	в свету ≥ 120
Итого стен	~6 600		~19 м² в одну сторону


ПРИМЕЧАНИЯ:

1. За отметку 0.000 принят уровень чистового пола.
2. Все размеры уточнить по месту перед началом работ; привязки даны по неоштукатуренным стенам.
3. Размеры в миллиметрах, площади в м². Планировка — по эскизу владельца от 09.11.2026.
4. Каркас ПС/ПН 75 с шагом стоек 400, минвата 50 мм внутри, со стороны санузла и за ТВ — два слоя влагостойкого ГКЛ. Инсталляция унитаза — на своей раме с креплением в пол и монолит правой стены.
5. Закладные из фанеры/OSB 18 мм внутри каркаса: ТВ + бамбук (z 2,2–2,3, h 0,8–1,6), зеркало и консоль (x 2,7–2,8, z 0–0,9), верхний шкаф колонны стиралка+сушилка (входная стена — монолит).
6. Карман перегородки: две стенки по 850 от короткой стены, между ними ≥120 в свету под 4 створки; направляющая — к закладному брусу до натяжного потолка.

Стадия	Лист	Листов	Квартира 72 · ЖК Buta Zaman · Алматы
РД	4	21	План монтажа перегородок 09.11.2026 · М 1:30 · А3

Напольные покрытия

КВАРТИРА 72

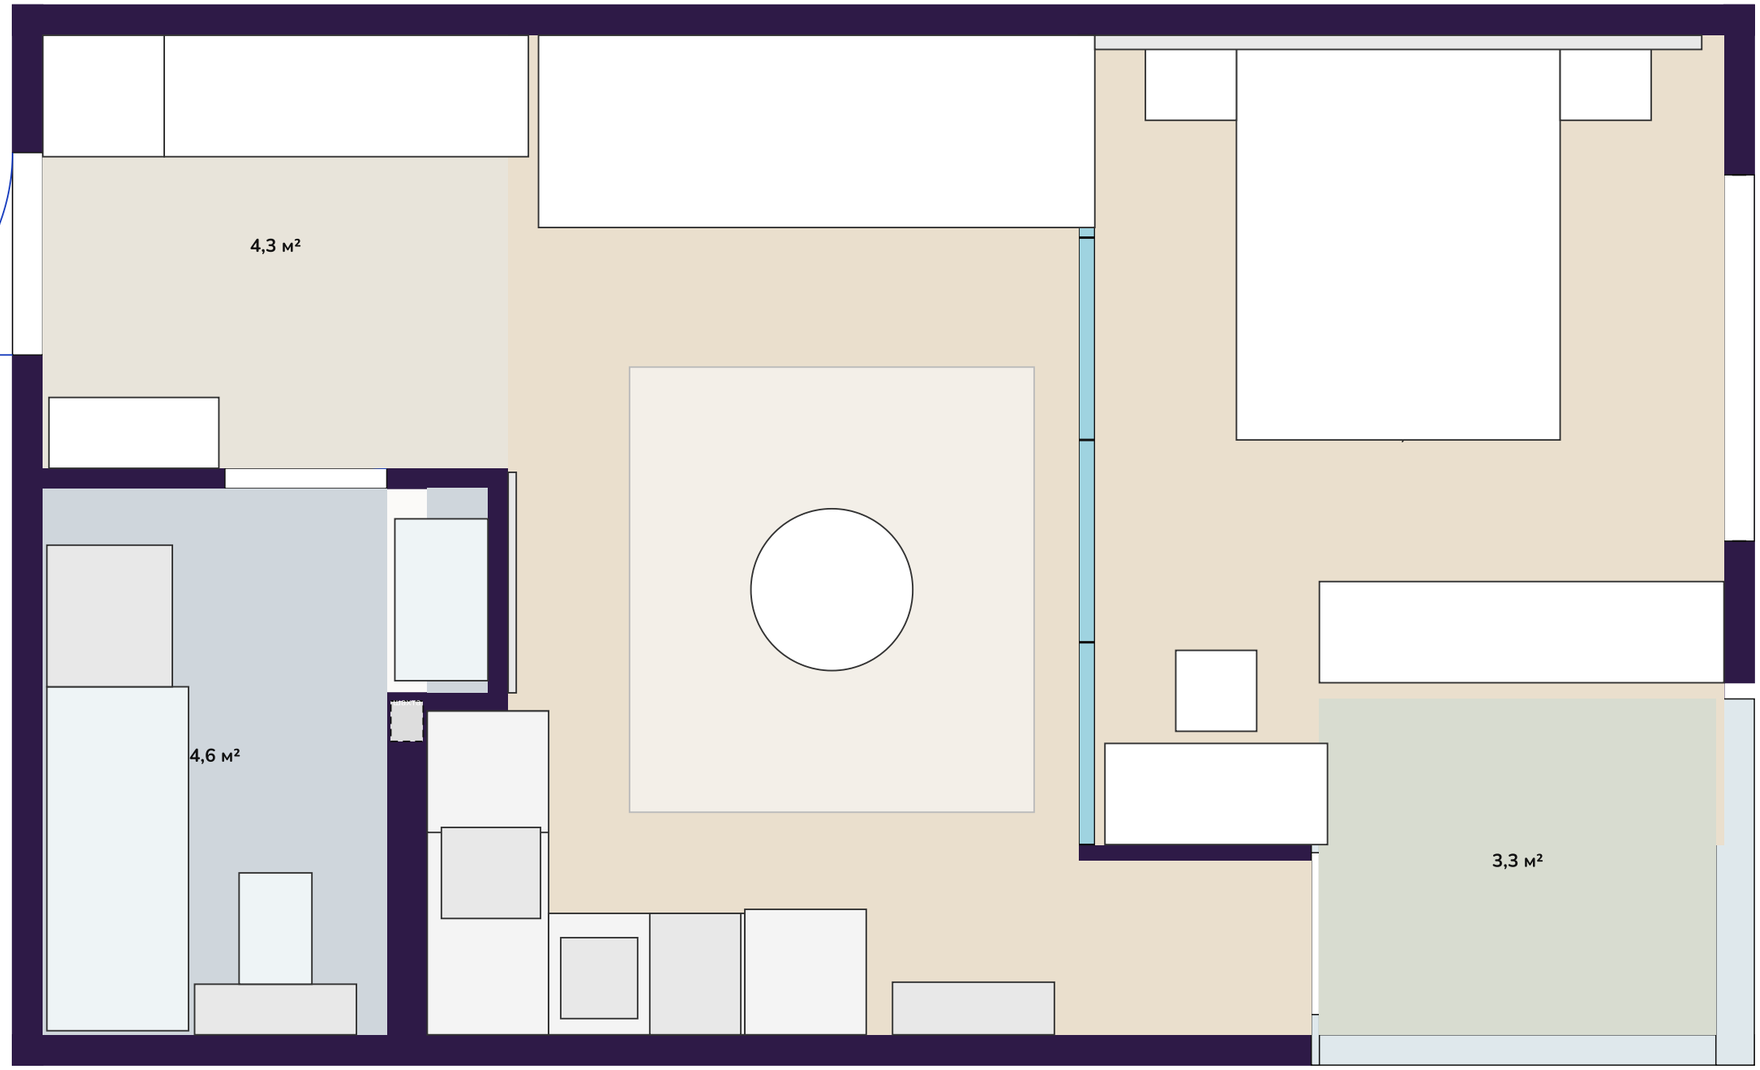

Спецификация

Покрытие	Площадь	С запасом
Ламинат 33 кл., 8 мм	26 м²	28,5 м² (+10%)
Керамогранит 600×1200 (санузел пол)	4,9 м²	5,5 м²
Керамогранит 200×200 PM213460 (прихожа	4,3 м²	5,0 м² (+15%)
Балкон: керамогранит	3,3 м²	3,7 м²
Подложка 3 мм	26 м²	28,5 м²
Плинтус 60 мм	—	30 м
Порожек плитка/ламинат	—	1 шт (прихожая–гостиная)

Количество указано с запасом на подрезку.


ПРИМЕЧАНИЯ:

1. За отметку 0.000 принят уровень чистового пола.
2. Все размеры уточнить по месту перед началом работ; привязки даны по неоштукатуренным стенам.
3. Размеры в миллиметрах, площади в м². Планировка — по эскизу владельца от 09.11.2026.
4. Ламинат укладывать вдоль длинной стороны (от входа к окну). Плитка прихожей и санузла — в один уровень с ламинатом (порожек 30 мм на границе прихожей).
5. Под плиткой в прихожей и санузле — электрический тёплый пол. Под шкафом, ванной, колонной и инсталляцией мат не кладут.

Стадия	Лист	Листов	Квартира 72 · ЖК Buta Zaman · Алматы
РД	5	21	Напольные покрытия 09.11.2026 · М 1:30 · А3

План осветительных приборов

КВАРТИРА 72

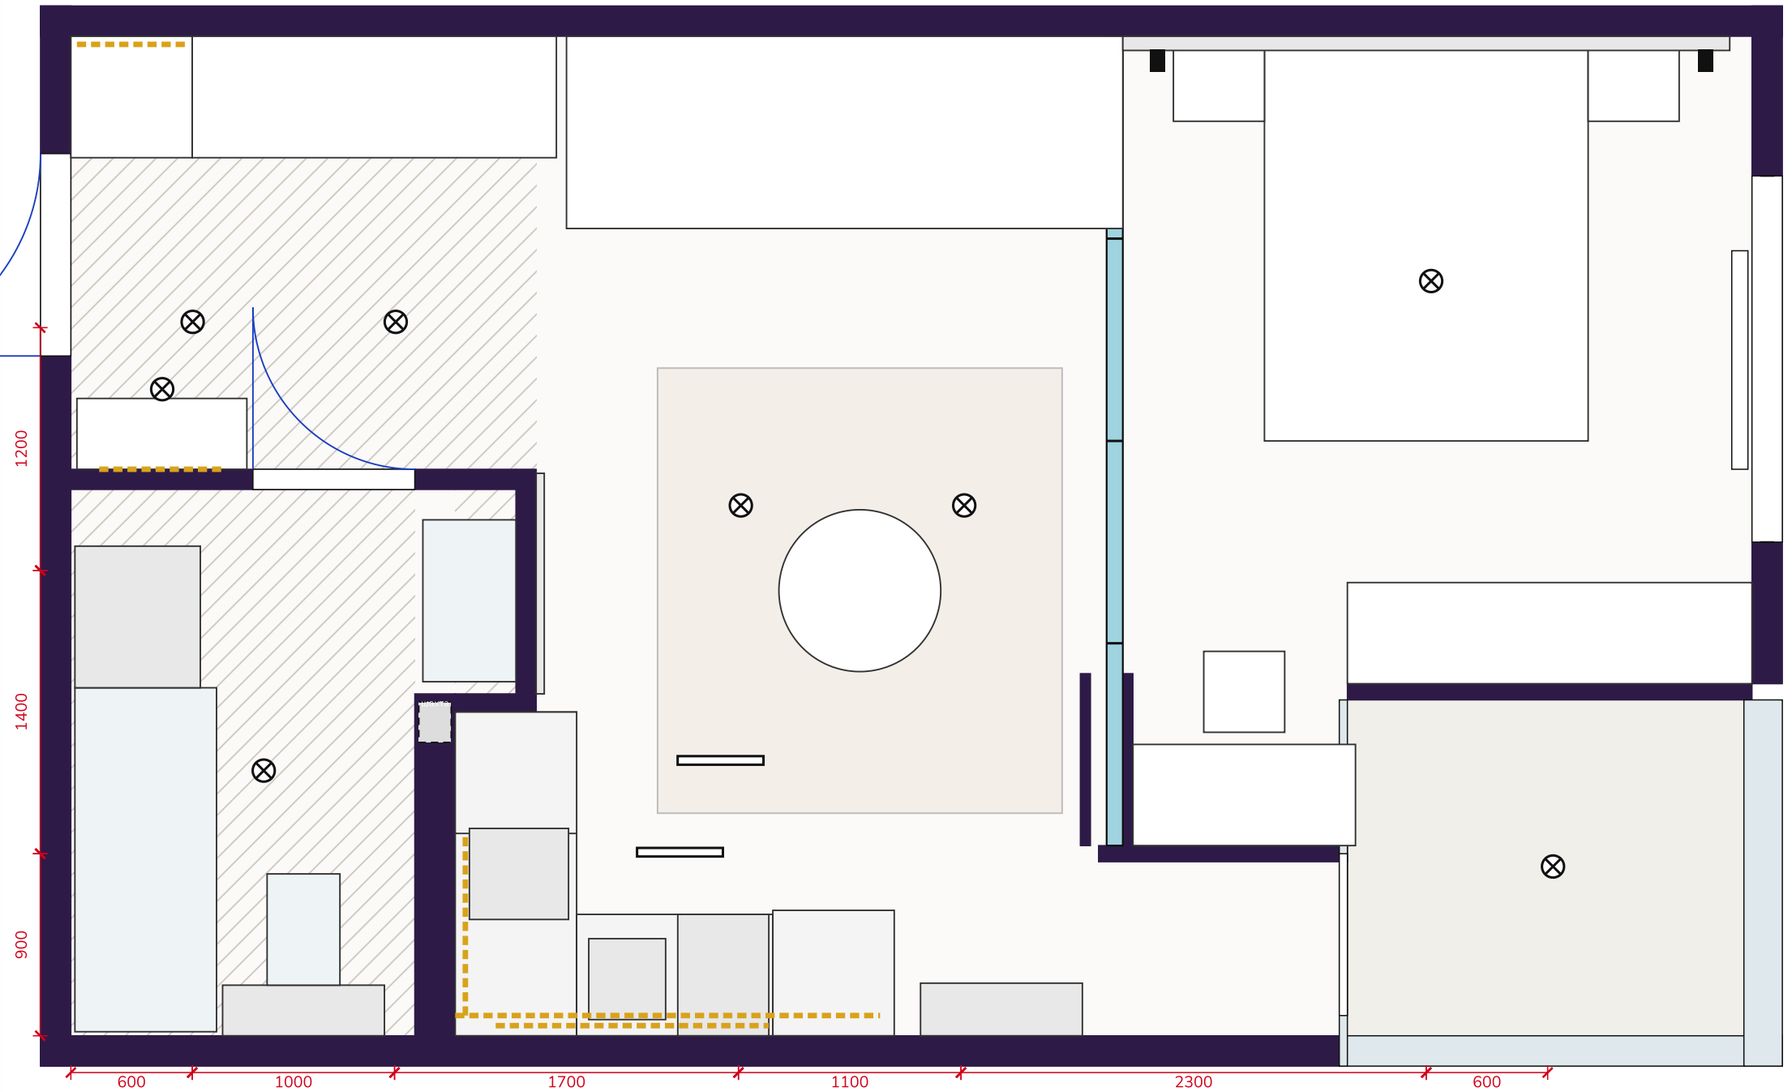

Условные обозначения

- Спот встраиваемый в натяжной потолок (IP44 в санузле)
- Световая линия в потолке кухни
- Бра на рейках изголовья, h=1200
- LED-лента 2700K: кухня, изголовье, зеркала, сиденье

Ведомость осветительных приборов

Наименование	Шт.
Спот встраиваемый: прихожая 3, санузел 1, гостиная 2, спальня 1, ба…	8
Световые линии в потолке кухни, ~3 м	2
Бра у кровати, чёрные	2
LED-лента с профилем и блоками, м	15
Зеркало с подсветкой: консоль у санузла, круглое в санузле	2
Вентилятор вытяжной с таймером	1


ПРИМЕЧАНИЯ:

1. За отметку 0.000 принят уровень чистового пола.
2. Все размеры уточнить по месту перед началом работ; привязки даны по неоштукатуренным стенам.
3. Размеры в миллиметрах, площади в м². Планировка — по эскизу владельца от 09.11.2026.
4. Привязки даны к центру светильника. Световые линии кухни — LED-профиль, встроенный в натяжной потолок, согласовать с потолочниками до монтажа.
5. Группы света: прихожая + консоль, санузел, кухня, гостиная (проходные), балкон, спальня (проходные с двух сторон кровати). Все группы — через мастер-выключатель.

Стадия	Лист	Листов	Квартира 72 · ЖК Buta Zaman · Алматы
РД	6	21	План осветительных приборов 09.11.2026 · М 1:30 · А3

План розеток

КВАРТИРА 72

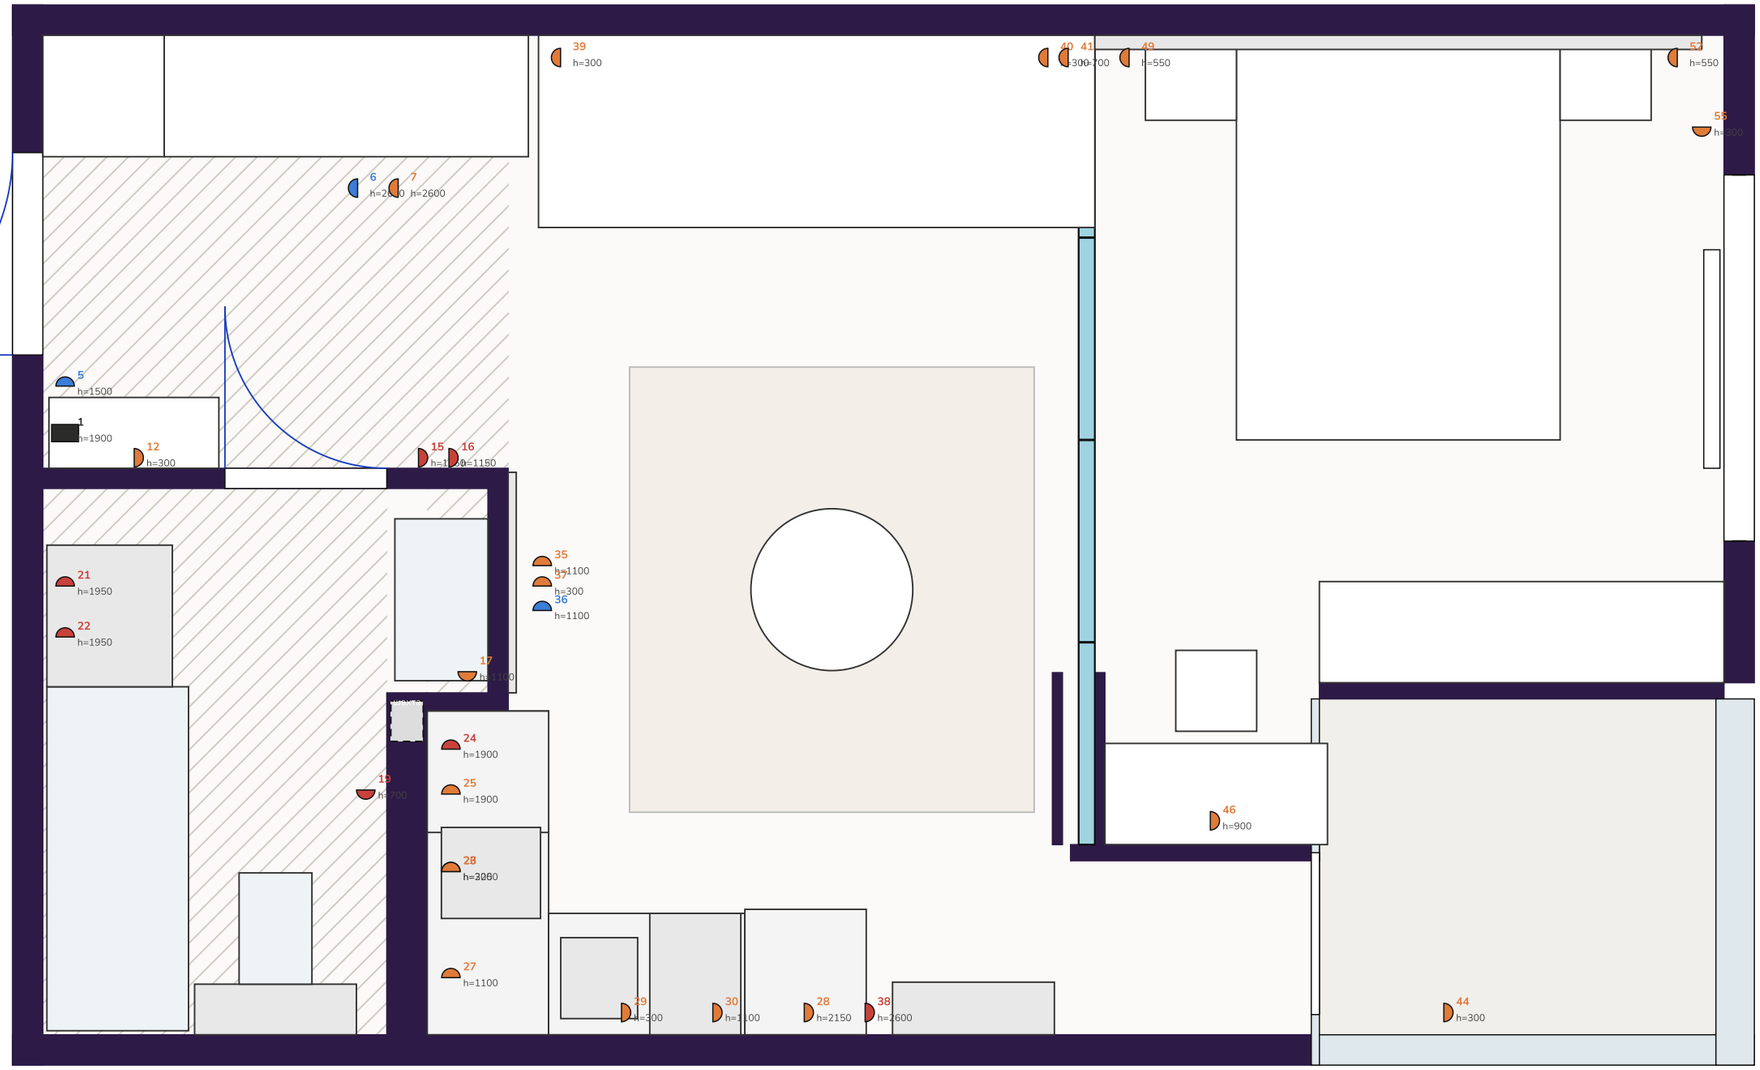

Условные обозначения

- Розетка (одинарная/двойная, USB), h=300 если не указано
- Силовой вывод / отдельная линия: техника, тёплый пол, кондиционер
- Интернет, ТВ, домофон
- Электрощиток 36 модулей, верх h≈2000

Ведомость

Наименование	Кол-во
Розетки, в т.ч. с USB и IP44	19
Силовые выводы и терморегуляторы	8
Слаботочные точки	3
Щиток	1


ПРИМЕЧАНИЯ:

1. За отметку 0.000 принят уровень чистового пола.
2. Все размеры уточнить по месту перед началом работ; привязки даны по неоштукатуренным стенам.
3. Размеры в миллиметрах, площади в м². Планировка — по эскизу владельца от 09.11.2026.
4. Высоты — до центра от чистого пола. Номера точек — по ведомости электрики (лист «План выключателей» и таблица на сайте).
5. Отдельные линии с автоматами: варочная 32 А (3×6), духовка, сушильная машина (3×4), стиральная, ПММ, холодильник+роутер, кондиционер, полотенцесушитель, 2 тёплых пола, 3 группы розеток. УЗО 30 мА: санузел; кухня + стиралка/сушилка; розетки комнат; тёплые полы.
6. Розетки стиралки и сушилки — внутри шкафа над колонной (h 1950), духовки и СВЧ — в колонне над СВЧ (h 1900), холодильника — в антресоли колонны (h 2150), ПММ — в шкафу под мойкой.

Стадия	Лист	Листов	Квартира 72 · ЖК Buta Zaman · Алматы
РД	7	21	План розеток 09.11.2026 · М 1:30 · А3

План выключателей и мастер-выключателя

КВАРТИРА 72

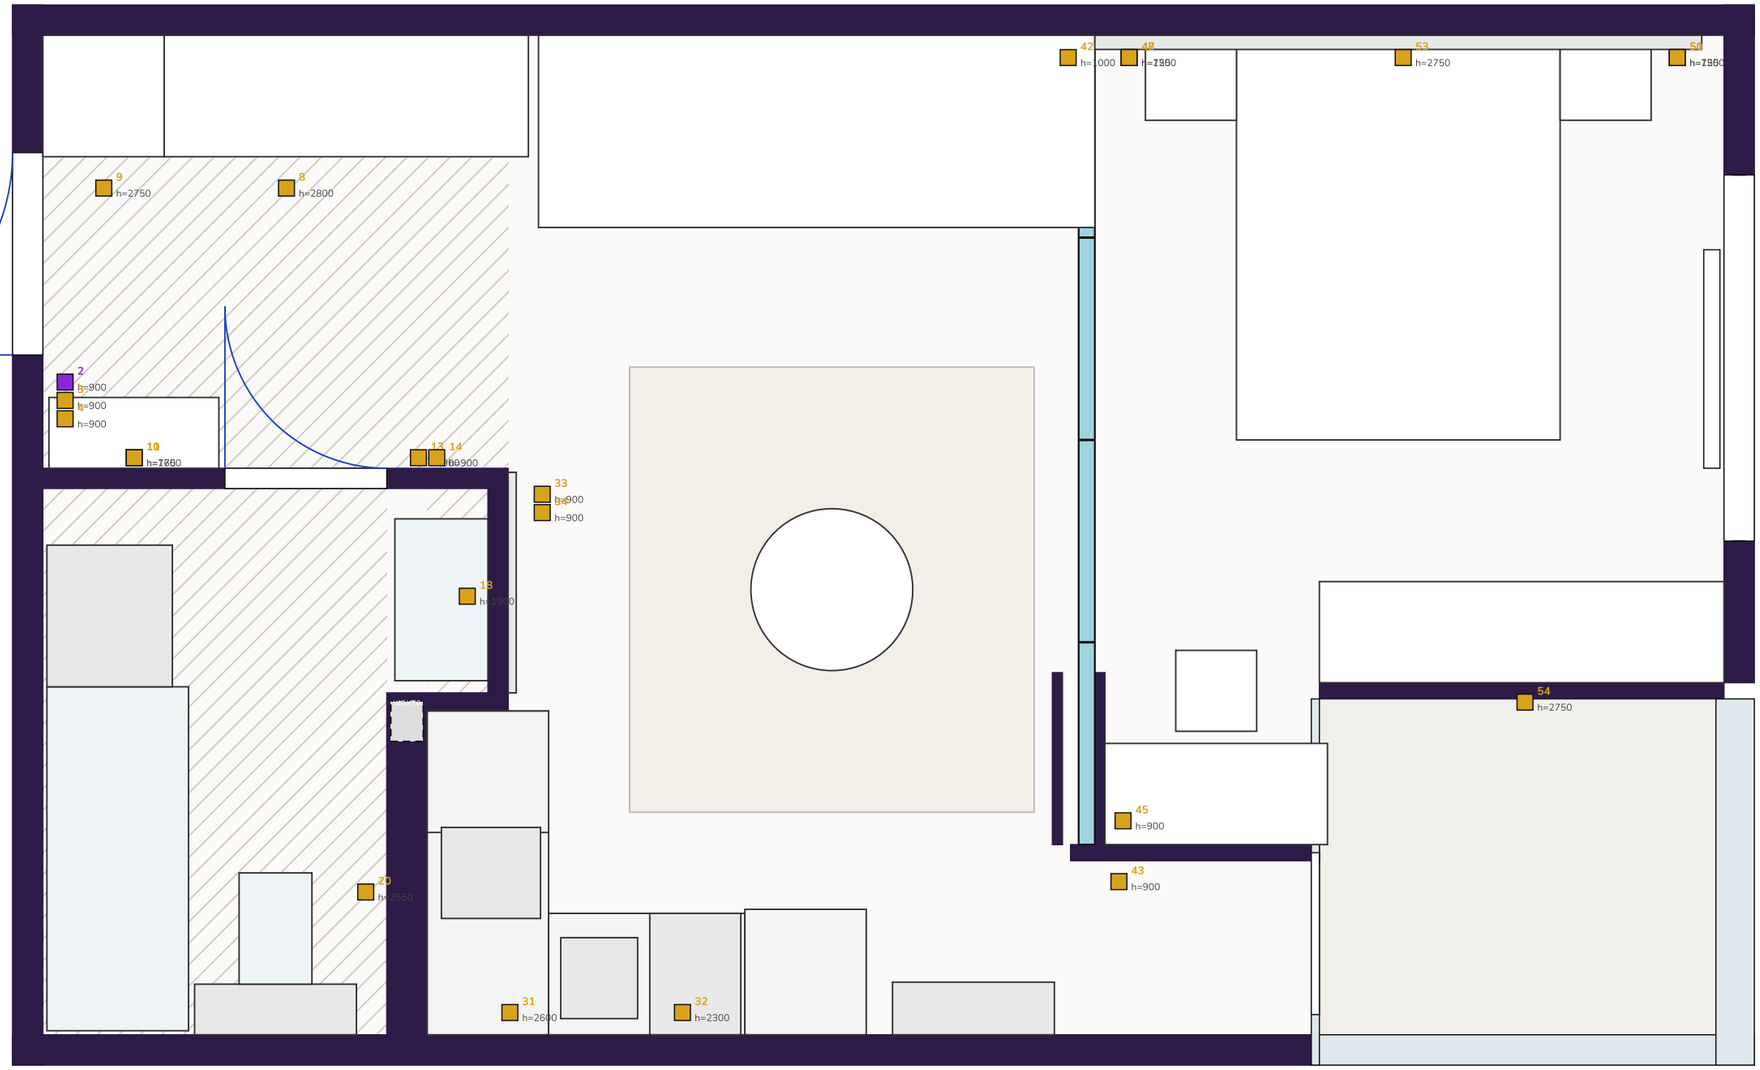

Условные обозначения

- Мастер-выключатель «всё выкл.» у входа, h=900
- Выключатель, h=900 (если не указано) / вывод под бра и подсветку

Ведомость выключателей и выводов

№	Выключатель / вывод	h
2	МАСТЕР-ВЫКЛЮЧАТЕЛЬ «всё выкл.»	900
3	Выключатель: свет прихожей	900
4	Выключатель: подсветка зеркала, консоли и сиденья	900
8	Вывод: подсветка в шкафу (от двери)	2800
9	Вывод: подсветка сиденья и зеркала у входа	2750
10	Вывод: подсветка зеркала у консоли (за зеркалом)	1750
11	Вывод: подсветка под консолью	760
13	Выключатель: свет санузла	900
14	Выключатель: вентилятор санузла (с таймером)	900
18	Вывод: подсветка зеркала санузла	1900
20	Вентилятор в вентканале выступа	2550
31	Вывод: подсветка под шкафами (сенсор в профиле)	2600
32	Вывод: подсветка витрины (от двери)	2300
33	Выключатель: кухня — потолок	900
34	Выключатель: гостиная — общий (проходной)	900
42	Выключатель: гостиная — общий (проходной, у перегоро	1000
43	Выключатель: свет балкона (в проходе)	900
45	Выключатель: свет спальни (у стола, проходной)	900
47	Вывод: бра слева (за рейками)	1250
48	Выключатели у кровати слева: бра + общий свет	750
50	Вывод: бра справа (за рейками)	1250
51	Выключатели у кровати справа: бра + общий свет	750
53	Вывод: подсветка изголовья (БП за панелью)	2750
54	Вывод: подсветка шкафа спальни (от двери)	2750


ПРИМЕЧАНИЯ:

1. За отметку 0.000 принят уровень чистового пола.
2. Все размеры уточнить по месту перед началом работ; привязки даны по неоштукатуренным стенам.
3. Размеры в миллиметрах, площади в м². Планировка — по эскизу владельца от 09.11.2026.
4. Мастер-выключатель (2): контактор в щитке отключает весь свет, бра, подсветки и розетки ТВ, дивана, стола, кровати. Не отключает холодильник, роутер, ПММ, стиралку, сушилку, кондиционер, тёплые полы, полотенцесушитель, духовку, варочную.
5. Проходные: общий свет гостиной (34 и 42), свет спальни (45, 48, 51). Выключатели санузла и терморегуляторы (13–16) — на стене санузла со стороны гостиной, за дверью.

Стадия	Лист	Листов	Квартира 72 · ЖК Buta Zaman · Алматы
РД	8	21	План выключателей и мастер-выключателя 09.11.2026 · М 1:30 · А3

План потолка

КВАРТИРА 72

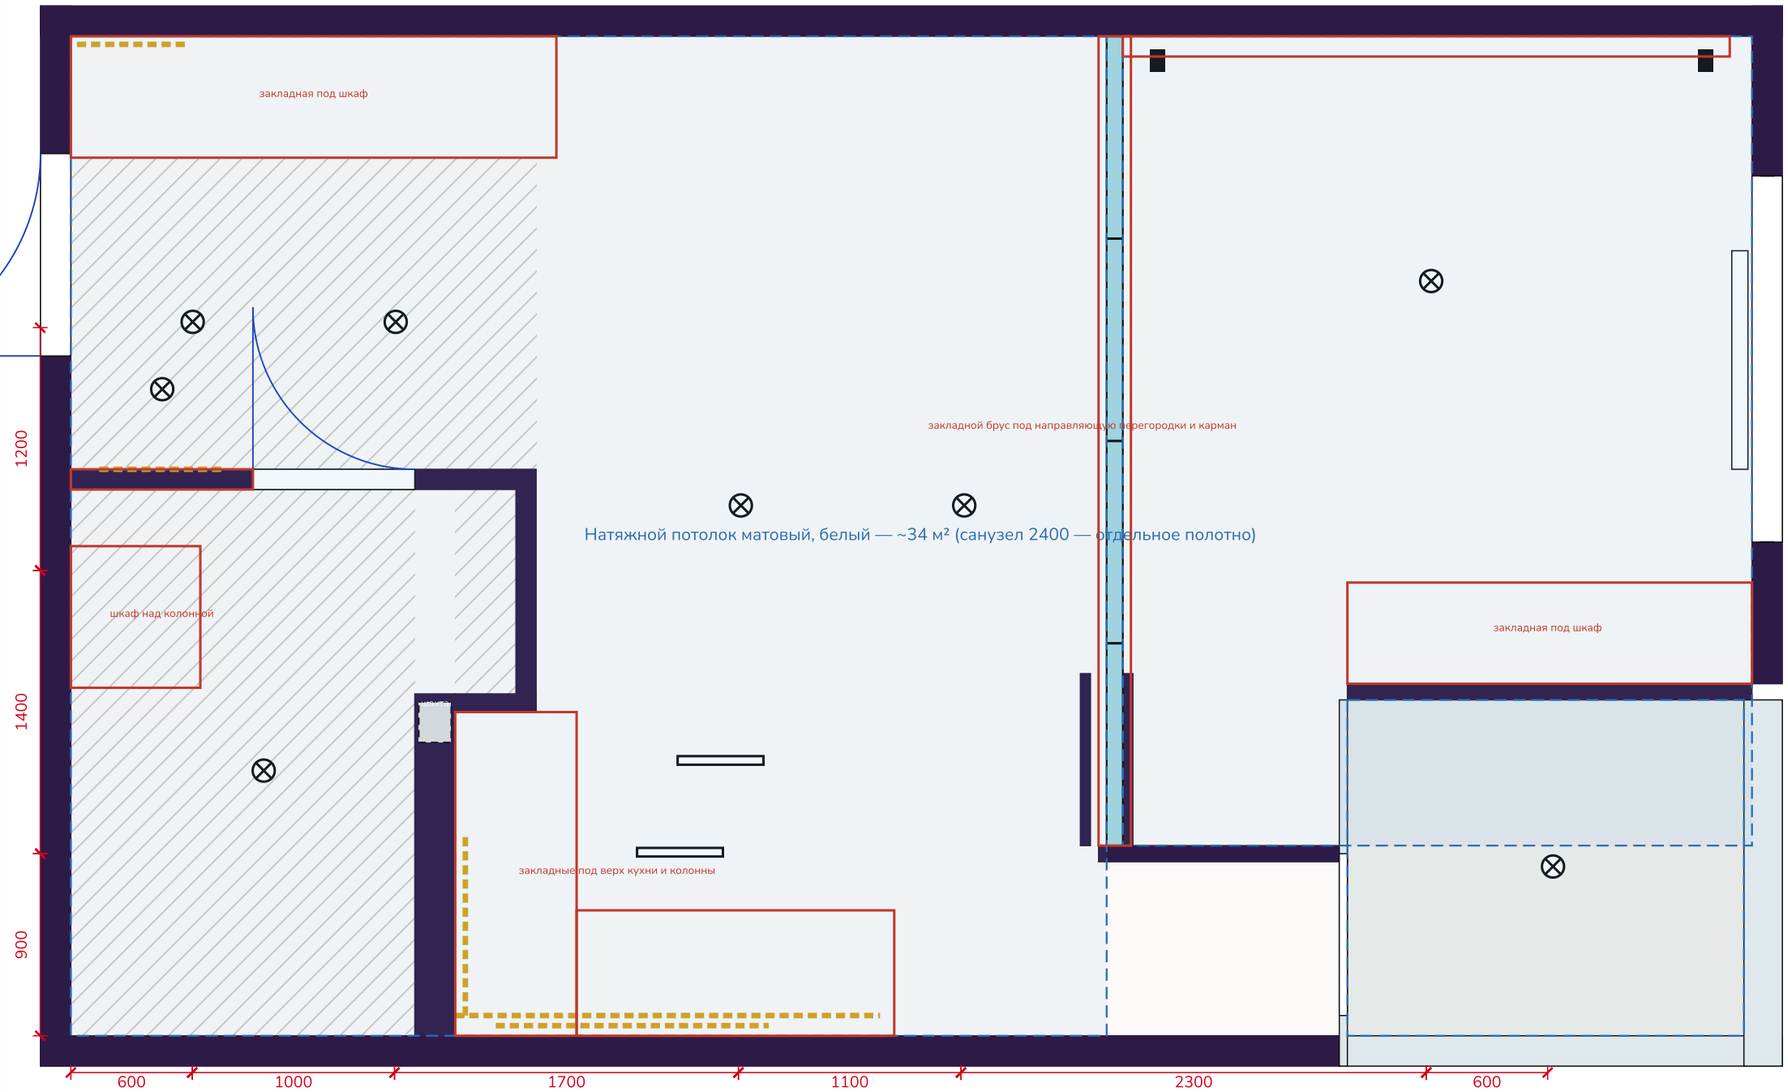

Условные обозначения

- ⊗ Спот встраиваемый, 8 точек
- Граница натяжного потолка
- Закладные (брус 60×60) до монтажа потолка: ~12 м

Потолок 2900; под споты полотно ниже на 80–100: ~2800. Санузел — 2400.

Световые линии кухни — закладной профиль в полотне.


ПРИМЕЧАНИЯ:

1. За отметку 0.000 принят уровень чистового пола.
2. Все размеры уточнить по месту перед началом работ; привязки даны по неоштукатуренным стенам.
3. Размеры в миллиметрах, площади в м². Планировка — по эскизу владельца от 09.11.2026.
4. Монтаж потолка — после покраски стен и до ламината; трасса кондиционера и кабели спотов — до потолка.
5. Все шкафы до потолка без зазора: закладной брус по линии фасада; корпус на 30–50 мм ниже, сверху доборная планка в цвет фасада. Замер шкафов — после монтажа потолка.

Стадия	Лист	Листов	Квартира 72 · ЖК Buta Zaman · Алматы
РД	9	21	План потолка 09.11.2026 · М 1:30 · А3

План сантехнического оборудования

КВАРТИРА 72

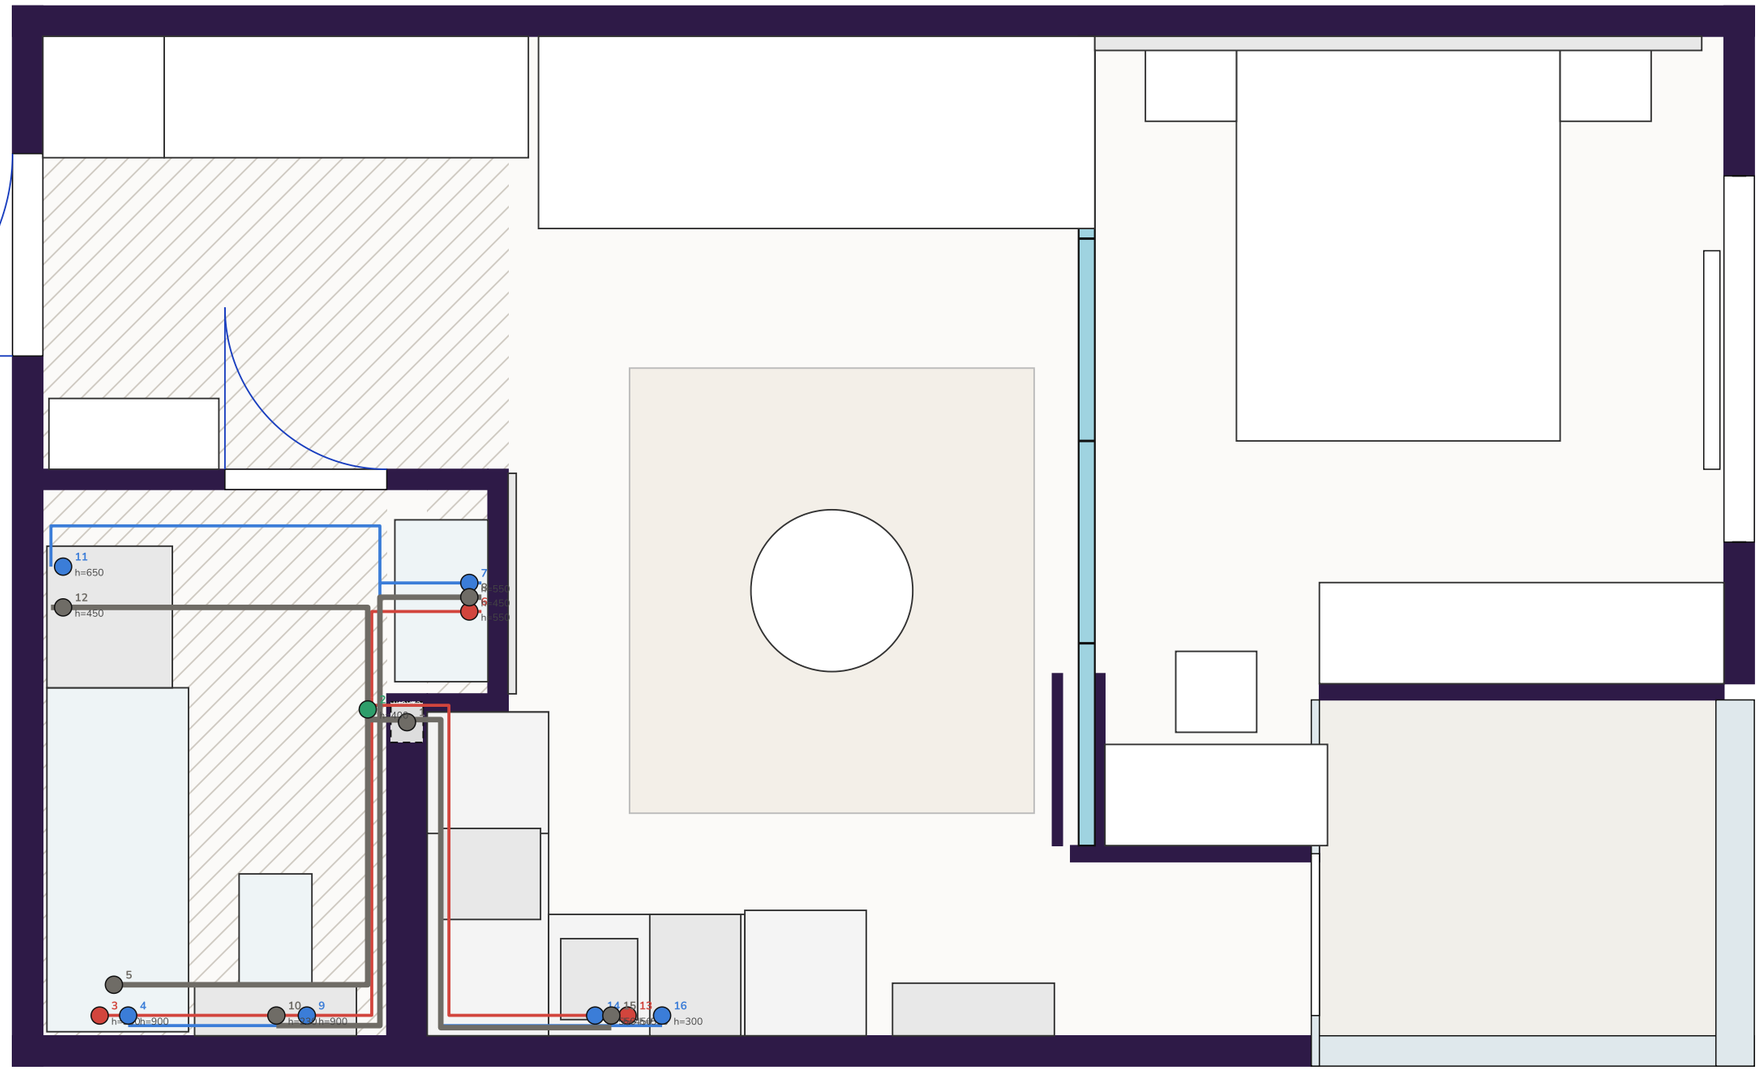

Условные обозначения

- Холодная вода
- Горячая вода
- Канализация Ø50 / Ø110
- Краны, фильтры, счётчики
- Точка вывода (номер — см. таблицу)

Ведомость точек

№	Точка	h, мм
1	Стояки и вентканалы — внутри выступа 169×20 (шахта	—
2	Краны, счётчики, фильтры (люк в выступе)	400
3	Ванна: смеситель с тропическим душем, горячая	900
4	Ванна: смеситель с тропическим душем, холодная	900
5	Ванна: слив Ø50	в полу
6	Раковина: горячая	550
7	Раковина: холодная	550
8	Раковина: слив Ø50	450
9	Унитаз: вода в инсталляцию	900
10	Унитаз: канализация Ø110	230
11	Стиральная машина: кран холодной воды + аквастоп	650
12	Стиральная машина: слив Ø50 с сифоном (сушилка — к	450
13	Мойка: горячая	550
14	Мойка: холодная	550
15	Мойка: слив Ø50	450
16	Посудомойка: кран на холодной, слив в сифон мойки	300


ПРИМЕЧАНИЯ:

1. За отметку 0.000 принят уровень чистового пола.
2. Все размеры уточнить по месту перед началом работ; привязки даны по неоштукатуренным стенам.
3. Размеры в миллиметрах, площади в м². Планировка — по эскизу владельца от 09.11.2026.
4. Горячая — слева, холодная — справа. Уклон канализации 2–3 см/м к стояку в выступе.
5. Ванна 1700×700 вдоль входной стены, смеситель и тропический душ — на правой стене. Унитаз на инсталляции — правая стена, ось 1 150 от входной стены. Раковина — в нише у кухни (z 1,9–2,2).
6. Колонна стиралка + сушилка у входной стены (x 1,72–2,42): вода и слив Ø50 в стяжке к стояку, сушилка конденсационная — без слива. Все приборы — через краны; ПММ — от мойки.

Стадия	Лист	Листов	Квартира 72 · ЖК Buta Zaman · Алматы
РД	10	21	План сантехнического оборудования 09.11.2026 · М 1:30 · А3

План радиаторов и тёплых полов

КВАРТИРА 72

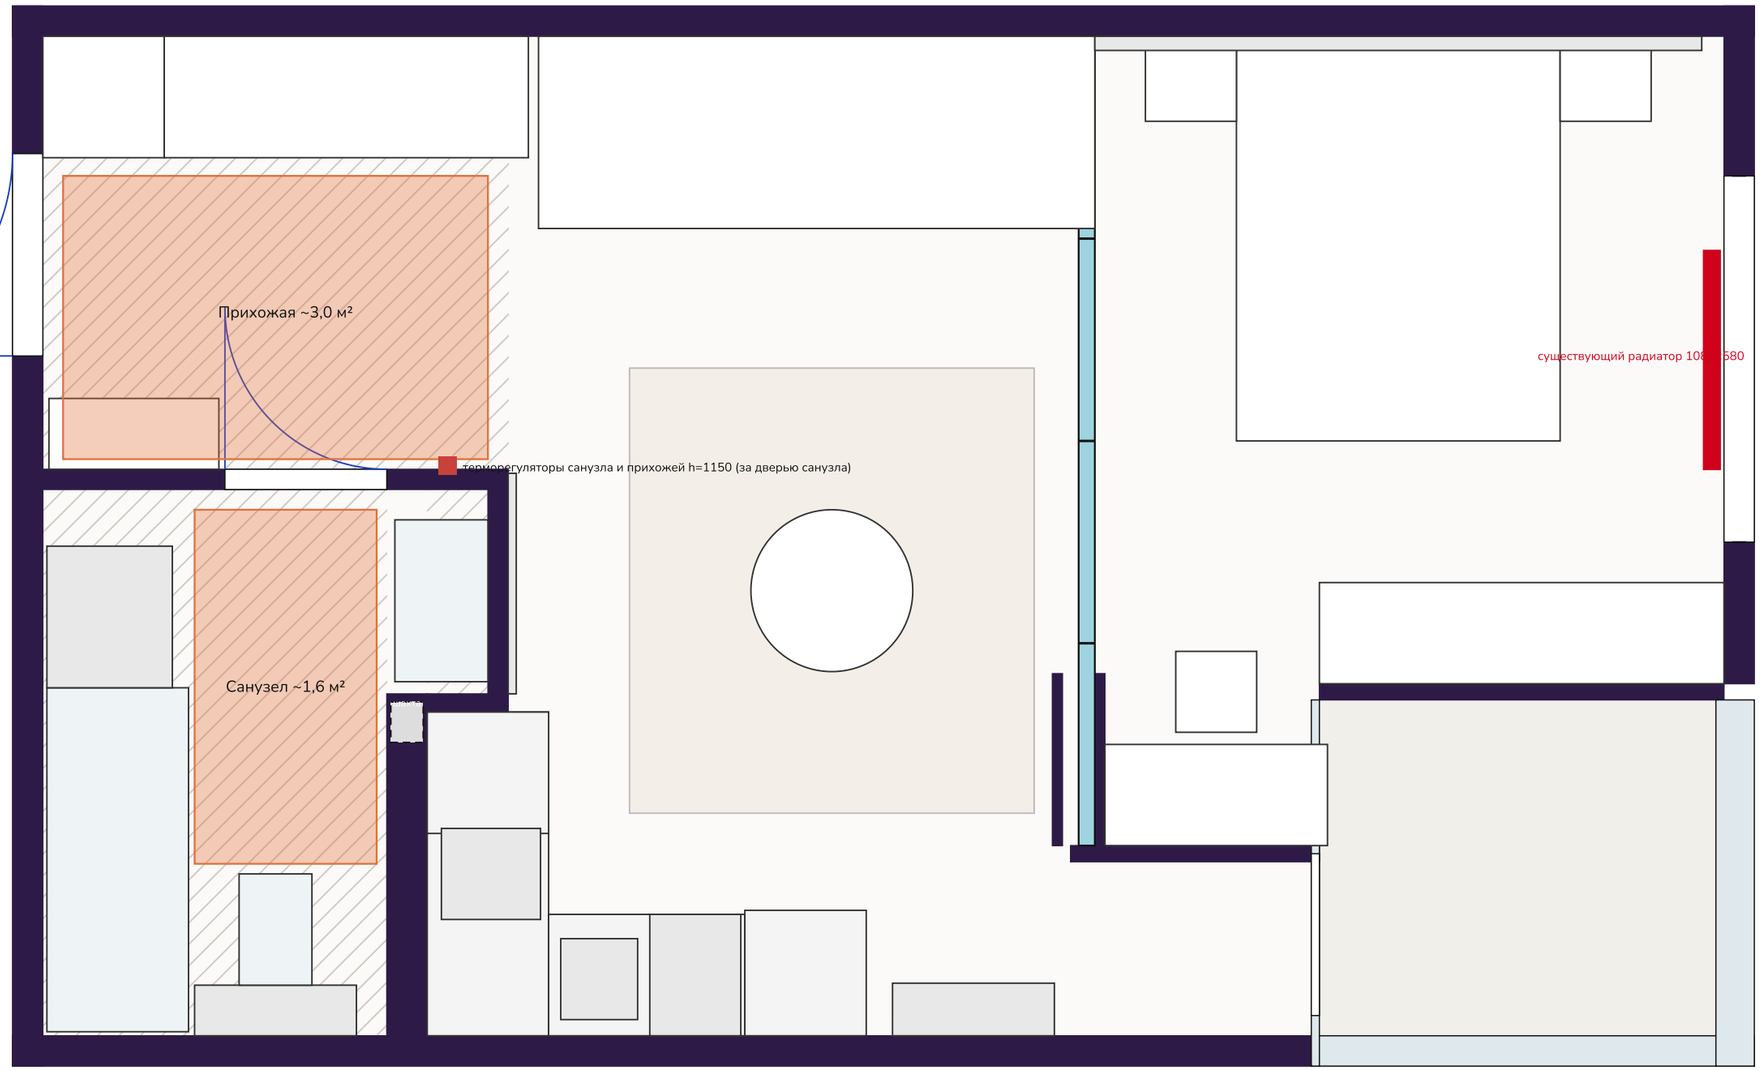

Условные обозначения

- Радиатор отопления (существующий)
- Нагревательный мат 150 Вт/м² под плитку
- Терморегулятор с датчиком пола

Ведомость

Элемент	Кол-во
Радиатор под окном 1080×580	1 шт
Тёплый пол прихожая	3,0 м²
Тёплый пол санузел	1,6 м²
Терморегуляторы (один блок, 2 шт)	2 шт
Полотенцесушитель электрический	1 шт

ПРИМЕЧАНИЯ:


1. За отметку 0.000 принят уровень чистового пола.
2. Все размеры уточнить по месту перед началом работ; привязки даны по неоштукатуренным стенам.
3. Размеры в миллиметрах, площади в м². Планировка — по эскизу владельца от 09.11.2026.
4. Мат не кладут под шкаф, сиденье, ванну, колонну, инсталляцию и тумбу. Датчик — в гофре между витками. Включать через 28 дней после укладки плитки.
5. Радиатор не переносится; шторы — над радиатором, карниз скрытый в потолке.

Стадия	Лист	Листов	Квартира 72 · ЖК Buta Zaman · Алматы
РД	11	21	План радиаторов и тёплых полов 09.11.2026 · М 1:30 · А3


КВАРТИРА 72


Развёртка стен: кухня

A · выступ санузла (z=1900)

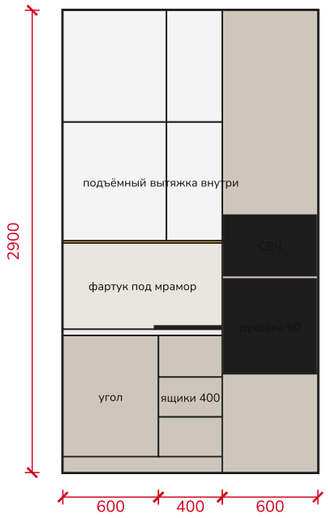

B · правая стена (x=0)

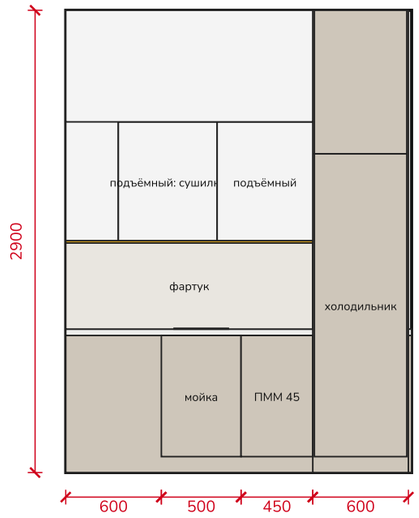

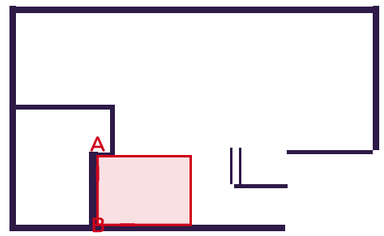

ключ-план

Стена под краску

2,5 м²

над колоннами, торцы

Размеры по оси A: угол 600, ящики 400 с варочной 450, колонна 600; по оси B: угол 600, мойка 500, ПММ 450, колонна холодильника 600, торец до 2170.

Отметки: столешница 900 · фартук 900–1450 · верх 1450 — потолок (2800) · розетки над столешницей h=1100 · LED под верхними шкафами · вытяжка встроенная в подъёмный шкаф над варочной.

Низ и колонны — МДФ грейж мат, верх — белый мат, без ручек (push / интегрированный профиль). Столешница кварц белый 20–30 мм, фартук керамогранит под мрамор. Мойка чёрная под столешницу + чёрный смеситель.

Колонна A: ящик 100–600, духовка 620–1215, СВЧ 1235–1615, шкаф выше. Колонна B: холодильник встраиваемый под фасад до 2000, антресоль с розеткой. Варочная 45 (3 конфорки) над ящиками 400.


ПРИМЕЧАНИЯ:


1. За отметку 0.000 принят уровень чистового пола.
2. Все размеры уточнить по месту перед началом работ; привязки даны по неоштукатуренным стенам.
3. Размеры в миллиметрах, площади в м². Планировка — по эскизу владельца от 09.11.2026.
4. Замер кухни — после штукатурки и потолка, установка — после пола. Глухой угол — механизм «волшебный угол» (LeMans) за дверцей 600 у правой стены.

Стадия	Лист	Листов	Квартира 72 · ЖК Buta Zaman · Алматы
РД	12	21	Развёртка стен: кухня 09.11.2026 · M 1:38 · A3

КВАРТИРА 72

Развёртка стен: санузел

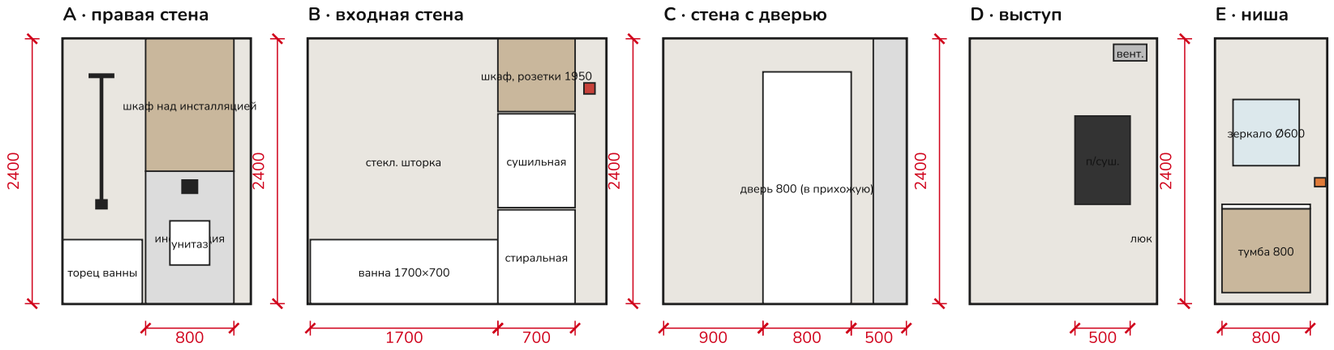

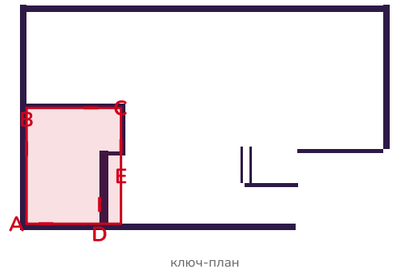

ключ-план

Стена под краску
0 м²
керамогранит ~21 м²

Санузел 2700 × 1700 + ниша раковины 1010 × 300 (между выступом и стенкой за ТВ); h 2400 (натяжной). Керамогранит 600×1200 стены и пол, швы 2 мм. Стены ~21 м², пол ~4,9 м².

Ванна 1700×700 вдоль входной стены, у правой стены — смеситель h 900 и тропический душ h 2100, стеклянная шторка 800. Рядом колонна: стиральная внизу, сушильная сверху, над ними шкаф до потолка с розетками (h 1950).

Правая стена: инсталляция 800 с подвесным унитазом (ось 1150), над ней шкаф под дерево до потолка. Полотенцесушитель — на выступе. Раковина 800 с круглым зеркалом Ø600 — в нише у кухни, розетка IP44 h 1100 сбоку.

Дверь 800 открывается в прихожую, петли у консоли. Гидроизоляция обмазочная: пол + стены на 300, зона ванны и душа — на 2000. Люк к кранам и счётчикам — в выступе.

ПРИМЕЧАНИЯ:


1. За отметку 0.000 принят уровень чистового пола.
2. Все размеры уточнить по месту перед началом работ; привязки даны по неоштукатуренным стенам.
3. Размеры в миллиметрах, площади в м². Планировка — по эскизу владельца от 09.11.2026.
4. Стояки и вентканалы — внутри выступа 1690×200. Слив унитаза Ø110 ~1,2 м к стояку вдоль правой стены — проверить уклон 2 см/м.
5. Колонна стиралка+сушилка 700×650: вода h 650, слив h 450 за машиной, аквастоп; сушилка конденсационная.

Стадия	Лист	Листов	Квартира 72 · ЖК Buta Zaman · Алматы
РД	13	21	Развёртка стен: санузел 09.11.2026 · М 1:55 · А3


КВАРТИРА 72

Развёртка стен: прихожая


A · левая стена: сиденье + шкаф

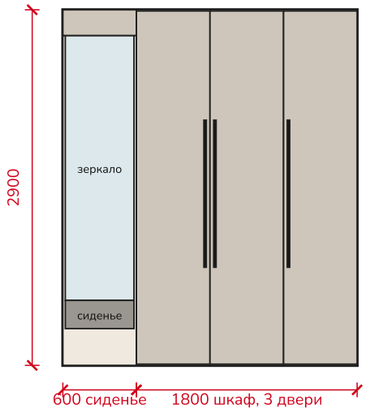


B · стена санузла

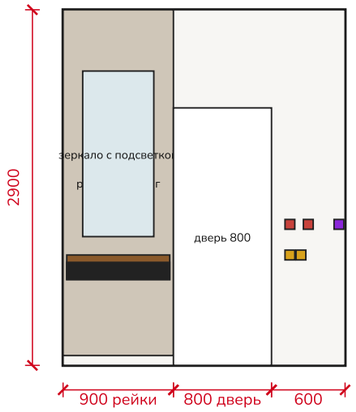

C · входная стена

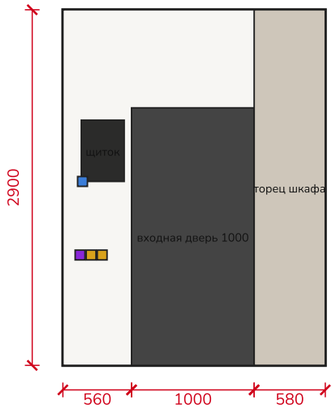

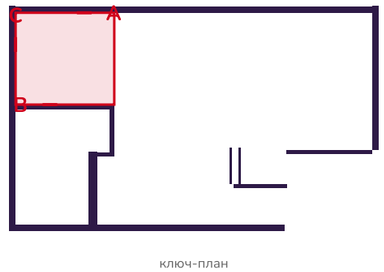

ключ-план

Стена под краску

4,5 м²

без шкафа, реек, дверей

Шкаф 2400×600 до потолка, фасады МДФ грейж мат с чёрными ручками-скобами 1200: у входа ниша 600 с мягким сиденьем (h 300–530) и зеркалом во всю стену ниши, LED сверху и под сиденьем; далее 3 двери по 600, в первой секции — поворотная обувница.

Стена санузла: рейки-флутинг 900 на всю высоту, консоль 840×350 (орех + 2 чёрных ящика) h 700–900 с LED снизу, зеркало 580×1340 в чёрной рамке с тёплой подсветкой по контуру (h 1050–2400). Розетка под консолью h 300.

Входная стена между санузлом и дверью (560): блок h 900 — мастер-выключатель, свет прихожей, подсветка зеркал и сиденья; домофон h 1500; щиток над блоком (верх ~2000). Выключатели санузла и терморегуляторы — за дверью санузла со стороны гостиной.

ПРИМЕЧАНИЯ:


1. За отметку 0.000 принят уровень чистового пола.
2. Все размеры уточнить по месту перед началом работ; привязки даны по неоштукатуренным стенам.
3. Размеры в миллиметрах, площади в м². Планировка — по эскизу владельца от 09.11.2026.
4. Пол прихожей — керамогранит Medici PM213460 200×200 с тёплым полом; раскладку начинать от шкафа целой плиткой; порожек на границе с ламинатом по линии z=2300.

Стадия	Лист	Листов	Квартира 72 · ЖК Buta Zaman · Алматы
РД	14	21	Развёртка стен: прихожая 09.11.2026 · M 1:50 · A3


КВАРТИРА 72

Развёртка стен: гостиная


A · ТВ-стена

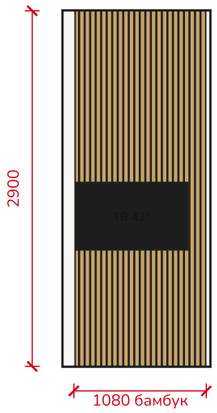


B · левая стена: диван

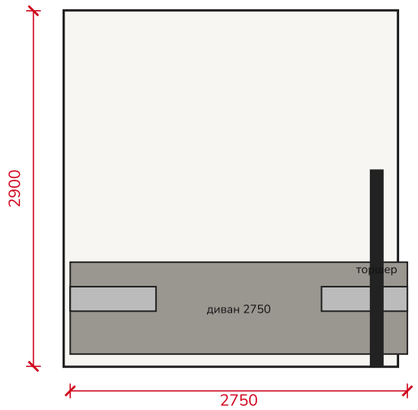

C · перегородка 4 м (z=5120)

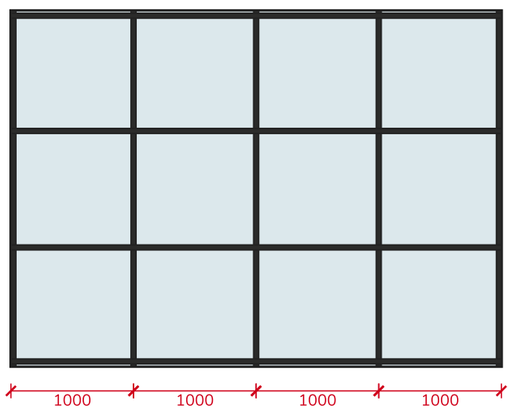

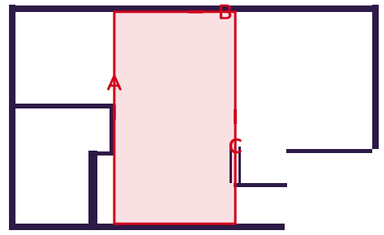

ключ-план

Стена под краску
14,0 м²
гостиная + кухня

ТВ-стена: стена санузла со стороны гостиной (1200 × 2900) — бамбуковые стволы Ø40 вплотную на всю высоту, ТВ 43" на кронштейне сквозь бамбук в закладную (h центра 1200). За ТВ: 2 розетки + интернет h 1100, труба к розетке h 300.

Диван 2750 вдоль левой стены, за ним розетки h 300 и розетка с USB h 700 у подлокотника; проходной выключатель гостиной — у перегородки h 1000. Кондиционер — на правой стене над кухней (z 4,2–5,0, низ h 2550), трасса на балкон.

Перегородка (z=5120): 4 стеклянные створки по 1000 в чёрном профиле с переплётом, до потолка; уезжают в карман 850 у короткой стены. Направляющая — к закладному брусу.

ПРИМЕЧАНИЯ:


1. За отметку 0.000 принят уровень чистового пола.
2. Все размеры уточнить по месту перед началом работ; привязки даны по неоштукатуренным стенам.
3. Размеры в миллиметрах, площади в м². Планировка — по эскизу владельца от 09.11.2026.

Стадия	Лист	Листов	Квартира 72 · ЖК Buta Zaman · Алматы
РД	15	21	Развёртка стен: гостиная 09.11.2026 · М 1:50 · А3


КВАРТИРА 72

Развёртка стен: спальня


A · стена с окном

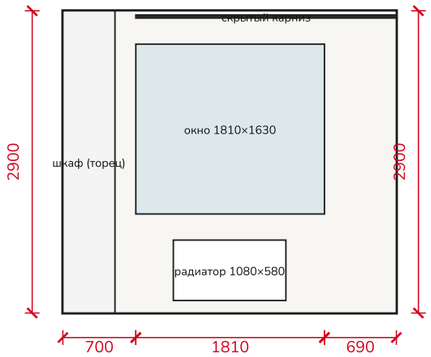


B · изголовье 3000

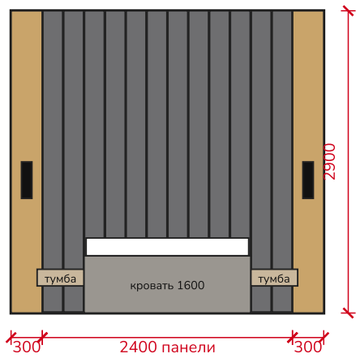


C · шкаф у балкона

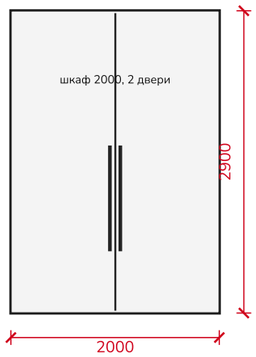

D · стол

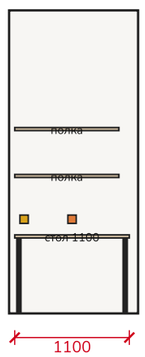

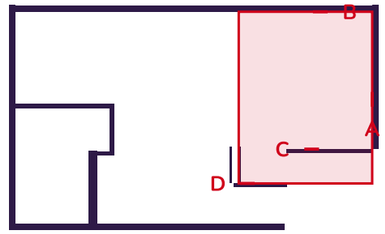

ключ-план

Стена под краску

8,5 м²

без изголовья и шкафа

Изголовье 3000 × 2900 по центру левой стены (z 5,2–8,2): по краям рейки дуб 300 (15/шаг 30, глубина 20) с LED у внутренней кромки, в центре 12 мягких серых панелей 190 × 2900 (шов 10), чёрные бра h 1200, подвесные тумбы дуб 450 (h 260–420).

Кровать 160×200, основание серое h 350, матрас до 550. У каждой тумбы: розетка USB-C h 550, выключатели бра + общий свет h 750 (проходные). Шкаф 500 × 2000 до потолка вдоль стены балкона, 2 двери. Стол 1100 × 500 у короткой стены, полки на h 1300 и 1750.

Окно: низ 950, верх 2580; скрытый карниз в нише потолка на всю ширину стены. Выключатель спальни (проходной) — на короткой стене у стола h 900. Шторы — окно спальни и вход на балкон.


ПРИМЕЧАНИЯ:

1. За отметку 0.000 принят уровень чистового пола.
2. Все размеры уточнить по месту перед началом работ; привязки даны по неоштукатуренным стенам.
3. Размеры в миллиметрах, площади в м². Планировка — по эскизу владельца от 09.11.2026.

Стадия	Лист	Листов	Квартира 72 · ЖК Buta Zaman · Алматы
РД	16	21	Развёртка стен: спальня 09.11.2026 · M 1:58 · A3

Мебель: схема

КВАРТИРА 72

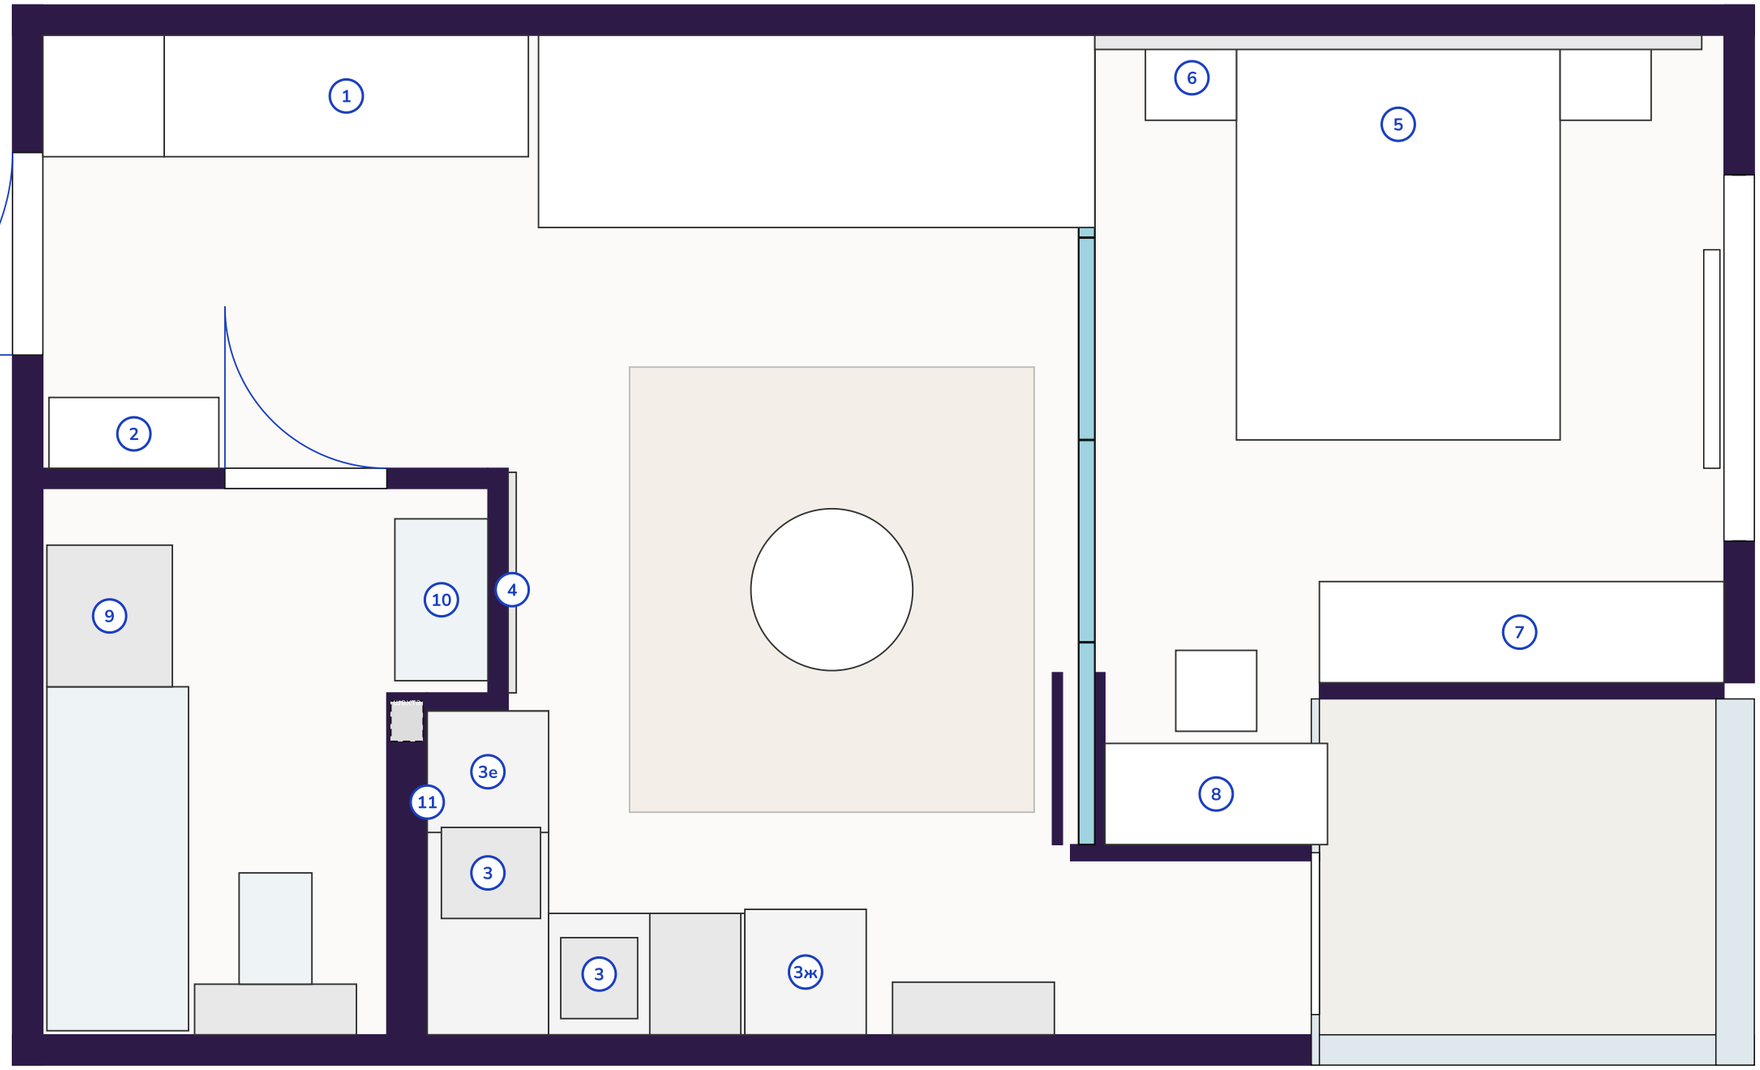

Изделия по схеме

№	Изделие
1	Шкаф прихожей с сиденьем и зеркалом
2	Консоль, зеркало и рейки у санузла
3	Кухня: низ, столешница, верх, колонны 3е и 3ж
4	Бамбук на ТВ-стене
5	Изголовье с рейками и панелями
6	Подвесные тумбы у кровати (2)
7	Шкаф спальни 500×2000
8	Стол и 2 полки у короткой стены
9	Шкаф над колонной стиралка+сушилка
10	Тумба с раковиной 800, санузел
11	Шкаф над инсталляцией, санузел

Размеры — на следующем листе.

ПРИМЕЧАНИЯ:

1. За отметку 0.000 принят уровень чистового пола.
2. Все размеры уточнить по месту перед началом работ; привязки даны по неоштукатуренным стенам.
3. Размеры в миллиметрах, площади в м². Планировка — по эскизу владельца от 09.11.2026.
4. Схема показывает расположение. Точные размеры мебельщик снимает на замере после чистовых стен, пола и натяжного потолка.

Стадия	Лист	Листов	Квартира 72 · ЖК Buta Zaman · Алматы
РД	17	21	Мебель: схема 09.11.2026 · М 1:30 · А3

Мебель: размеры для мебельщика

Встроенная и заказная мебель


№	Изделие	Ш × Г × В, мм	Исполнение и привязки
1	Шкаф прихожей	2400 × 600 × до потолка	У входа ниша 600: мягкое сиденье h 300–530, зеркало на всю стену ниши (от 530 до короба), LED сверху и под сиденьем. Далее 3 распашные двери по 600, МДФ грейж мат, чёрные ручки 1200. В 1-й секции — поворотная обувница, во 2-й — штанга, антресоль 2400–2800.
2	Консоль + зеркало + рейки	900 × 350 × 2900	На стене санузла справа от двери: рейки-флутинг 900 на всю высоту; консоль 840×350 h 700–900 (столешница орех 60, 2 чёрных ящика), LED снизу; зеркало 580×1340 в чёрной рамке с LED по контуру, низ h 1050. Закладная в каркасной стене.
3а	Кухня низ, выступ	1600 × 600 × 860	От правой стены: угол 600 с механизмом «волшебный угол» (дверь 600 на стороне В), ящики 400 (3 шт) под варочной 450. Цоколь 100 чёрный. Фасады грейж мат.
3б	Кухня низ, правая стена	2170 × 600 × 860	От угла: мойка 500 (чёрная под столешницу), ПММ 45 встроенная, колонна холодильника 600 (поз. 5). Цоколь 100.
3в	Столешница	Г 1600 + 2170 × 620	Кварцевый агломерат белый 20–30 мм, верх h 900. Вырезы: варочная 450 (у выступа), мойка под столешницу ~400×380 (правая стена). Фартук 900–1450 керамогранит под мрамор — не в заказ мебели.
3г	Кухня верх	1000 + 1550 × 350 × 1350	h 1450 — потолок 2800, в 2 ряда (1450–2200 подъёмные, 2200–2800 глухие). Над варочной — встраиваемая вытяжка 600 внутри подъёмного шкафа; над мойкой — сушилка; верх по стене В от углового шкафа до колонны холодильника без зазора. Белый мат без ручек.
3е	Колонна духовка + СВЧ (в составе кухни)	600 × 600 × до потолка	У выступа, торец к гостиной (грейж). Ящик 100–600, духовка 60 (620–1215), СВЧ встраиваемая (1235–1615), дверь выше. Розетки духовки и СВЧ внутри над СВЧ h 1900.
3ж	Колонна холодильника (в составе кухни)	600 × 600 × до потолка	Правая стена, конец кухни (z 3,47–4,07). Фасад до 2000 + антресоль, розетка в антресоли h 2150. Холодильник встраиваемый под фасад; вентзазоры по паспорту.
4	Бамбук на ТВ-стене	1080 × 40 × 2900	Стволы Ø40 вплотную (~24 шт) на подложке 12 мм по стене санузла со стороны гостиной (x 1,69–2,78, z 2,3). Кронштейн ТВ — сквозь бамбук в закладную OSB. Отверстия под кабели.
5	Изголовье	3000 × 70 × 2900	Центр левой стены спальни (z 5,2–8,2): рейки дуб 300 (15/30/20) слева и справа, LED у кромки; центр 2400 — 12 мягких панелей 190 × 2900 серая ткань на фанере, шов 10; бра чёрные h 1200 на рейках (вывод за рейками).
6	Тумбы подвесные	450 × 350 × 160, 2 шт	Дуб, с ящиком, низ h 260, верх h 420; крепление к изголовью/стене. Над тумбами розетка USB-C h 550 и блок выключателей h 750.
7	Шкаф спальни	500 × 2000 × до потолка	Вдоль стены балкона (x 1,74–2,24), 2 распашные двери 1000 МДФ белый, ручки-профили. Штанга + полки.
8	Стол + 2 полки	1100 × 500 × 750	У короткой стены со стороны спальни (x 0,94), столешница дуб 40 на чёрных ножках; полки 1000 × 250 на h 1300 и 1750. Розетка 2 + USB h 900 над столом.
9	Шкаф над колонной стиралка+сушилка	700 × 650 × 660	Санузел, входная стена: низ h 1740 — потолок 2400. 2 фасада влагостойкие под дерево, внутри розетки стиралки и сушилки h 1950. Колонна стоит на полу: стиральная 850, сушильная 850 на кронштейне.
10	Тумба с раковиной	800 × 460 × 860	В нише у кухни (x 1,75–2,55, z 1,9–2,2): подвесная или на ножках, 2 фасада под дерево, раковина накладная/встроенная, верх h 900. Круглое зеркало Ø600 с подсветкой, h 1250–1850.
11	Шкаф над инсталляцией	800 × 250 × 1200	Правая стена санузла над инсталляцией (z 0,75–1,55): h 1200 — потолок 2400, 2 фасада под дерево, влагостойкий. Доступ к инсталляции — через кнопку.

Покупная мебель (для проверки места)	Размер, мм
Диван	2750 × 950
Кровать	1600 × 2000, h 350
Журнальный столик	Ø 800
Стул к столу	450 × 450
Ванна	1700 × 700
Стиральная / сушильная машины	600 × 600 × 850 каждая


ПРИМЕЧАНИЯ:

1. Высота: черновой потолок 2900, натяжной ~2800 (санузел 2400). Все шкафы до потолка без зазора: корпус на 30–50 мм ниже, сверху доборная планка в цвет фасада, подрезка по месту.
2. Закладной брус под линией фасадов ставят до натяжного потолка (лист «План потолка»). Замер мебели — только после монтажа потолка и чистовых стен и пола.
3. Стены санузла и ТВ-стена каркасные: всё навесное (ТВ, консоль, зеркало, шкаф над колонной) крепится в закладные OSB 18, положение закладных — по листу «План монтажа перегородок».
4. Материалы: корпуса ЛДСП, фасады МДФ (кухня низ и колонны — грейж мат, верх — белый мат, прихожая — грейж), санузел — влагостойкие материалы под дерево. Петли и направляющие с доводчиком.
5. Техника: варочная 45 (3 конфорки), духовка 60, СВЧ встраиваемая, вытяжка 60 встраиваемая, холодильник встраиваемый под фасад, ПММ 45, стиральная и сушильная 60 см. Размеры техники сверить перед заказом мебели.
6. Размеры — проектные. Окончательные снимает мебельщик по месту и согласует с заказчиком.


Визуализация 1

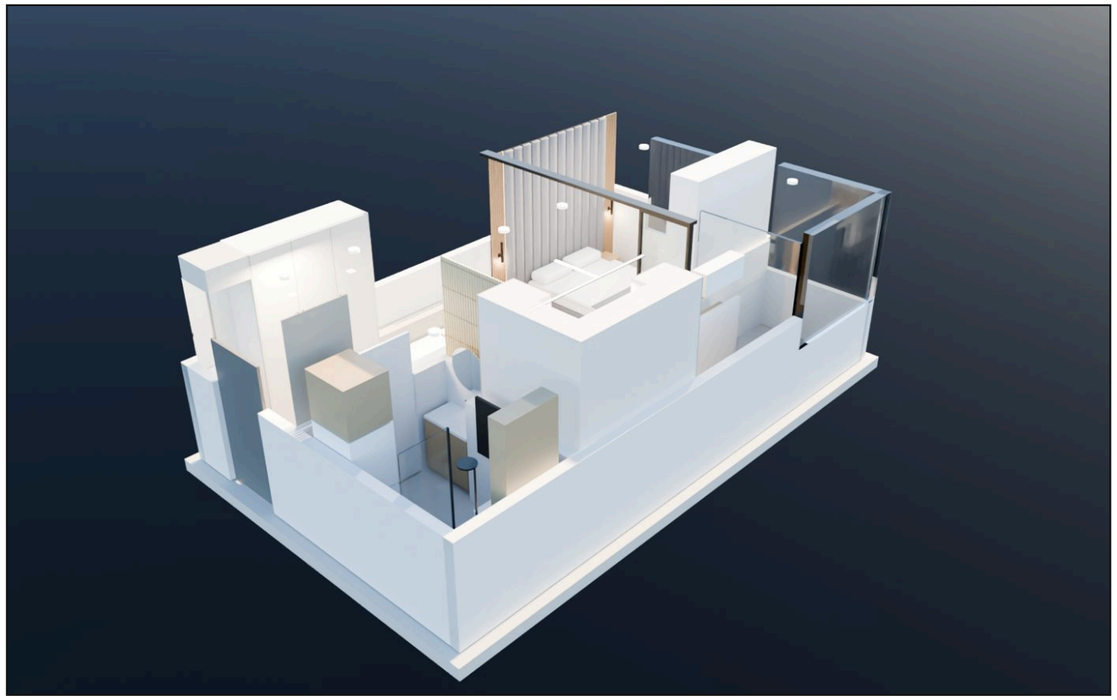

Общий вид (стены срезаны на 1,5 м)

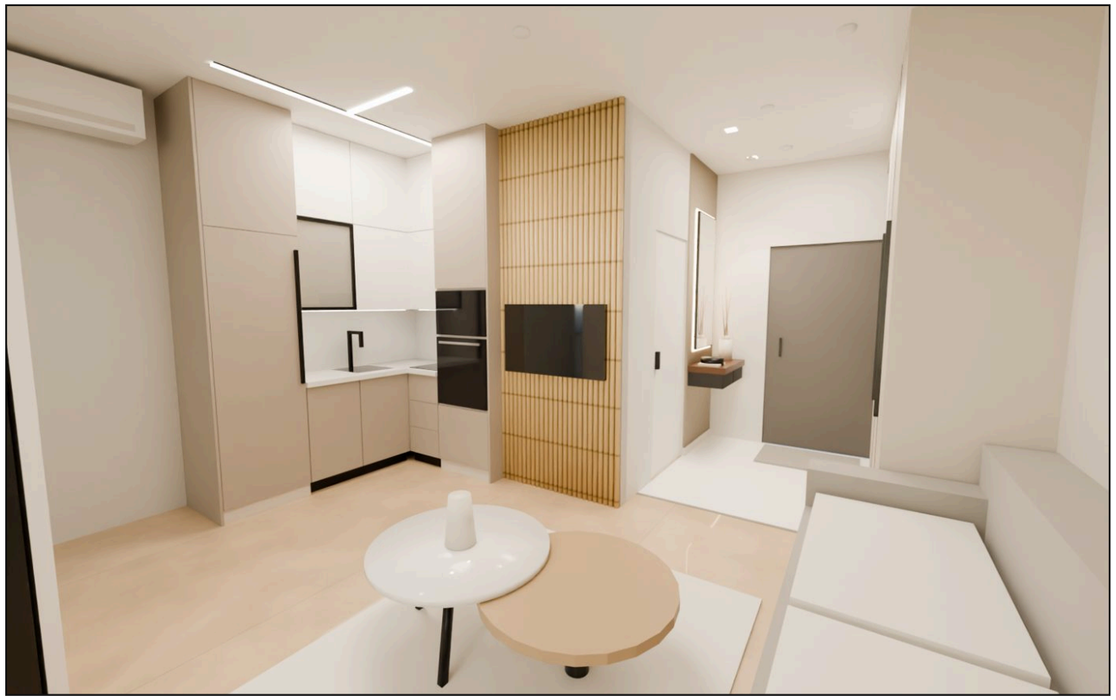

Гостиная: диван, ТВ-стена в бамбуке, кухня

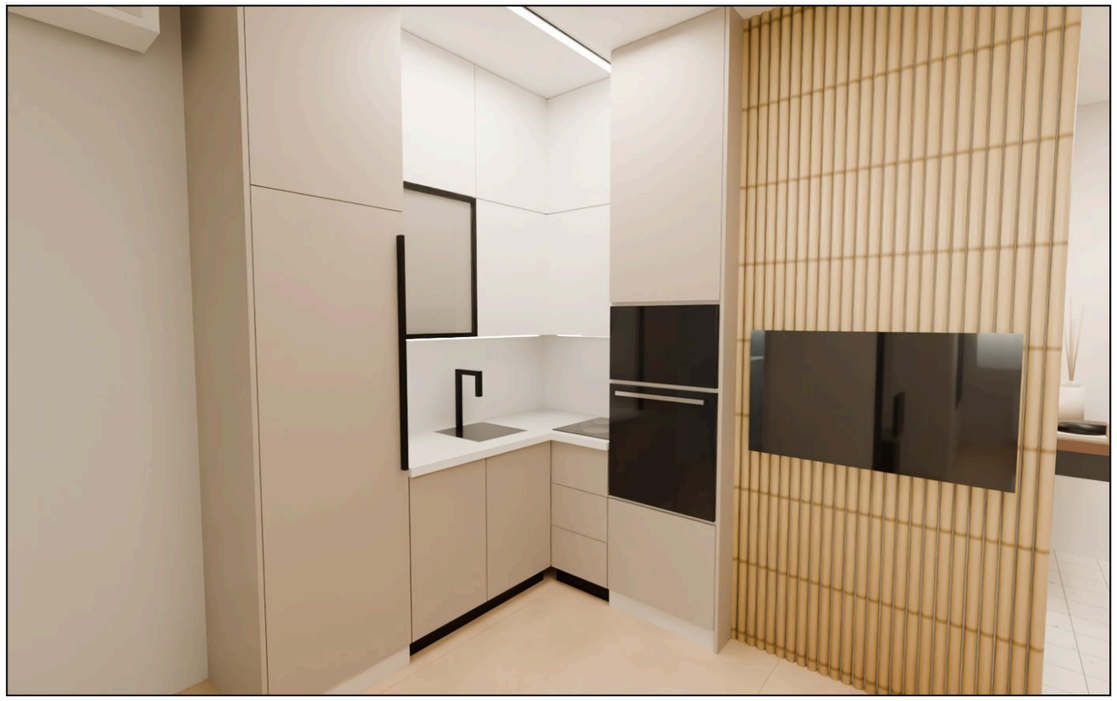


Кухня: две колонны, варочная 45




Вид с дивана на кухню и вход

Стадия	Лист	Листов	Квартира 72 · ЖК Buta Zaman · Алматы
РД	19	21	Визуализация 1 09.11.2026 · M — · A3


Визуализация 2

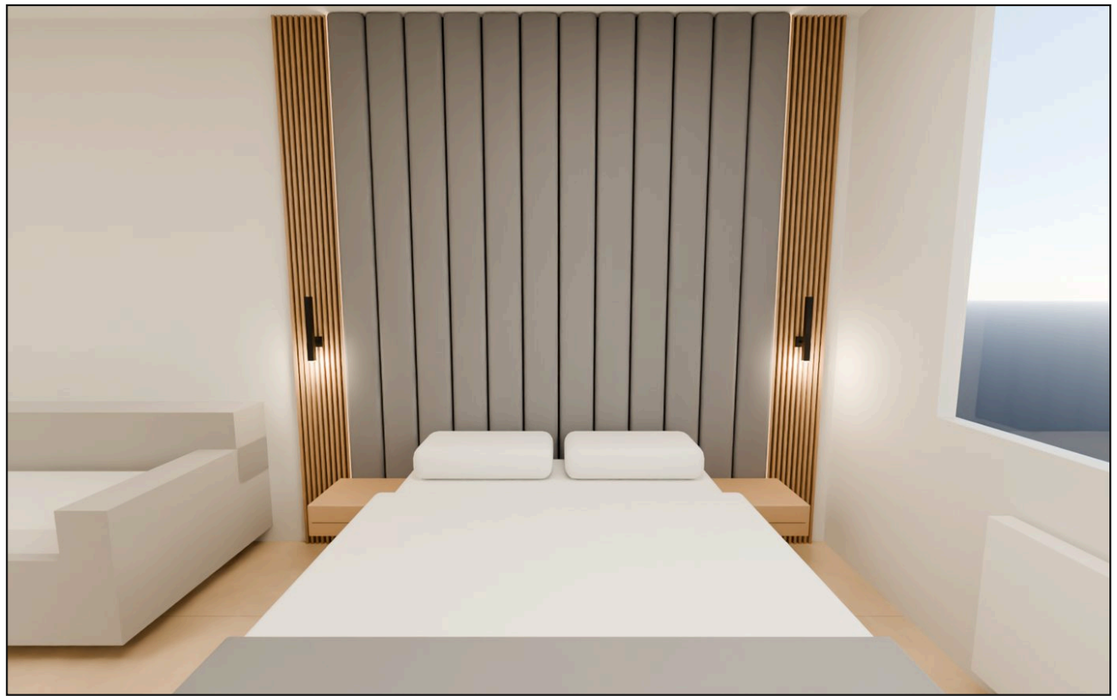

Спальня: изголовье 3 м до потолка, кровать 160

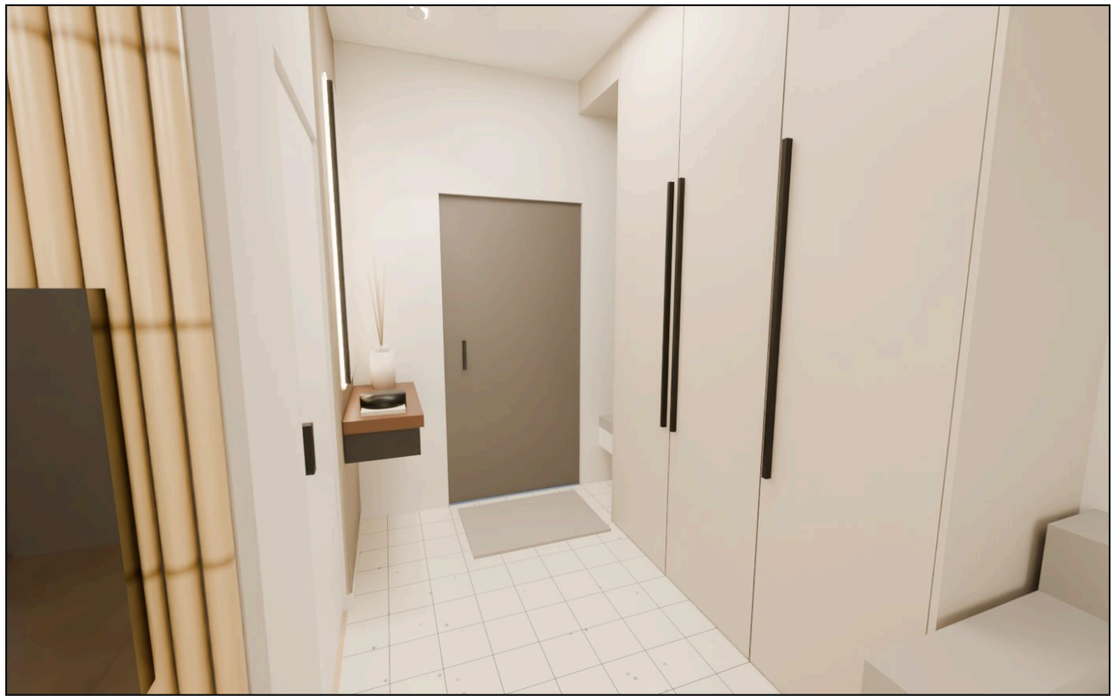

Прихожая: сиденье с зеркалом, шкаф, консоль

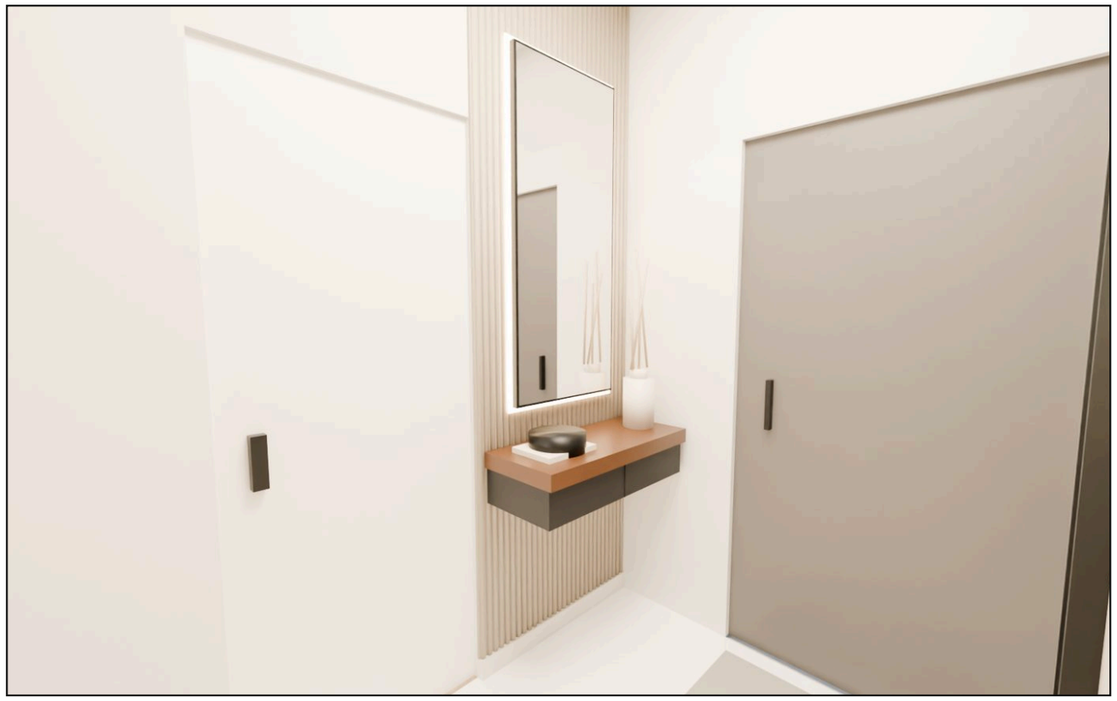

Консоль с зеркалом у двери санузла



Спальня: шкаф, стол у короткой стены, вид на кухню

Стадия	Лист	Листов	Квартира 72 · ЖК Buta Zaman · Алматы
РД	20	21	Визуализация 2 09.11.2026 · M — · A3

Ведомость материалов

Отделка помещений

№	Помещение	Пол	Стены	Потолок	Площадь
1	Прихожая	Керамогранит 200×200 + тёплый пол	Краска; рейки у санузла	Натяжной	~4,0 м²
2	Санузел	Керамогранит 600×1200 + тёплый пол	Керамогранит 600×1200	Натяжной влагост. 2400	~4,9 м²
3	Кухня	Ламинат 33 кл.	Краска; фартук под мрамор	Натяжной со световыми линиями	~5,5 м²
4	Гостиная	Ламинат 33 кл.	Краска; ТВ-стена — бамбук	Натяжной	~12 м²
5	Спальня	Ламинат 33 кл.	Краска; изголовье панели + рейки	Натяжной	~9,9 м²
6	Балкон	Керамогранит	Краска	Покраска / натяжной	3,3 м²

Ведомость отделки

Элемент	Кол-во
Ламинат (с запасом 10%)	28,5 м²
Керамогранит пол	14 м²
Керамогранит стены санузла	23 м²
Фартук кухни	2,5 м²
ГКЛ влагостойкий	22 листа
Стены под покраску	~75 м²
Натяжной потолок	~34 м²
Плинтус	30 м
Нагревательный мат	5,5 м²

Ведомость электрики

Электрика	Кол-во
Розетки	19
Силовые выводы и терморегуляторы	8
Выключатели, мастер и выводы света	34
Слаботочные точки	3
Споты встраиваемые	8
Световые линии / бра	2 / 2
LED-лента	15 м
Терморегуляторы	2

Ведомость сантехники

Сантехника	Кол-во
Ванна акриловая 1700×700	1
Унитаз подвесной + инсталляция	1
Тумба с раковиной 800	1
Смесители (ванна/душ, раковина, кухня)	3
Мойка кухонная чёрная	1
Полотенцесушитель эл.	1
Точки воды / канализации	16

Палитра

Стены: светло-серый тёплый

Потолок, верх кухни: белый мат

Фасады: грейж мат

Пол: светлый дуб

Бамбук, рейки дуб

Панели изголовья: серая ткань

Профили, ручки, бра: чёрный мат

Встроенная мебель: шкаф 2400 с сиденьем и зеркалом; консоль с зеркалом и рейками; кухня Г 1,6 + 2,17 с двумя колоннами; бамбук на ТВ-стене; изголовье 3 м; шкаф спальни 500×2000; стол 1100; шкафы санузла; стеклянная перегородка 4 м с карманом.

Техника: холодильник встраиваемый, варочная 45, духовка, СВЧ, вытяжка, ПММ 45, стиральная и сушильная машины, кондиционер, телевизор 43".

Стадия	Лист	Листов	Квартира 72 · ЖК Buta Zaman · Алматы
РД	21	21	Ведомость материалов 09.11.2026 · М — · А3